

ASSESSOR REFERENCE:  
MAP 504 BLOCK 245 LOT 3

## WASHINGTON STREET

PUBLIC - NORTH VARIES  
1871 E.C.L.D. No. 1205


0106 645:24  
PLANNING  
ENGINEER

| REQUIRED PARKING               |           |
|--------------------------------|-----------|
| 512 WASHINGTON - BLDGS 1, 2, 3 | 13 SPACES |

### ZONING TABLE: RH ZONING DISTRICT (MULTI-FAMILY)

| DESCRIPTION                | REQUIRED    |
|----------------------------|-------------|
| MINIMUM LOT FRONTAGE (FT.) | 150'-0"     |
| MINIMUM LOT AREA (S.F.)    | 40,000 S.F. |
| MINIMUM FRONT YARD (FT.)   | 25'-0"      |
| MINIMUM SIDE YARD (FT.)    | 20'-0"      |
| MINIMUM REAR YARD (FT.)    | 40'-0"      |
| MINIMUM OPENSPACE          | 35%         |
| MINIMUM LOT DEPTH          | 200'-0"     |

1/2" J. JOSEPH L. ABOUZEK  
8220 WASHINGTON ST.  
MAP 504 BLOCK 245 LOT 4  
BK. 31500 PG. 176

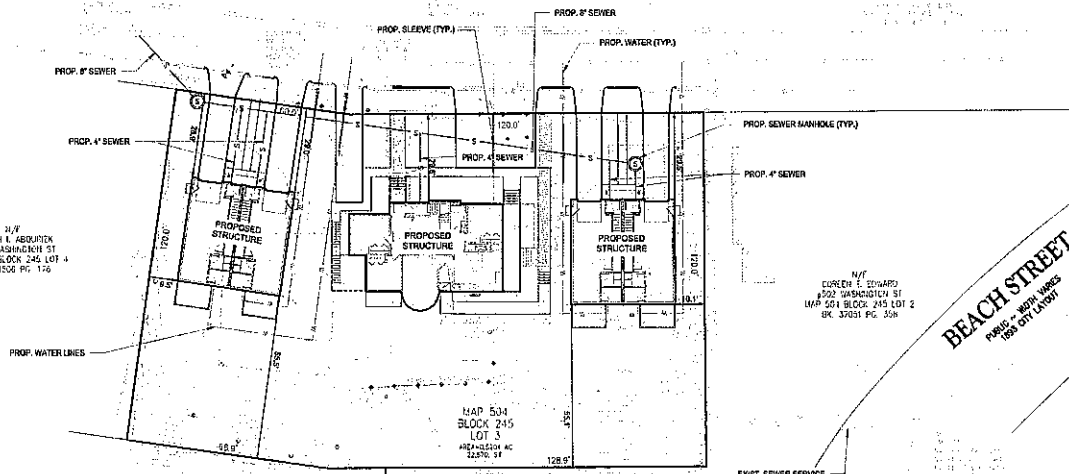

### OWNER & APPLICANT:

ESSEX COUNTY HABITAT FOR HUMANITY  
14 PARK ST  
DANVERS, MA 01923

### KEY REFERENCE DEEDS:

- DEED FROM FEDERAL MORTGAGE ASSOCIATION TO KEITH F. BOUCHER AND DIANE C. BOUCHER DATED MAY 17, 2012 AND RECORDED AT THE SOUTH ESSEX REGISTRY OF DEEDS BOOK 31356 PAGE 76.
- DEED FROM PAUL H. AND THANA H. TO SOCRATES & POTOLIA VANNIAKOURIS DATED NOV 5, 1973 AND RECORDED AT THE SOUTH ESSEX REGISTRY OF DEEDS BOOK 6081 PAGE 776.

### KEY REFERENCE PLANS:

- PLAN OF A PORTION OF WASHINGTON STREET, HAVERHILL, MASS. AS OWNED BY THE COUNTY COMMISSIONERS, BY N. SPOFFORD, SURVEYOR, DATED 1871 AND RECORDED AT THE SOUTH ESSEX REGISTRY OF DEEDS E.C.L.D. No. 1205.
- PLAN OF A PORTION OF BEACH STREET, HAVERHILL, MASS. BY JOHN T. DESHOND, CITY ENGINEER, DATED APRIL, 1893 AND ON FILE WITH THE CITY OF HAVERHILL ENGINEERING DEPARTMENT, SECTION 3A PLAN 20.
- PLAN OF A PORTION OF WILSON STREET, BEACH ST. TO RIVER ST. FOR ACCEPTANCE, BY HARRY W. BAILEY, CITY ENGINEER, DATED SEPT. 1947, ON FILE WITH THE CITY OF HAVERHILL ENGINEERING DEPARTMENT AND RECORDED AT THE SOUTH ESSEX REGISTRY OF DEEDS PLAN BOOK 79 PLAN 51.
- PLAN OF A PORTION OF THE BOWLEY ESTATE, HAVERHILL, MASS. BY N. SPOFFORD, SURVEYOR, DATED FEB. 15, 1900 AND RECORDED AT THE SOUTH ESSEX REGISTRY OF DEEDS PLAN BOOK 12 PLAN 18.

### GENERAL NOTES:

- THE EXISTING CONDITIONS SHOWN HEREON ARE TAKEN FROM AN EXISTING CONDITIONS PLAN DATED NOVEMBER 27, 2024, PREPARED AND SIGNED/STAMPED BY MICHAEL J. SERGI, PROFESSIONAL LAND SURVEYOR.
- THE SUBJECT PROPERTY IS NOT LOCATED WITHIN ANY FLOOD ZONE AS ILLUSTRATED BY FEMA MAP 2500000080F; EFFECTIVE JULY 3, 2012.
- ELEVATIONS HEREON ARE BASED ON NAVD83.
- ORIENTATION IS TO MASSACHUSETTS STATE PLANE COORDINATES.
- HORIZONTAL LOCATION OF SITE BENCHMARKS SHOWN ARE APPROXIMATE.
- THE LOCATION OF ALL UNDERGROUND UTILITIES SHOWN HEREON ARE APPROXIMATE AND ARE BASED ON A COMBINATION OF FIELD LOCATIONS AND RECORD DATA ON FILE WITH THE CITY OF HAVERHILL ENGINEERING DEPARTMENT.
- THE SUBJECT PROPERTY IS BENEFITED BY A SEWER EASEMENT CROSSING ADJUTHO PROPERTY AT 4502 WASHINGTON STREET TO BEACH STREET AS DESCRIBED IN KEY REFERENCE DEED 2. THIS EASEMENT IS BLANKET IN NATURE AND NOT PLOTTABLE.

### LEGEND

- BENCHMARK
- CATCH BASIN
- DRAIN MANHOLE
- HYDRANT
- SEWER MANHOLE
- WATER GATE VALVE
- WATER SHUT-OFF
- UTILITY POLE
- CONTOUR MAJOR
- CONTOUR MINOR
- DRAIN LINE
- GAS LINE
- OVERHEAD WIRES
- SEWER LINE
- WATER LINE

### ABBREVIATIONS

- CB CATCH BASIN
- CLF CHAINLINK FENCE
- DMH DRAIN MANHOLE
- EP EDGE OF PAVEMENT
- HYD HYDRANT
- HYD HYDRANT
- SMH SEWER MANHOLE
- VCC VERTICAL GRANITE CURB
- WFD WOOD-FRAMED DWELLING
- WG WATER GATE VALVE
- WDO WATER SHUT-OFF

1/2" STEPHEN & KATHLEEN PARKINS  
4121-123 WALSON ST  
MAP 500 BLOCK 252A LOT 13  
BK. 37478 PG. 441

1/2" RICHARD ALVARADO LUIS  
1121-123 WALSON ST  
MAP 500 BLOCK 252A LOT 14  
BK. 37478 PG. 441

1/2" NATALIE MCGOUGH  
4101-100 WALSON ST  
MAP 504 BLOCK 245 LOT 5  
BK. 34456 PG. 124

SCALE: 1"=20'  
20 0 20 40 FT



PCA

Tighe & Bond

The Morin-Cameron GROUP, INC.

CIVIL ENGINEERS (ENVIRONMENTAL CONSULTANTS)  
LAND SURVEYORS (LAND USE PLANNERS)  
60 RUP STREET, DANVERS, MASSACHUSETTS 01923  
P: 978-777-8550, F: 978-777-8551, WWW.MORINCAMERON.COM

512 WASHINGTON STREET  
HAVERHILL, MASSACHUSETTS



|             |        |
|-------------|--------|
| PROJECT NO. | 14515  |
| DRAWN BY    | ACB    |
| CHECKED BY  | BU     |
| SCALE       | 1"=20' |

APRIL 10, 2026  
REVISED JULY 31, 2026

CERTIFIED  
PLOT PLAN