

N/F
AG PALMDALE REAL
OWNERS, LLC

N/F AG PALMDALE REAL
OWNERS, LLC

PARKING LOT

(8' x 22')
ROLL OFF YARD
CONTAINER DUMPSTER

4 STORY BRICK
121-125 MERRIMACK ST.
PARCEL ID: 106 - 9 - 24
AREA
GIS ACRES: 0.1534
LOT SIZE: 6,680 S.F.

MERRIMACK STREET
(PUBLIC - VARIABLE WIDE)

HOW STREET
(PUBLIC - VARIABLE WIDE)

NOTE:

THE PURPOSE OF THIS PLAN IS TO LAYOUT EXISTING STRUCTURES, PROPOSED ADDITION AND IMPROVEMENT WORKS WITHIN THE PROPERTY BOUNDARIES AS SHOWN IN THE REFERENCE MAPS AND DEED. IT IS NOT INTENDED AS SURVEY TO SET AND/OR UPDATE PROPERTY LINES. CONTRACTOR SHALL PERFORM ALL WORKS IN COMPLIANCE WITH THE COMMONWEALTH OF MASSACHUSETTS LATEST EDITION OF THE BUILDING CODE, THE BUILDING BOARD OF STANDARDS AND REGULATIONS AND THE CITY OF HAVERHILL ORDINANCES. CURB GRANITE PIECES MUST BE RECYCLED BY CITY'S DPW. CONTRACTOR MUST CALL CITY'S DPW FOR RECYCLING ARRANGEMENTS. SIDEWALK MUST BE RESURFACED WITH MATERIAL TO MATCH EXISTING, IF REQUIRED.



REFERENCE DOCS & PLANS

GIS PARCEL INFORMATION
PARCEL ID: 106 - 9 - 24
GIS ACRES: 0.1534

PROPERTY INFORMATION
PROPERTY ID: 106 - 9 - 24
OWNER: DAVINCI MINI APTS / CO
JONY PEREZ
ADDRESS: 125 MERRIMACK ST.
LOT SIZE: 6,680 S.F.
LAND USE CODE: 1110
LEGAL REFERENCE: 11123-454

ZONING: NA
BLDG STYLE: COMM BLOCK
STORIES: 4
YEAR BUILT: 1975
ASSESSOR MAP: HaverhillAssessorMap194

LEGEND

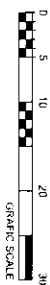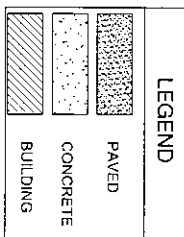

DIMENSIONAL SITE PLAN
SCALE: 1"=10'



**GJ
DESIGN GROUP LLC**
Assoc. AIA
Professional Designer

118 WOODLAND ST LAWRENCE MA 01841
978-691-2644 FAX 978-208-1335
E. MAIL: lach.o7812@gmail.com
NOT TO BE USED BY THE CLIENT FOR ANY WORK OR
PROJECT WITHOUT THE AUTHORIZATION OF THE AUTHOR

PROJECT: COMMERCIAL RESIDENTIAL BUILDING
ADDRESS: 125 MERRIMACK ST. HAVERHILL MA 01830
OWNER: DAVINCI MINI APTS-JONY PEREZ
PETITIONER: DAVINCI MINI APTS-JONY PEREZ

REVISED BY:
APPROVED BY:
DRAWN BY: GILBERTO JIMENEZ
DATE: 9/28/2025

**DIMENSIONAL
SITE PLAN**
SHEET 1 / 1

PROJECT



PROPOSED COMMERCIAL RESIDENTIAL BUILDING

119-125 MERRIMACK STREET, HAVERHILL MA 01830

OWNER: DAVINCI MINI APTS-JONY PEREZ

DRAWN BY: GILBERTO JIMENEZ
GJ DESIGN GROUP LLC

Assoc. AIA
Professional Designer
118 WOODLAND ST LAWRENCE MA 01841
TEL 978-601-2644 E.M. lach 07812@gmail.com Fax: 978-208-1335

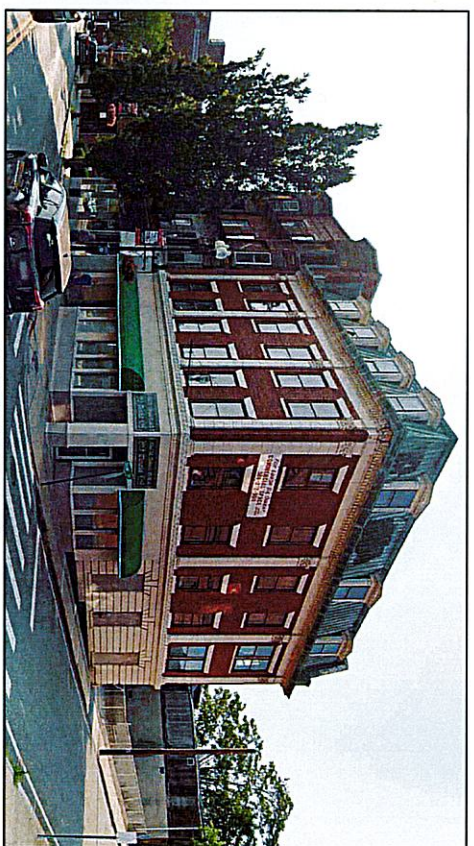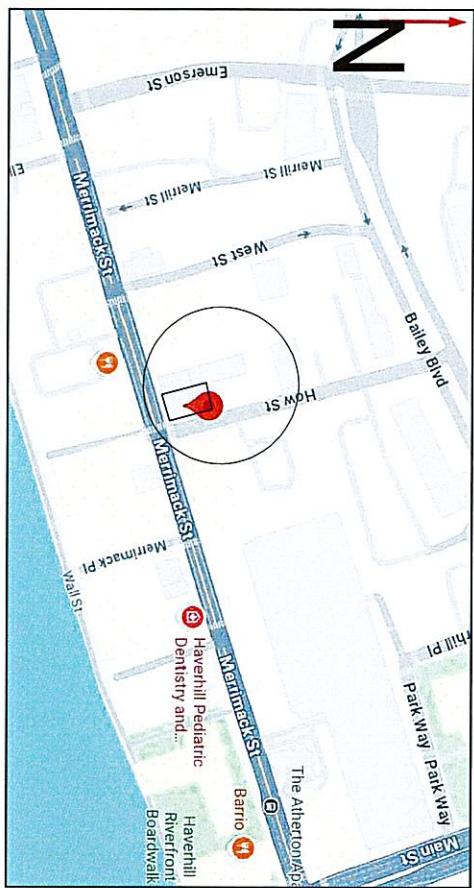

LOCUS MAP

119-125 MERRIMACK ST.

APARTMENTS SCHEDULED:

SECOND FLOOR : 4 APARTMENTS				THIRD FLOOR : 4 APARTMENTS				FOURTH FLOOR : 4 APARTMENTS				OPTION A FOURTH FLOOR : 4 APARTMENTS			
APARTMENT 201	1 BEDROOM	1 BATH	415.00 S.F.	APARTMENT 301	1 BEDROOM	1 BATH	415.00 S.F.	APARTMENT 401	1 BEDROOM	1 BATH	460.00 S.F.	APARTMENT 401	1 BEDROOM	1 BATH	460.00 S.F.
APARTMENT 202	1 BEDROOM	1 BATH	574.00 S.F.	APARTMENT 302	1 BEDROOM	1 BATH	574.00 S.F.	APARTMENT 402	1 BEDROOM	1 BATH	403.00 S.F.	APARTMENT 402	1 BEDROOM	1 BATH	403.00 S.F.
APARTMENT 203	2 BEDROOM	1 BATH	532.00 S.F.	APARTMENT 303	2 BEDROOM	1 BATH	532.00 S.F.	APARTMENT 403	2 BEDROOM	1 BATH	520.00 S.F.	APARTMENT 403	2 BEDROOM	1 BATH	520.00 S.F.
APARTMENT 204	1 BEDROOM	2 BATH	550.00 S.F.	APARTMENT 304	1 BEDROOM	2 BATH	550.00 S.F.	APARTMENT 404	2 BEDROOM	2 BATH	524.00 S.F.	APARTMENT 404	2 BEDROOM	2 BATH	524.00 S.F.
AREA:	2,071.00 S.F.			AREA:	2,071.00 S.F.			AREA:	1,907.00 S.F.			AREA:	1,907.00 S.F.		

GENERAL NOTES:

1. ALL WORK SHALL COMPLY WITH STATE AND LOCAL BUILDING CODES AND REGULATIONS.
2. CONTRACTOR SHALL BE SOLELY RESPONSIBLE FOR ALL DESIGN AND CONSTRUCTION OF THE BUILDING.
3. CONTRACTOR SHALL BE RESPONSIBLE FOR ALL ASPECTS OF THE BUILDING, INCLUDING BUT NOT LIMITED TO: ARCHITECTURAL, STRUCTURAL, MECHANICAL, ELECTRICAL, AND PLUMBING.
4. ALL DIMENSIONS AND SITE CONDITIONS SHALL BE AS SHOWN ON THE DRAWINGS AND SPECIFICATIONS.
5. IT SHALL BE THE RESPONSIBILITY OF THE CONTRACTOR TO OBTAIN ALL NECESSARY PERMITS AND APPROVALS FROM THE CITY OF HAVERHILL.
6. ALL DETAILS, SECTIONS, AND ELEVATIONS SHALL BE IN ACCORDANCE WITH THE CITY OF HAVERHILL ORDINANCES.

SCHEDULED GROSS AREA:

FIRST FLOOR PLAN COMMERCIAL	2,773.00 S.F.
SECOND FLOOR PLAN APARTMENTS	2,859.00 S.F.
THIRD FLOOR PLAN APARTMENTS	2,859.00 S.F.
FOURTH FLOOR PLAN APARTMENTS	2,653.00 S.F.
BASEMENT FLOOR PLAN	2,176.00 S.F.
TOTAL AREA:	13,320.00 S.F.

GENERAL SYMBOLS	
ROOM NAME	DOOR
BREAK LINE	OBJECT ABOVE OR BELOW




GJ DESIGN GROUP LLC
Assoc. AIA
Professional Designer

118 WOODLAND ST LAWRENCE MA 01841
978-601-2644 FAX 978-208-1335
E-MAIL: lach 07812@gmail.com
NOTE: THIS DESIGN IS THE INTELLECTUAL PROPERTY OF GILBERTO JIMENEZ GROUP. THEREFORE IT IS PROHIBITED COPY PARTIALLY OR COMPLETELY THIS DESIGN WITHOUT THE AUTHORIZATION OF THE AUTHOR.

PROJECT: COMMERCIAL RESIDENTIAL BUILDING
ADDRESS: 125 MERRIMACK ST. HAVERHILL MA 01830
OWNER: DAVINCI MINI APTS-JONY PEREZ
PETITIONER: DAVINCI MINI APTS-JONY PEREZ

REVISED BY:
APPROVED BY:
DRAWN BY: GILBERTO JIMENEZ
DATE: 7/28/2025

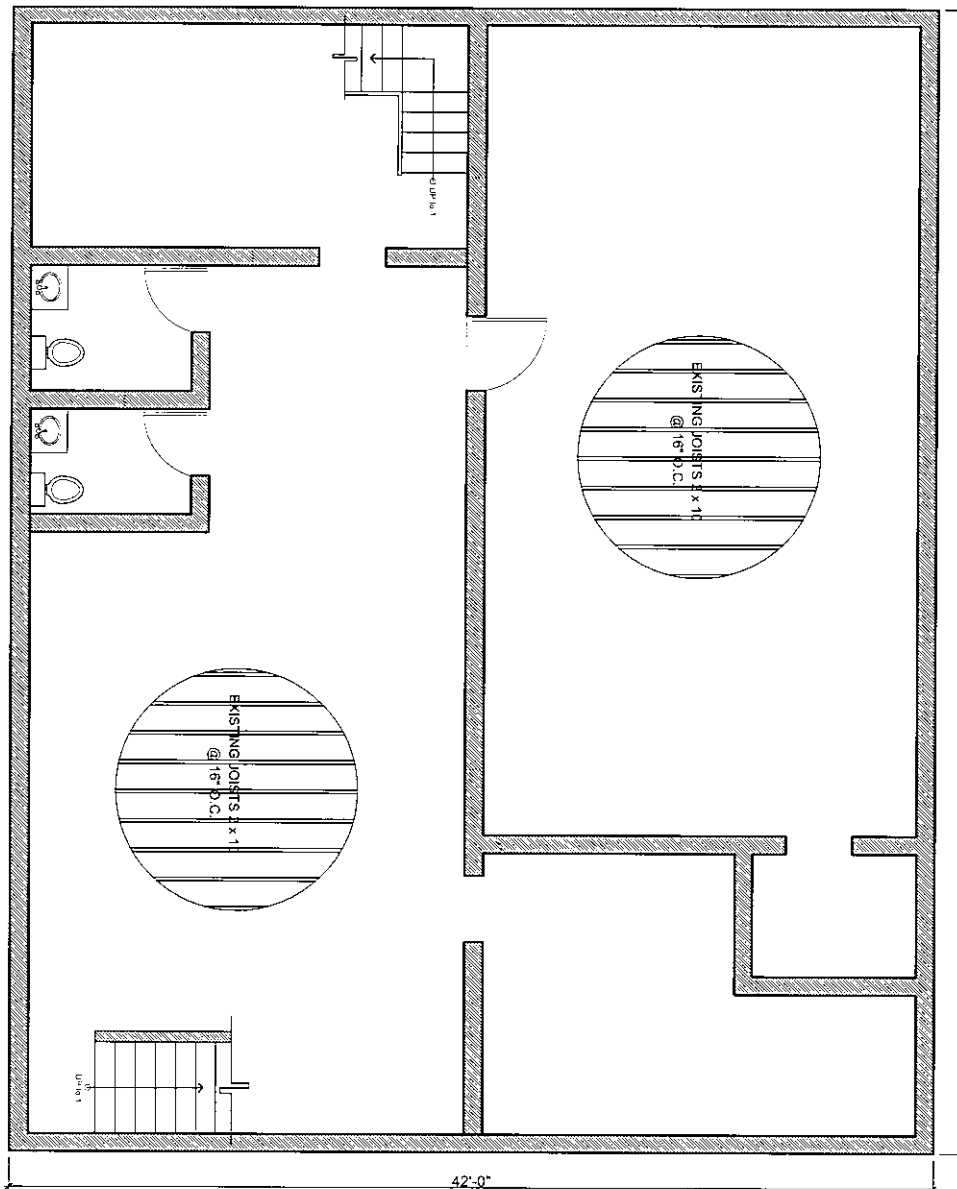

EXISTING BASEMENT FLOOR PLAN

GROSS AREA = 2,180 S.F.

SCALE: 1/4" = 1'-0"



GJ
DESIGN GROUP LLC
 Assoc. AIA
 Professional Designer

118 WOODLAND ST LAWRENCE MA 01841
 978-601-2844 FAX 978-208-1335
 E. MAIL: lach.o7812@gmail.com

NOTE: THIS DESIGN IS THE INTELLECTUAL PROPERTY OF
 GILBERTO JIMENEZ GROUP. THEREFORE, THIS
 PROJECT CANNOT BE REPRODUCED OR COPIED IN ANY
 FORM OR BY ANY MEANS WITHOUT THE AUTHORIZATION OF THE AUTHOR.


PROJECT: COMMERCIAL RESIDENTIAL BUILDING
 ADDRESS: 125 MERRIMACK ST. HAVERHILL MA 01830
 OWNER: DAVINCI MINI APTS-JONY PEREZ
 PETITIONER: DAVINCI MINI APTS-JONY PEREZ

REVISED BY:
 APPROVED BY:
 DRAWN BY: GILBERTO JIMENEZ
 DATE: 7/28/2025

FLOOR PLAN
 SHEET 1 2 41

EXISTING FIRST FLOOR PLAN

SCALE 1/4" = 1'-0"
GROSS AREA = 2,180 S.F.

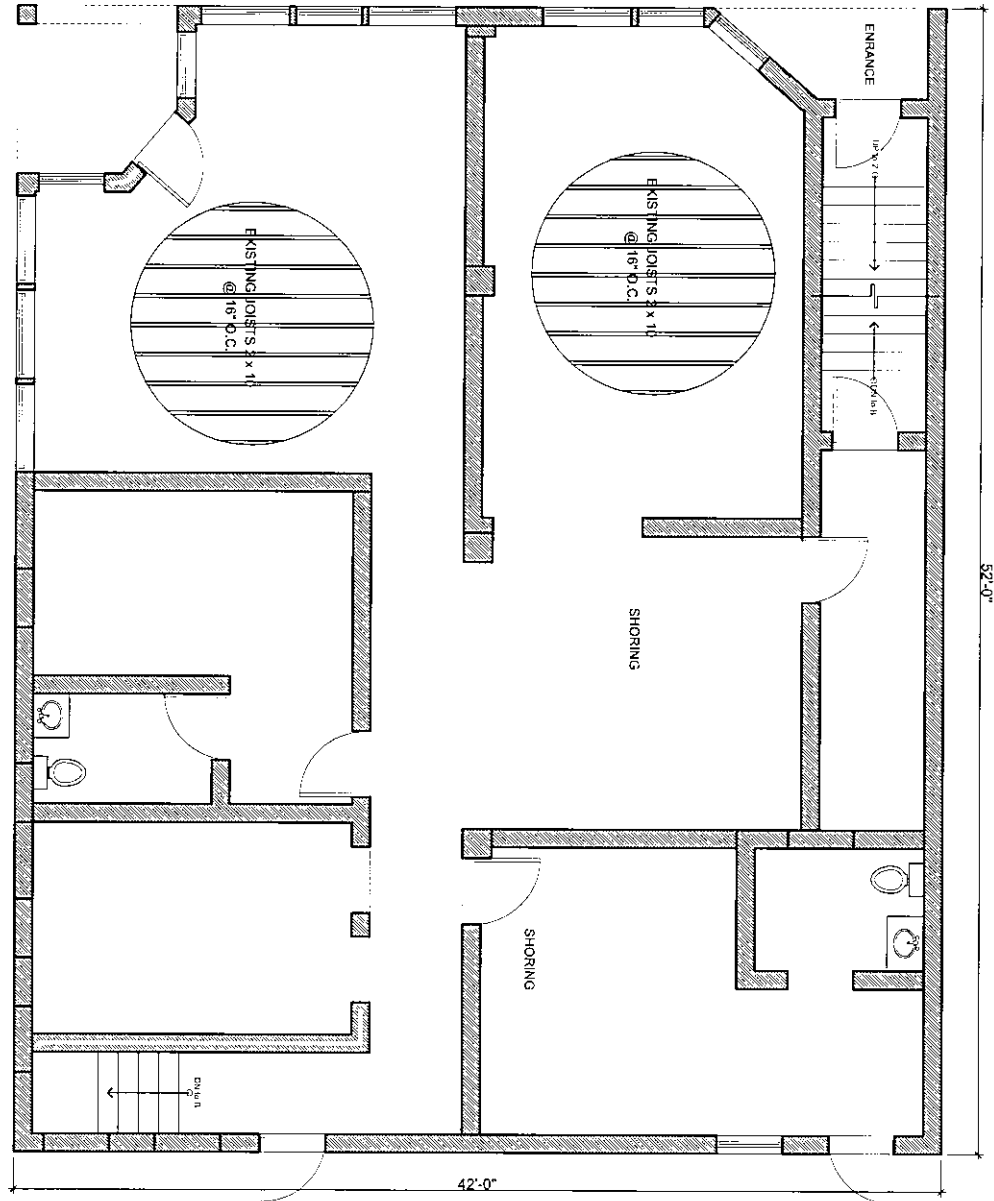

GJ
DESIGN GROUP LLC
Assoc. AIA
Professional Designer

118 WOODLAND ST LAWRENCE MA 01841
978-601-2844 FAX 978-208-1335
E. MAIL lach.o7612@gmail.com
NOTE: THIS DESIGN IS THE INTELLECTUAL PROPERTY OF
GILBERTO JIMENEZ GROUP. IT IS NOT TO BE
REPRODUCED, COPIED, PARTIALLY OR COMPLETELY THIS
DESIGN WITHOUT THE AUTHORIZATION OF THE AUTHOR


PROJECT: COMMERCIAL RESIDENTIAL BUILDING
ADDRESS: 125 MERRIMACK ST. HAVERHILL MA 01830
OWNER: DAVINCI MINI APTS-JONY PEREZ
PETITIONER: DAVINCI MINI APTS-JONY PEREZ

REVISED BY:
APPROVED BY:
DRAWN BY: GILBERTO JIMENEZ
DATE: 7/28/2025

FLOOR PLAN
SHEET 1 3 41

EXISTING SECOND FLOOR PLAN

GROSS AREA= 2,180 S.F.

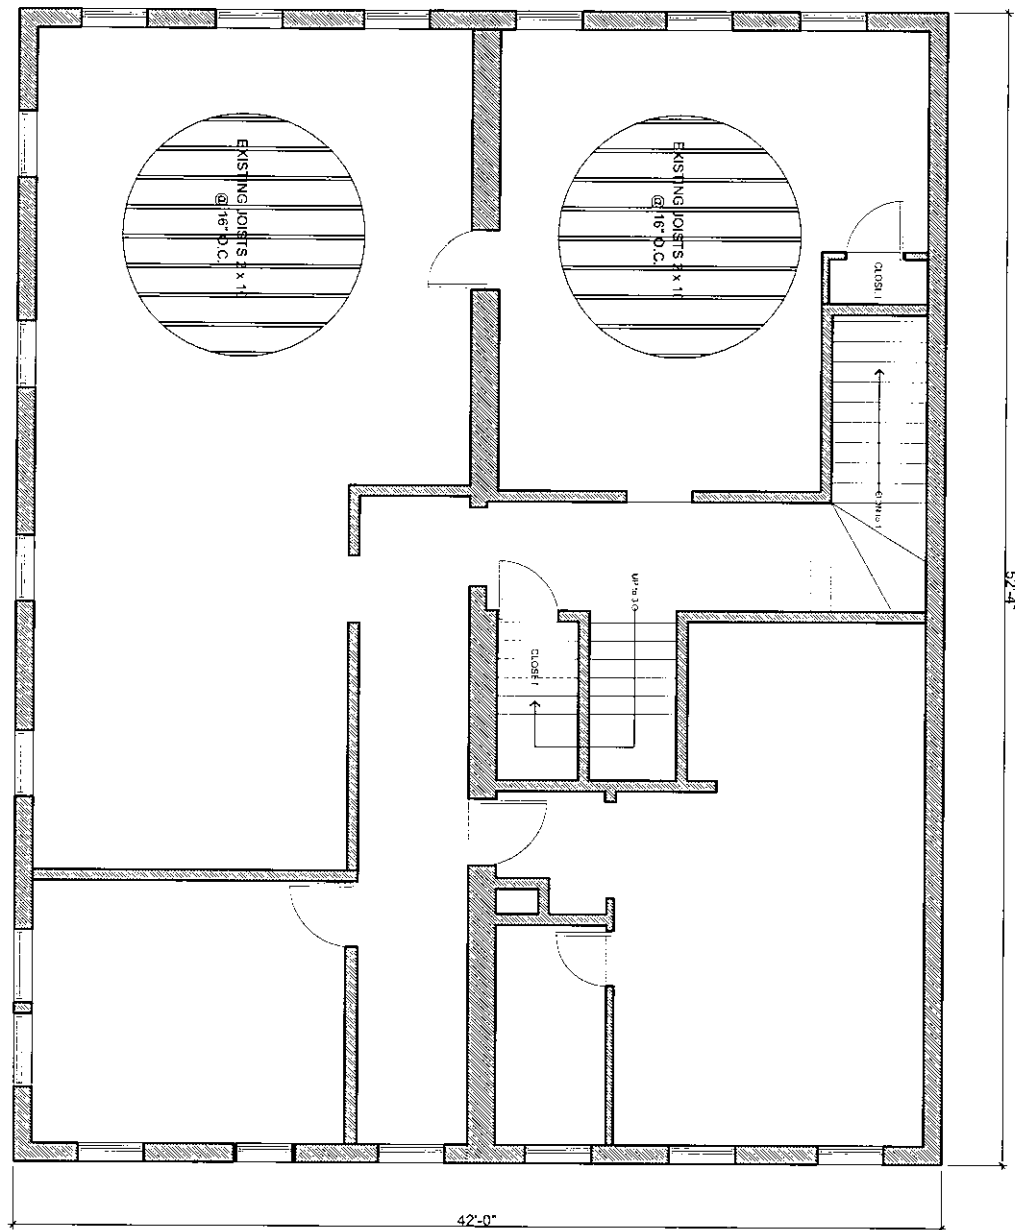

GJ
DESIGN GROUP LLC
 Assoc. AIA
 Professional Designer

118 WOODLAND ST LAWRENCE MA 01841
 978-601-2844 FAX 978-208-1335
 E. MAIL lach.o7812@gmail.com



NOTE: THIS DESIGN IS THE INTELLECTUAL PROPERTY OF
 GILBERTO JIMENEZ GROUP. NO REUSE, REPRODUCTION,
 PHOTOCOPYING, OR ANY OTHER FORM OF REPRODUCTION OF THIS
 DESIGN WITHOUT THE AUTHORIZATION OF THE AUTHOR.

PROJECT: COMMERCIAL RESIDENTIAL BUILDING
 ADDRESS: 125 MERRIMACK ST. HAVERHILL MA 01830
 OWNER: DAVINCI MINI APTS-JONY PEREZ
 PETITIONER: DAVINCI MINI APTS-JONY PEREZ

REVISED BY:
 APPROVED BY:
 DRAWN BY: GILBERTO JIMENEZ
 DATE: 7/28/2025

FLOOR PLAN

SHEET
 1
 4
 41

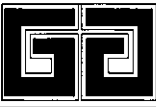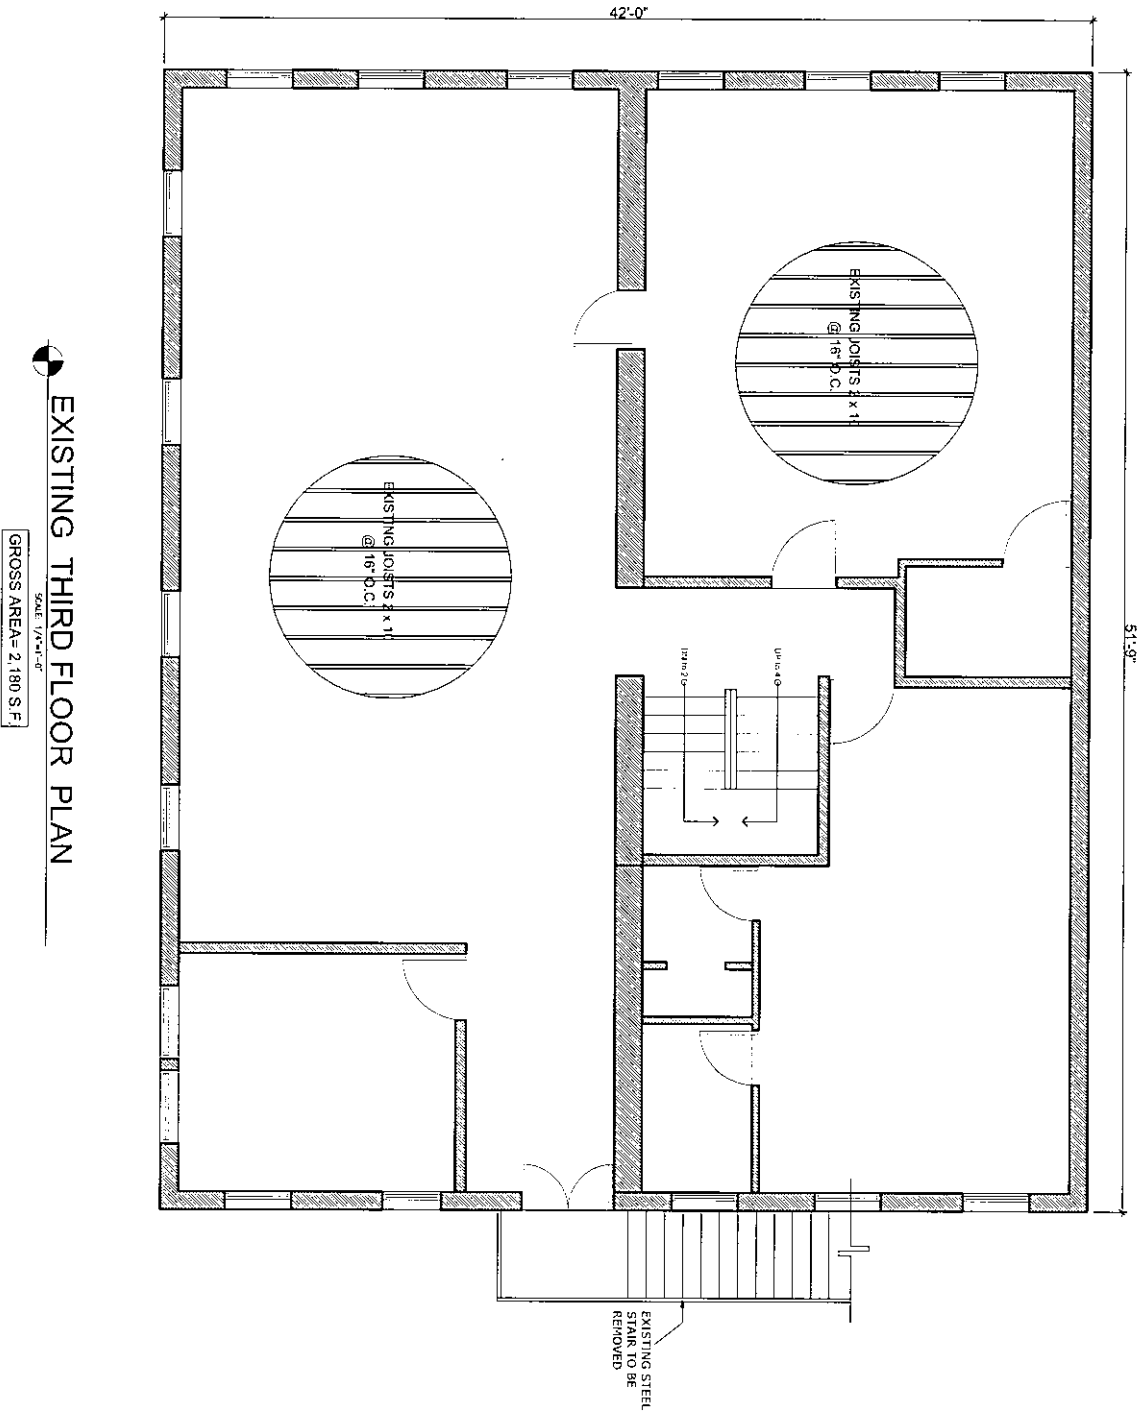

GJ
DESIGN GROUP LLC
 Assoc. AIA
 Professional Designer

118 WOODLAND ST LAWRENCE, MA 01841
 978-601-2844 FAX 978-208-1335
 E. MAIL: lach@7612@gmail.com
 NOTE: THIS DESIGN IS THE EXCLUSIVE PROPERTY OF
 GILBERTO JIMENEZ GROUP. NO REUSE, REPRODUCTION,
 PROMOTION, COPY PARTIALY OR COMPLETELY THIS
 DESIGN WITHOUT THE AUTHORIZATION OF THE AUTHOR



PROJECT: COMMERCIAL RESIDENTIAL BUILDING
 ADDRESS: 125 MERRIMACK ST, HAVERHILL, MA 01830
 OWNER: DAVINCI MINI APTS-JONY PEREZ
 PETITIONER: DAVINCI MINI APTS-JONY PEREZ

REVISED BY:
 APPROVED BY:
 DRAWN BY: GILBERTO JIMENEZ
 DATE: 7/28/2025

FLOOR PLAN
 SHEET 1
 5
 41

EXISTING FOURTH FLOOR PLAN

GROSS AREA = 2,000 S.F.

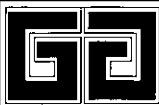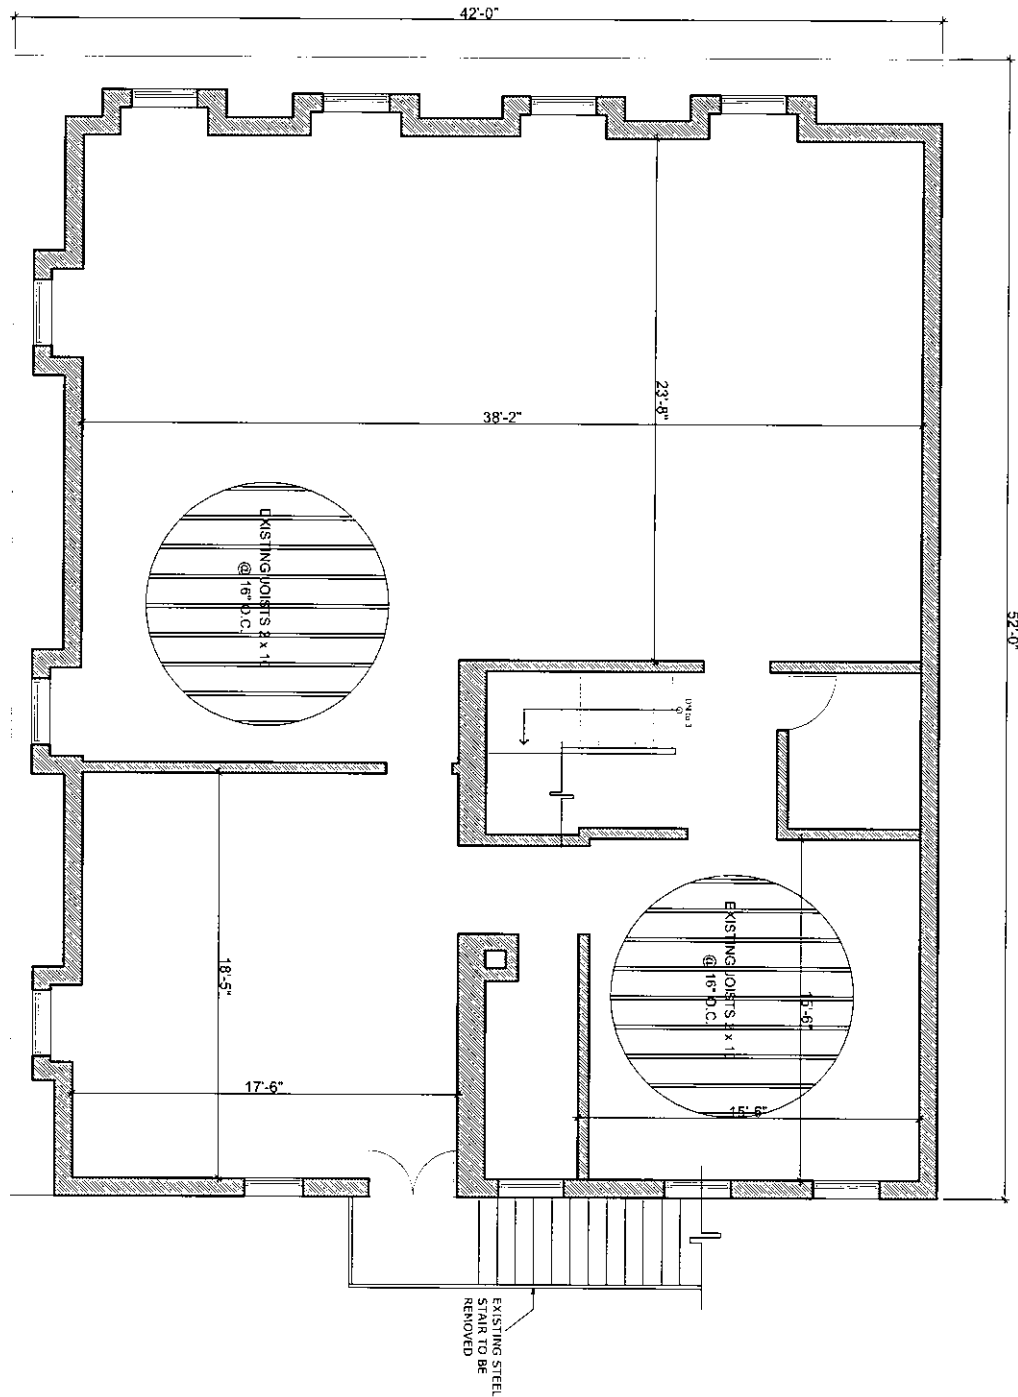

GJ
DESIGN GROUP LLC
 Assoc. AIA
 Professional Designer

118 WOODLAND ST LAWRENCE MA 01841
 978-601-2844 FAX 978-208-1335
 E. MAIL: lach.o7812@gmail.com
 NOTE: THIS DESIGN IS THE "LECTICA" PROPERTY OF
 GILBERTO JIMENEZ GROUP. THEREFORE, IT IS
 PROHIBITED COPY, REPRODUCE OR OTHERWISE
 DESIGN WITHOUT THE AUTHORIZATION OF THE AUTHOR


PROJECT: COMMERCIAL RESIDENTIAL BUILDING
 ADDRESS: 125 MERRIMACK ST. HAVERHILL MA 01830
 OWNER: DAVINCI MINI APTS-JONY PEREZ
 PETITIONER: DAVINCI MINI APTS-JONY PEREZ

REVISED BY:
 APPROVED BY:
 DRAWN BY: GILBERTO JIMENEZ
 DATE: 7/28/2025

FLOOR PLAN
 SHEET 1
 6
 41

EXISTING RIGHT SIDE ELEVATION

SCALE: 1/4"=1'-0"

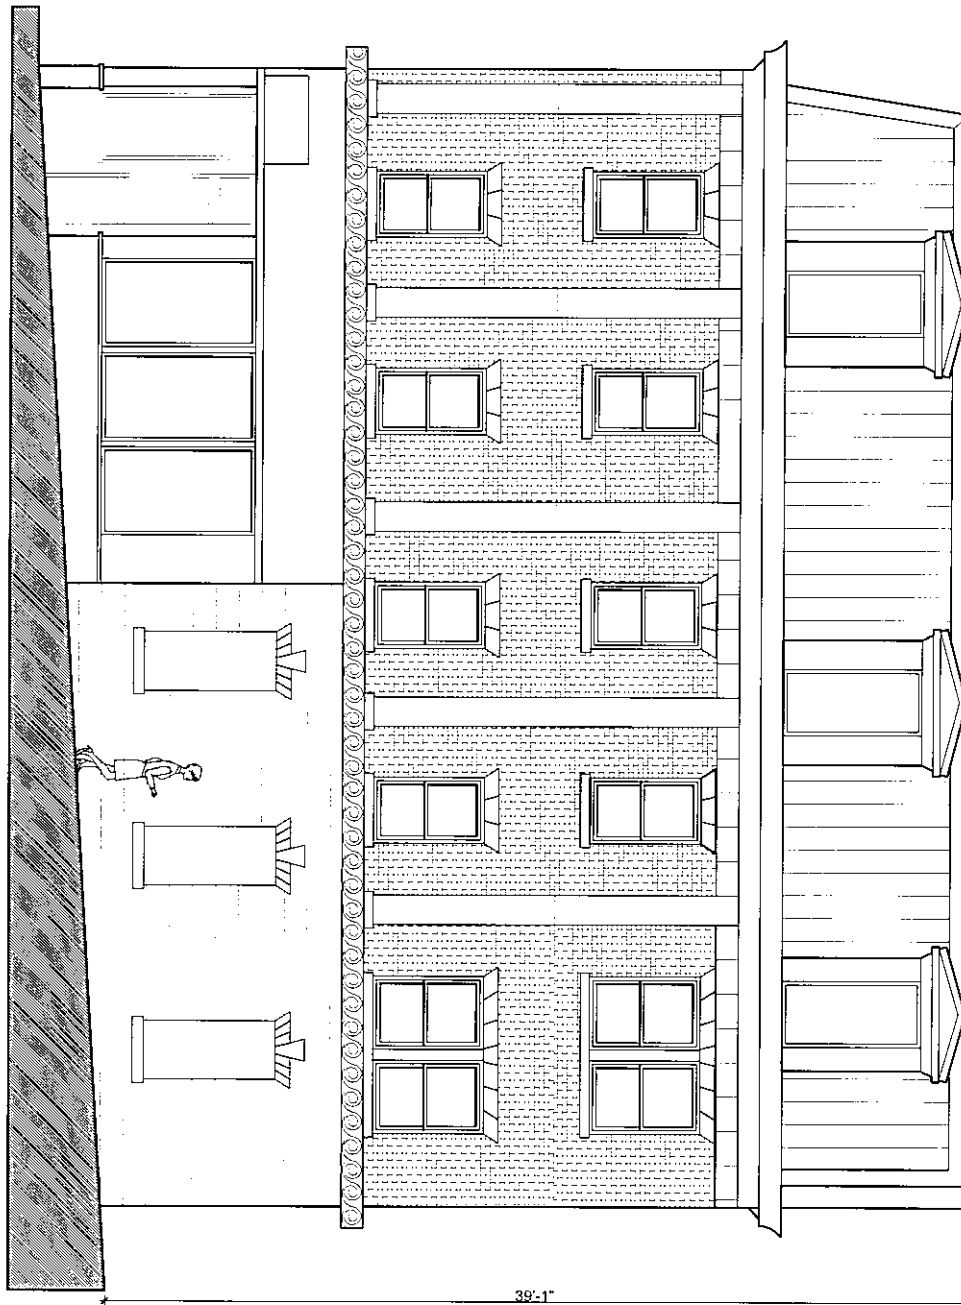

39'-1"



GJ
DESIGN GROUP LLC
 Assoc. AIA
 Professional Designer


118 WOODLAND ST LAWRENCE MA 01841
 978-661-2844 FAX 978-208-1335
 E. MAIL lach.o7812@gmail.com
 NOTE: THIS DESIGN IS THE PROPERTY OF
 GILBERTO JIMENEZ GROUP. ANY REUSE OR
 PROHIBITED. COPY PARTIALLY OR COMPLETELY THIS
 DESIGN WITHOUT THE AUTHORIZATION OF THE AUTHOR

PROJECT: COMMERCIAL RESIDENTIAL BUILDING
 ADDRESS: 125 MERRIMACK ST. HAVERHILL MA 01830
 OWNER: DAVINCI MINI APTS-JONY PEREZ
 PETITIONER: DAVINCI MINI APTS-JONY PEREZ

REVISED BY:
 APPROVED BY:
 DRAWN BY: GILBERTO JIMENEZ
 DATE: 7/28/2025

ELEVATION
 SHEET 1 7 41

EXISTING REAR ELEVATION
SCALE 1/4"=1'-0"

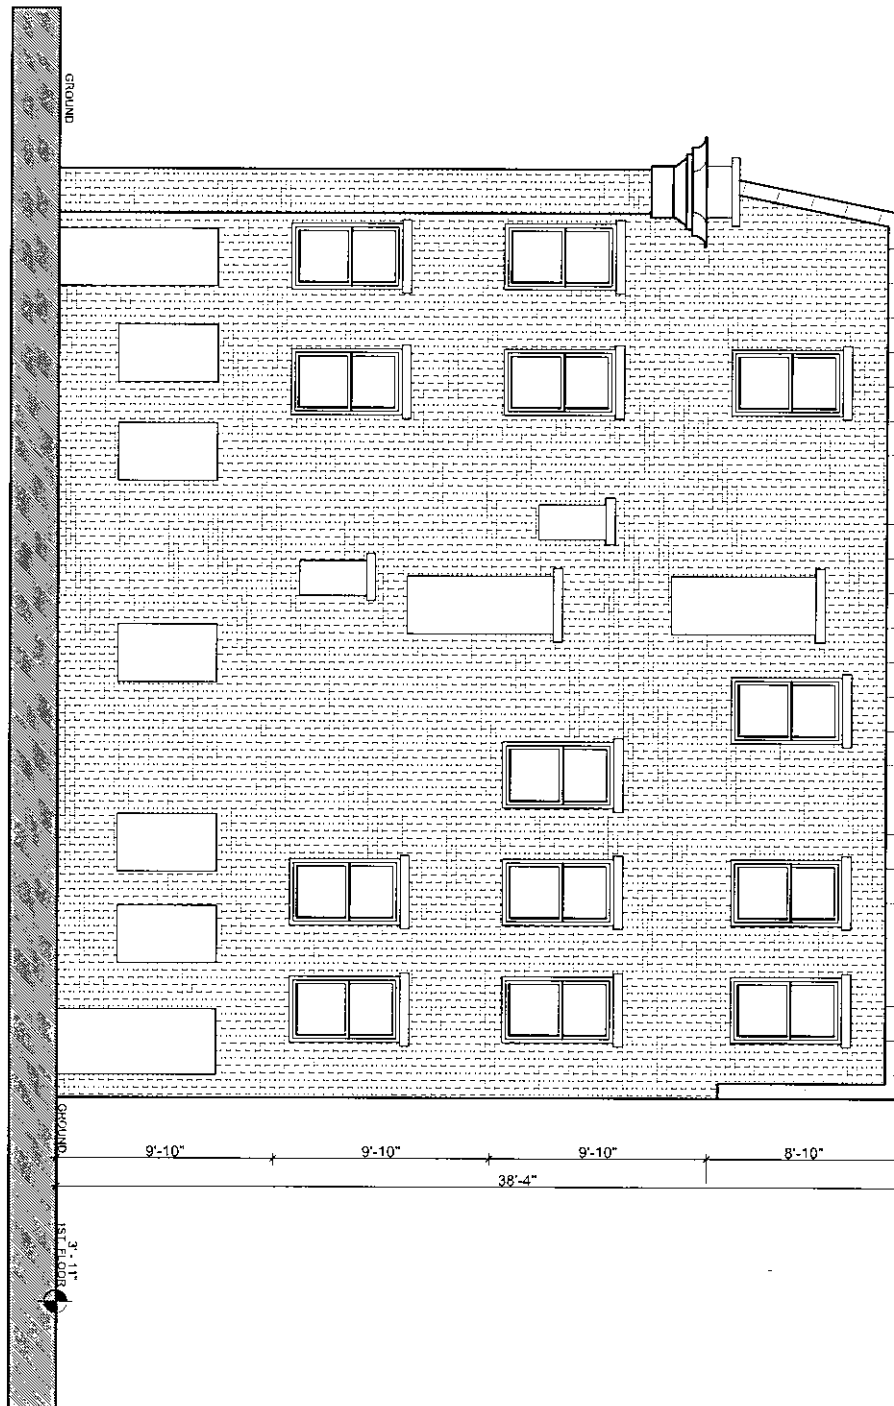

GJ
DESIGN GROUP LLC
Assoc. AIA
Professional Designer


118 WOODLAND ST LAWRENCE MA 01841
978-601-2844 FAX 978-208-1335
E. MAIL: lach.o7812@gmail.com
NOT TO BE REPRODUCED OR TRANSMITTED IN ANY FORM OR BY ANY MEANS, ELECTRONIC OR MECHANICAL, INCLUDING PHOTOCOPYING, RECORDING, OR BY ANY INFORMATION STORAGE AND RETRIEVAL SYSTEM, WITHOUT THE WRITTEN PERMISSION OF THE DESIGNER.

PROJECT: COMMERCIAL RESIDENTIAL BUILDING
ADDRESS: 125 MERRIMACK ST. HAVERHILL MA 01830
OWNER: DAVINCI MINI APTS-JONY PEREZ
PETITIONER: DAVINCI MINI APTS-JONY PEREZ


REVISED BY:
APPROVED BY:
DRAWN BY: GILBERTO JIMENEZ
DATE: 7/28/2025

ELEVATION
SHEET 1
8
41

LEGEND	
	EXISTING WALL TO REMAIN
	PROPOSED NEW WALL
	DEMOL. WALL

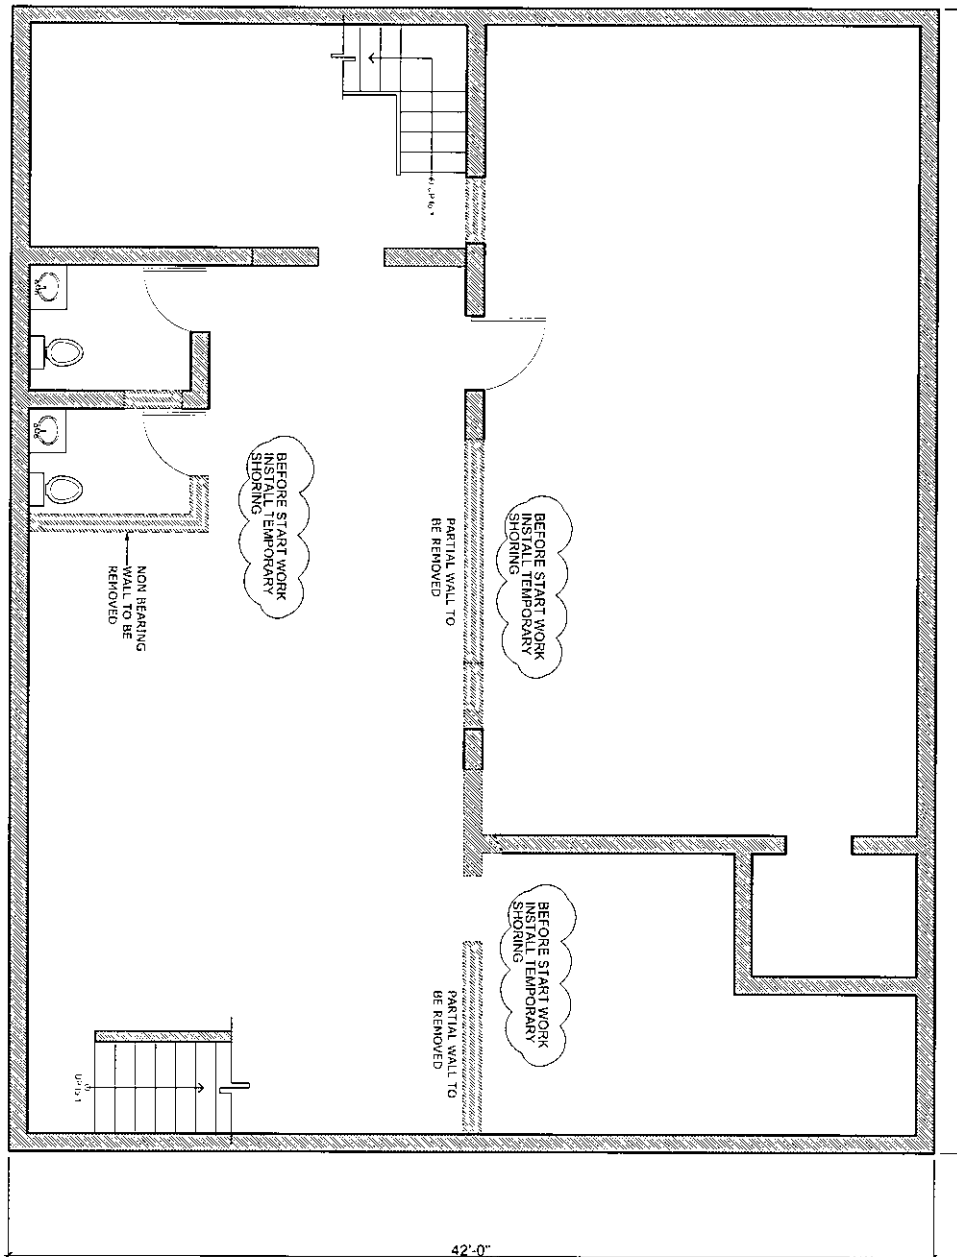

BASEMENT
DEMO PLAN
SCALE 1/4"=1'-0"

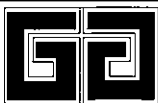

GJ
DESIGN GROUP LLC
Assoc. AIA
Professional Designer


118 WOODLAND ST LAWRENCE MA 01841
978-601-2844 FAX 978-208-1335
E. MAIL lach.o7812@gmail.com

NOTE: THIS DESIGN IS THE INTELLECTUAL PROPERTY OF
GILBERTO JIMENEZ GROUP. NO PART OF THIS
DESIGN MAY BE REPRODUCED OR TRANSMITTED IN ANY
FORM OR BY ANY MEANS, ELECTRONIC OR MECHANICAL,
INCLUDING PHOTOCOPYING, RECORDING, OR BY ANY
INFORMATION STORAGE AND RETRIEVAL SYSTEM,
WITHOUT THE WRITTEN PERMISSION OF THE DESIGNER.

PROJECT: COMMERCIAL RESIDENTIAL BUILDING
ADDRESS: 125 MERRIMACK ST. HAVERHILL MA 01830
OWNER: DAVINCI MINI APTS-JONY PEREZ
PETITIONER: DAVINCI MINI APTS-JONY PEREZ


REVISED BY:
APPROVED BY:
DRAWN BY: GILBERTO JIMENEZ
DATE: 7/28/2025

FLOOR PLAN
SHEET 1 9 41

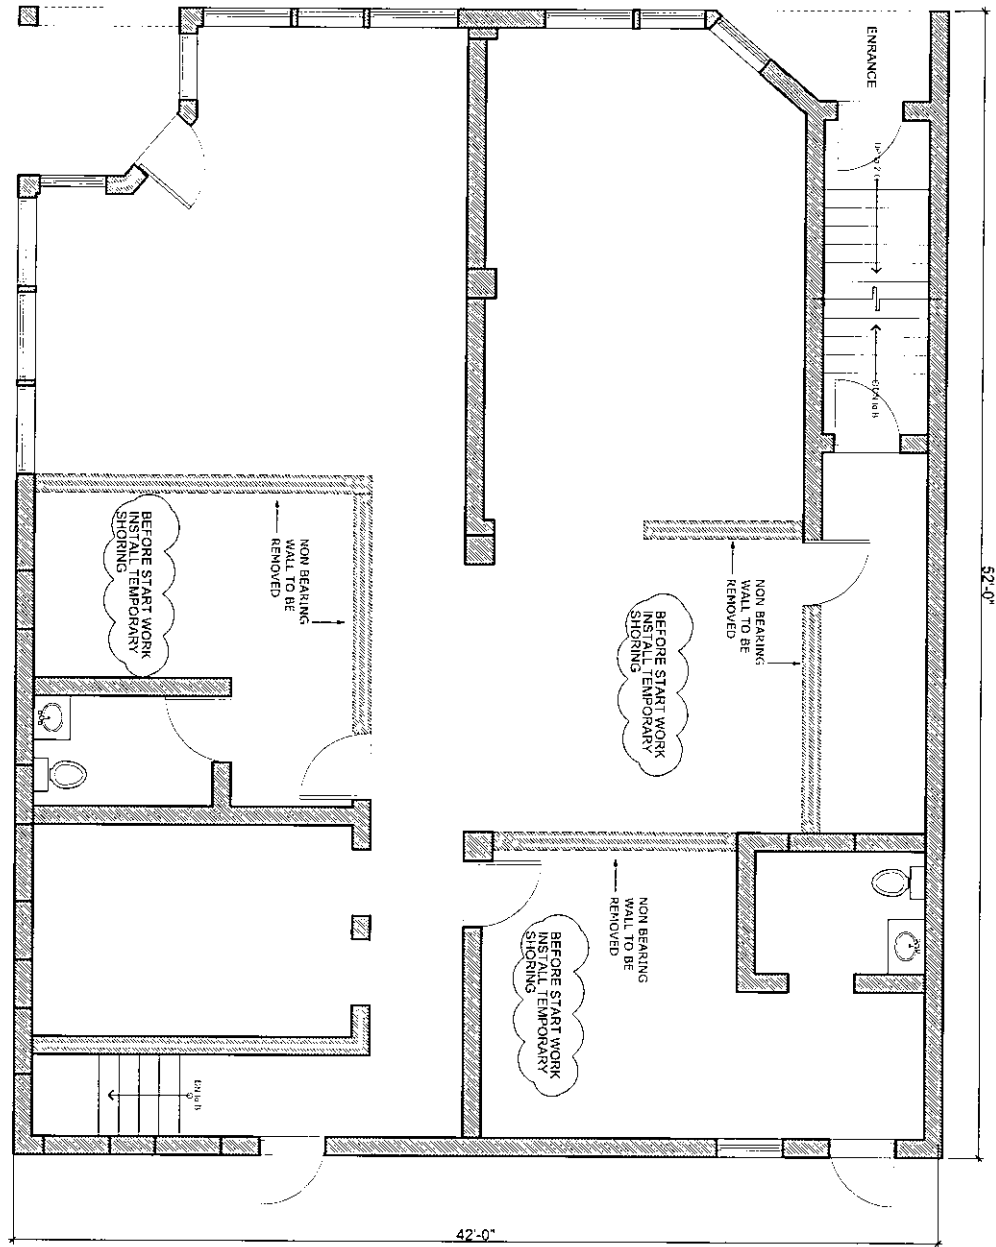

FIRST FLOOR
DEMO PLAN
SCALE: 1/8"=1'-0"

SECOND FLOOR
DEMO PLAN
SCALE: 1/4"=1'-0"

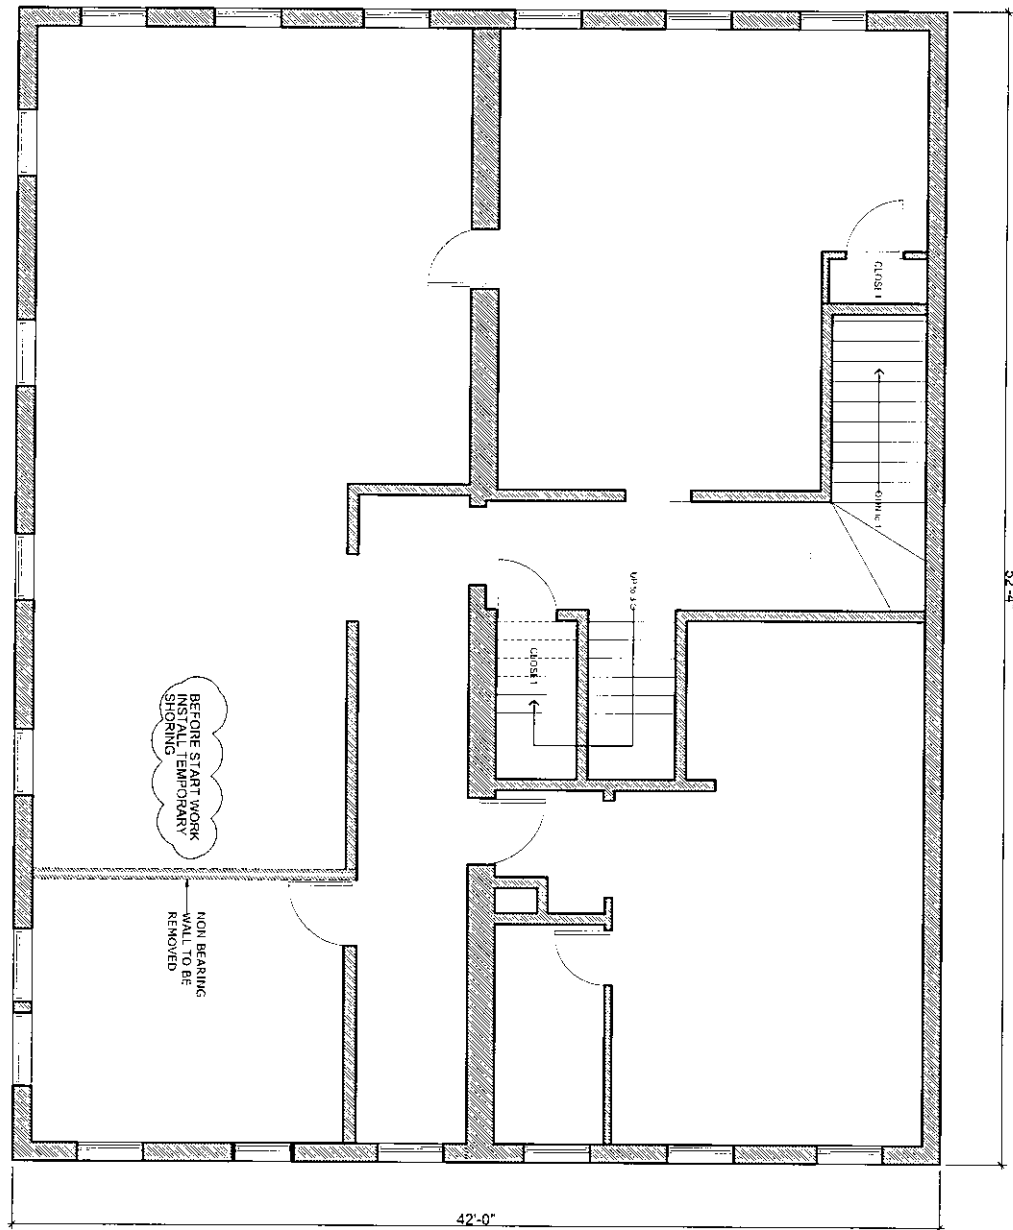

GJ
DESIGN GROUP LLC
Assoc. AIA
Professional Designer


118 WOODLAND ST. LAWRENCE MA 01841
978-601-2844 FAX 978-208-1335
E. MAIL: lach.o7812@gmail.com
NOTE: THIS DESIGN IS THE INTELLECTUAL PROPERTY OF
GILBERTO JIMENEZ GROUP. THEREFORE, IT IS
PROHIBITED TO REPRODUCE OR COMPLETE THIS
DESIGN WITHOUT THE AUTHORIZATION OF THE AUTHOR.

PROJECT: COMMERCIAL RESIDENTIAL BUILDING
ADDRESS: 125 MERRIMACK ST. HAVERHILL MA 01830
OWNER: DAVINCI MINI APTS-JONY PEREZ
PETITIONER: DAVINCI MINI APTS-JONY PEREZ

REVISED BY:
APPROVED BY:
DRAWN BY: GILBERTO JIMENEZ
DATE: 7/28/2025

FLOOR PLAN
SHEETS
11
41

THIRD FLOOR
DEMO PLAN
SCALE 1/4"=1'-0"

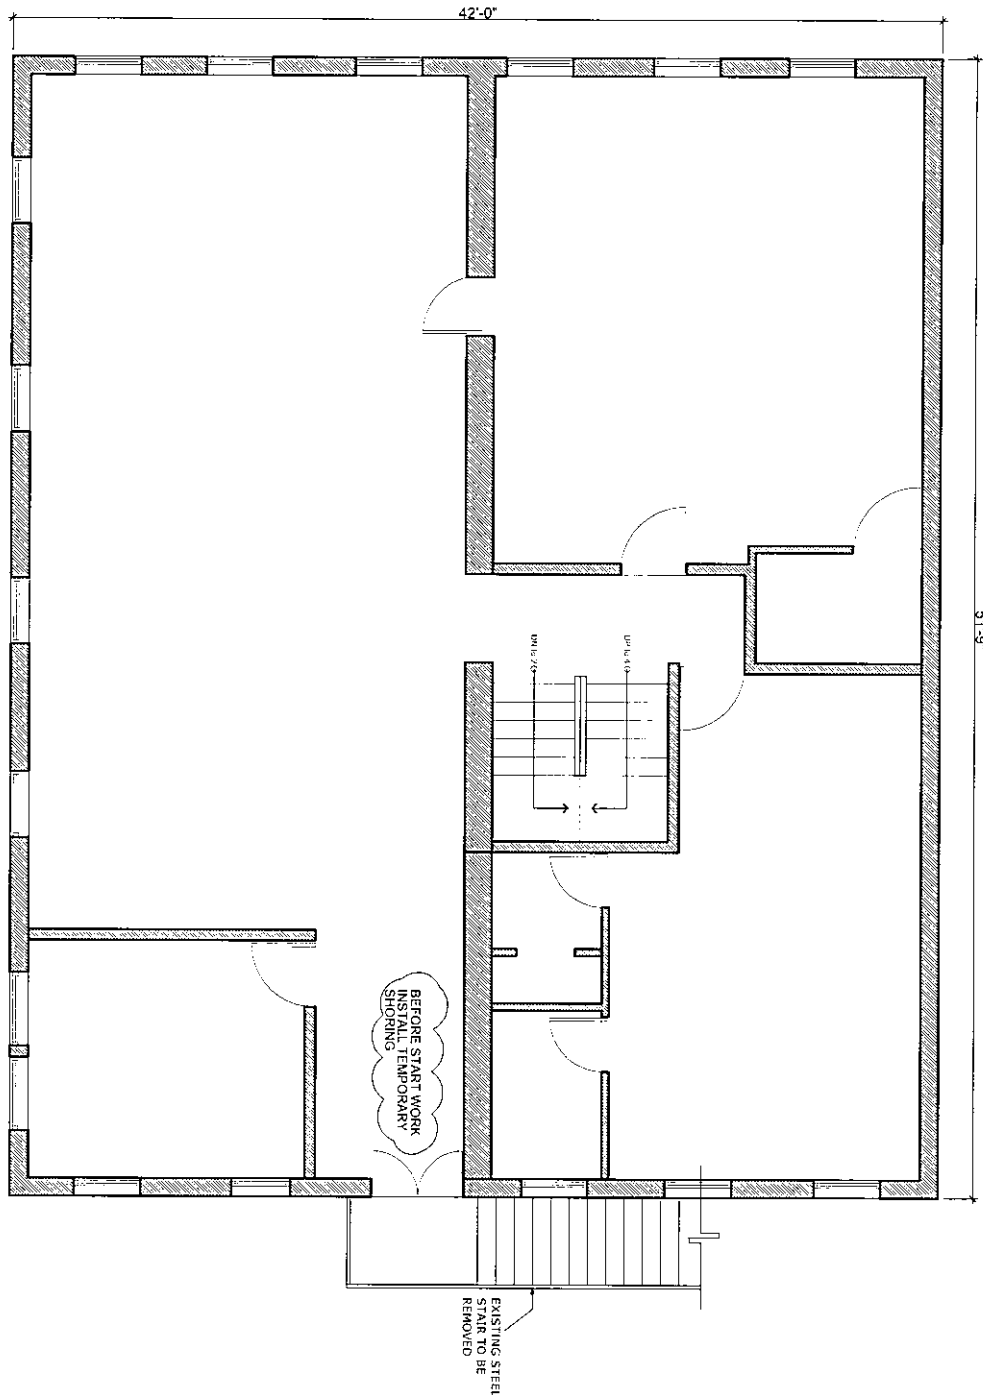

GJ
DESIGN GROUP LLC
Assoc. AIA
Professional Designer


118 WOODLAND ST LAWRENCE MA 01841
978-601-2844 FAX 978-208-1335
E. MAIL: lach.o7812@gmail.com
NOT TO BE USED IN THE FUTURE, PROPERTY OF
GILBERTO JIMENEZ GROUP. THEREFORE IT IS
PROHIBITED COPY PARTIALLY OR COMPLETELY THIS
DESIGN WITHOUT THE AUTHORIZATION OF THE AUTHOR

PROJECT: COMMERCIAL RESIDENTIAL BUILDING
ADDRESS: 125 MERRIMACK ST. HAVERHILL MA 01830
OWNER: DAVINCI MINI APTS-JONY PEREZ
PETITIONER: DAVINCI MINI APTS-JONY PEREZ

REVISED BY:
APPROVED BY:
DRAWN BY: GILBERTO JIMENEZ
DATE: 7/28/2025

FLOOR PLAN
SHEET 1
12
41

FOURTH FLOOR
DEMO PLAN
SCALE: 1/8" = 1'-0"

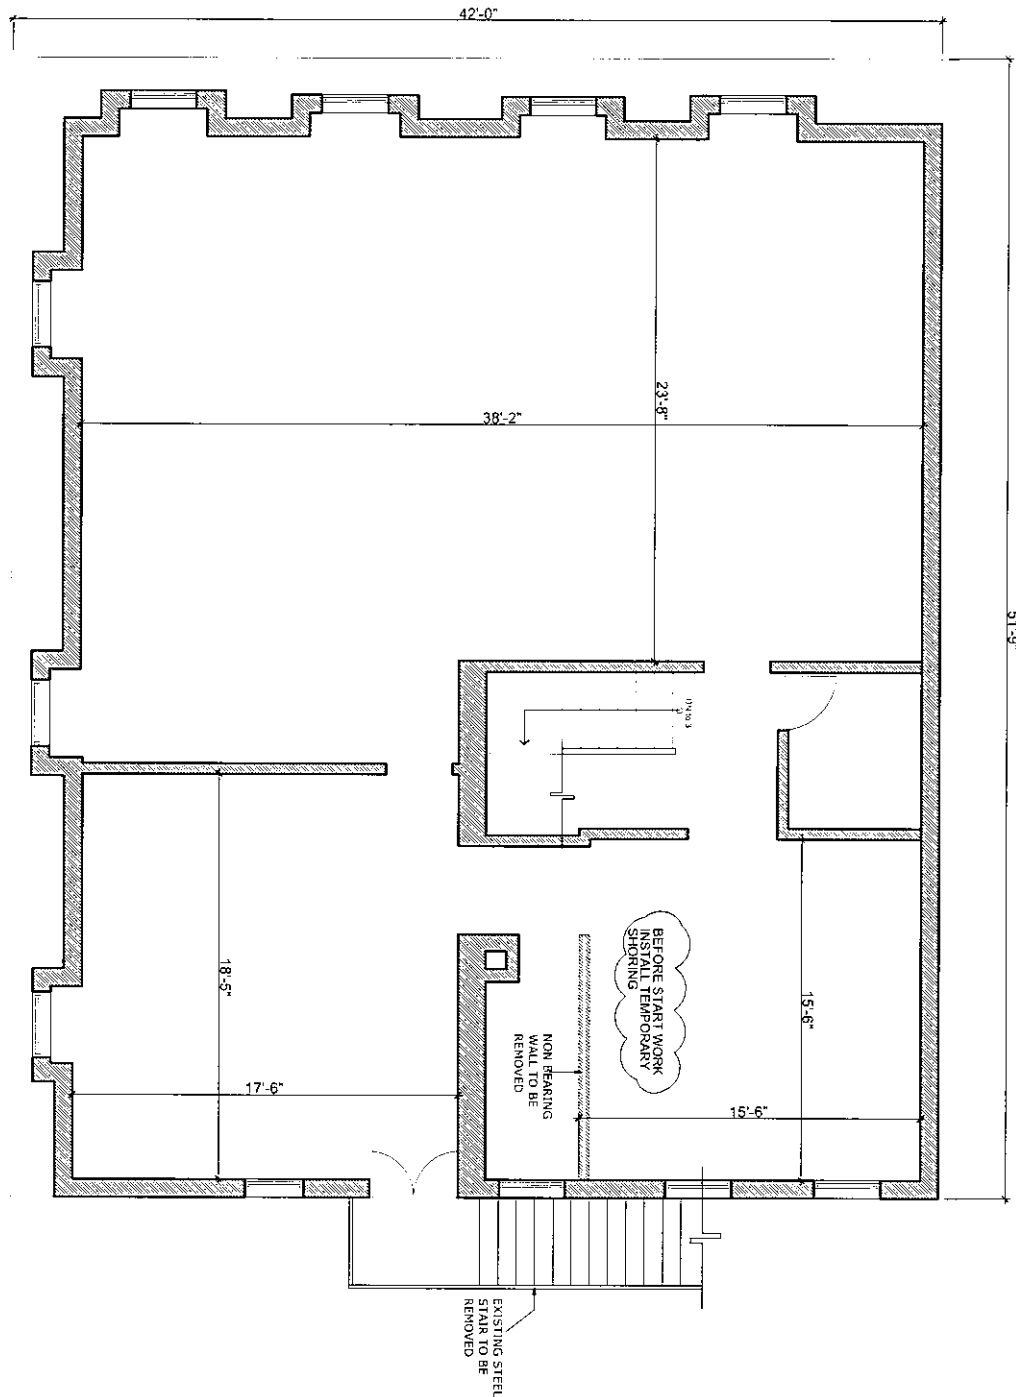


GJ
DESIGN GROUP LLC
Assoc. AIA
Professional Designer

118 WOODLAND ST LAWRENCE MA 01841
978-601-2644 FAX 978-208-1335
E. MAIL lach.07812@gmail.com
NOTE: THIS DESIGN IS THE INTELLECTUAL PROPERTY OF
GILBERTO JIMENEZ GROUP. THEREFORE, IT IS
PROHIBITED TO COPY PARTIALLY OR COMPLETELY THIS
DESIGN WITHOUT THE AUTHORIZATION OF THE AUTHOR

PROJECT: COMMERCIAL RESIDENTIAL BUILDING
ADDRESS: 125 MERRIMACK ST. HAVERHILL MA 01830
OWNER: DAVINCI MINI APTS-JONY PEREZ
PETITIONER: DAVINCI MINI APTS-JONY PEREZ


REVISED BY:
APPROVED BY:
DRAWN BY: GILBERTO JIMENEZ
DATE: 7/28/2025

FLOOR PLAN
SHEET 1
13
41

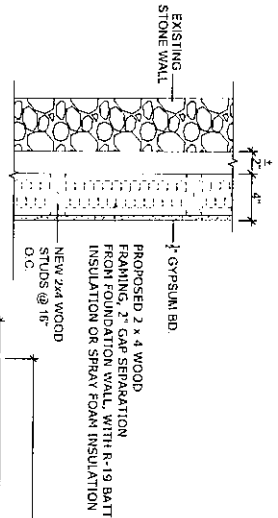

NOTE:
CONTRACTOR SHALL PERFORM ALL WORKS IN COMPLIANCE WITH THE COMMONWEALTH OF MASSACHUSETTS (10TH EDITION OF THE MISC.780 CMR) (2021 IBC AND THE COMMONWEALTH OF MASSACHUSETTS AMENDMENT TO THE INTERNATIONAL COMMERCIAL CODE 2021) AND THE CITY OF HAVERHILL ORDINANCES.

DETAIL -L- EXTERIOR WALL

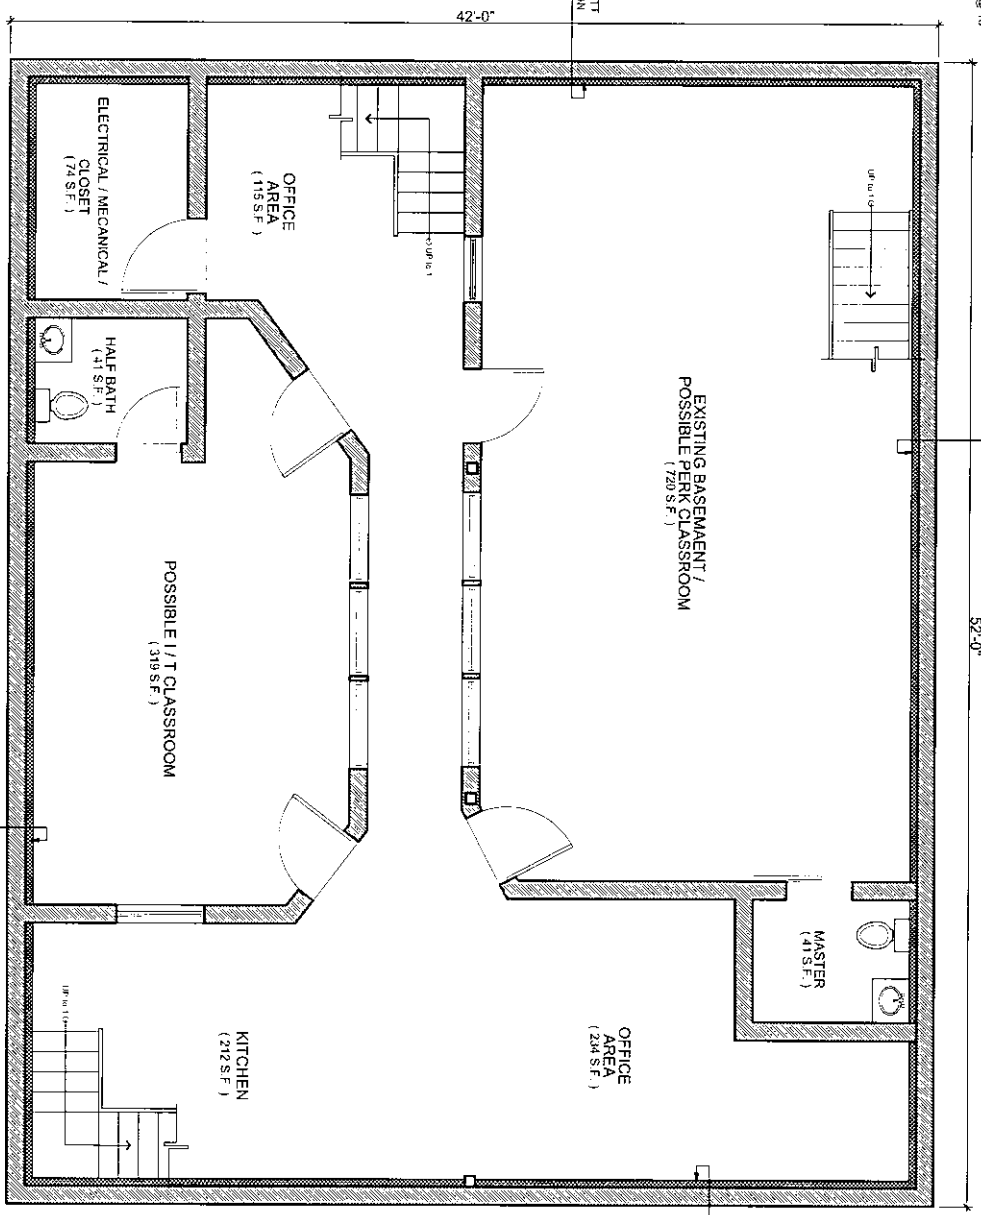

PROPOSED 2 x 4 WOOD FRAMING, 2" GAP SEPARATION FROM FOUNDATION WALL, WITH R-19 BATT INSULATION OR SPRAY FOAM INSULATION
SEE DETAIL -L-

SEE DETAIL -L-

PROPOSED 2 x 4 WOOD FRAMING, 2" GAP SEPARATION FROM FOUNDATION WALL, WITH R-19 BATT INSULATION OR SPRAY FOAM INSULATION
SEE DETAIL -L-

PROPOSED 2 x 4 WOOD FRAMING, 2" GAP SEPARATION FROM FOUNDATION WALL, WITH R-19 BATT INSULATION OR SPRAY FOAM INSULATION
SEE DETAIL -L-

PROPOSED BASEMENT FLOOR PLAN

INTERIOR AREA = 2,027 S.F.




GJ DESIGN GROUP LLC
Assoc. AIA
Professional Designer

118 WOODLAND ST LAWRENCE MA 01841
978-601-2844 FAX 978-208-1335
E. MAIL lach.07812@gmail.com
NOTE: THIS DESIGN IS THE INTELLECTUAL PROPERTY OF GILBERTO JIMENEZ GROUP. THEREFORE, NO PROHIBITED, COMPARABLE OR COMPLETELY THIS DESIGN WITHOUT THE AUTHORIZATION OF THE AUTHOR

PROJECT: COMMERCIAL RESIDENTIAL BUILDING
ADDRESS: 125 MERRIMACK ST. HAVERHILL MA 01830
OWNER: DAVINCI MINI APTS-JONY PEREZ
PETITIONER: DAVINCI MINI APTS-JONY PEREZ

REVISED BY:
APPROVED BY:
DATE: 7/28/2025

FLOOR PLAN
SHEET 14 OF 41

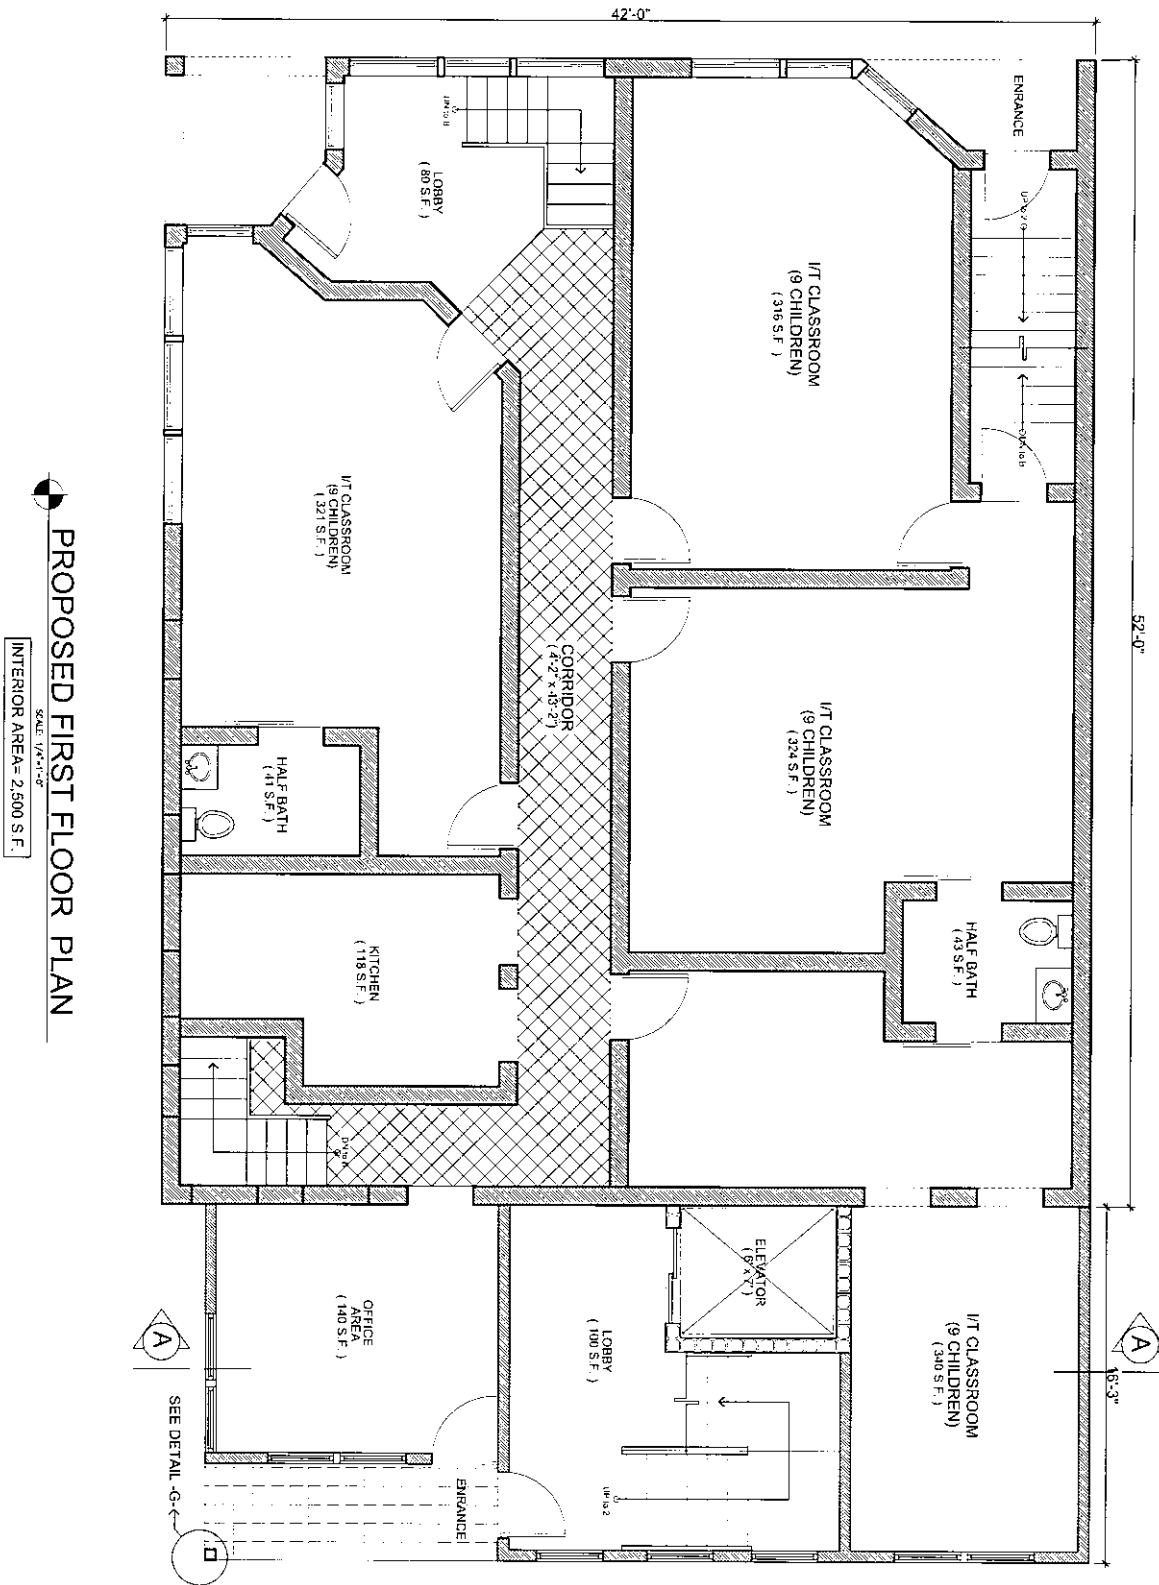

PROPOSED FIRST FLOOR PLAN

SCALE: 1/4" = 1'-0"
INTERIOR AREA= 2,500 S.F.




GJ
DESIGN GROUP LLC
Assoc. AIA
Professional Designer

118 WOODLAND ST LAWRENCE MA 01841
978-601-2644 FAX 978-208-1335
E. MAIL: lach.o7812@gmail.com
NOTE: THIS DESIGN IS THE INTELLECTUAL PROPERTY OF GILBERTO JIMENEZ. ANY REUSE OR REPRODUCTION OF THIS DESIGN WITHOUT THE AUTHORIZATION OF THE AUTHOR IS PROHIBITED. COPYRIGHT © 2025 BY GILBERTO JIMENEZ.

PROJECT: COMMERCIAL RESIDENTIAL BUILDING
ADDRESS: 125 MERRIMACK ST. HAVERHILL MA 01830
OWNER: DAVINCI MINI APTS-JONY PEREZ
PETITIONER: DAVINCI MINI APTS-JONY PEREZ

REVISED BY:
APPROVED BY:
DRAWN BY: GILBERTO JIMENEZ
DATE: 7/28/2025

FLOOR PLAN
SHEET 1
15
41

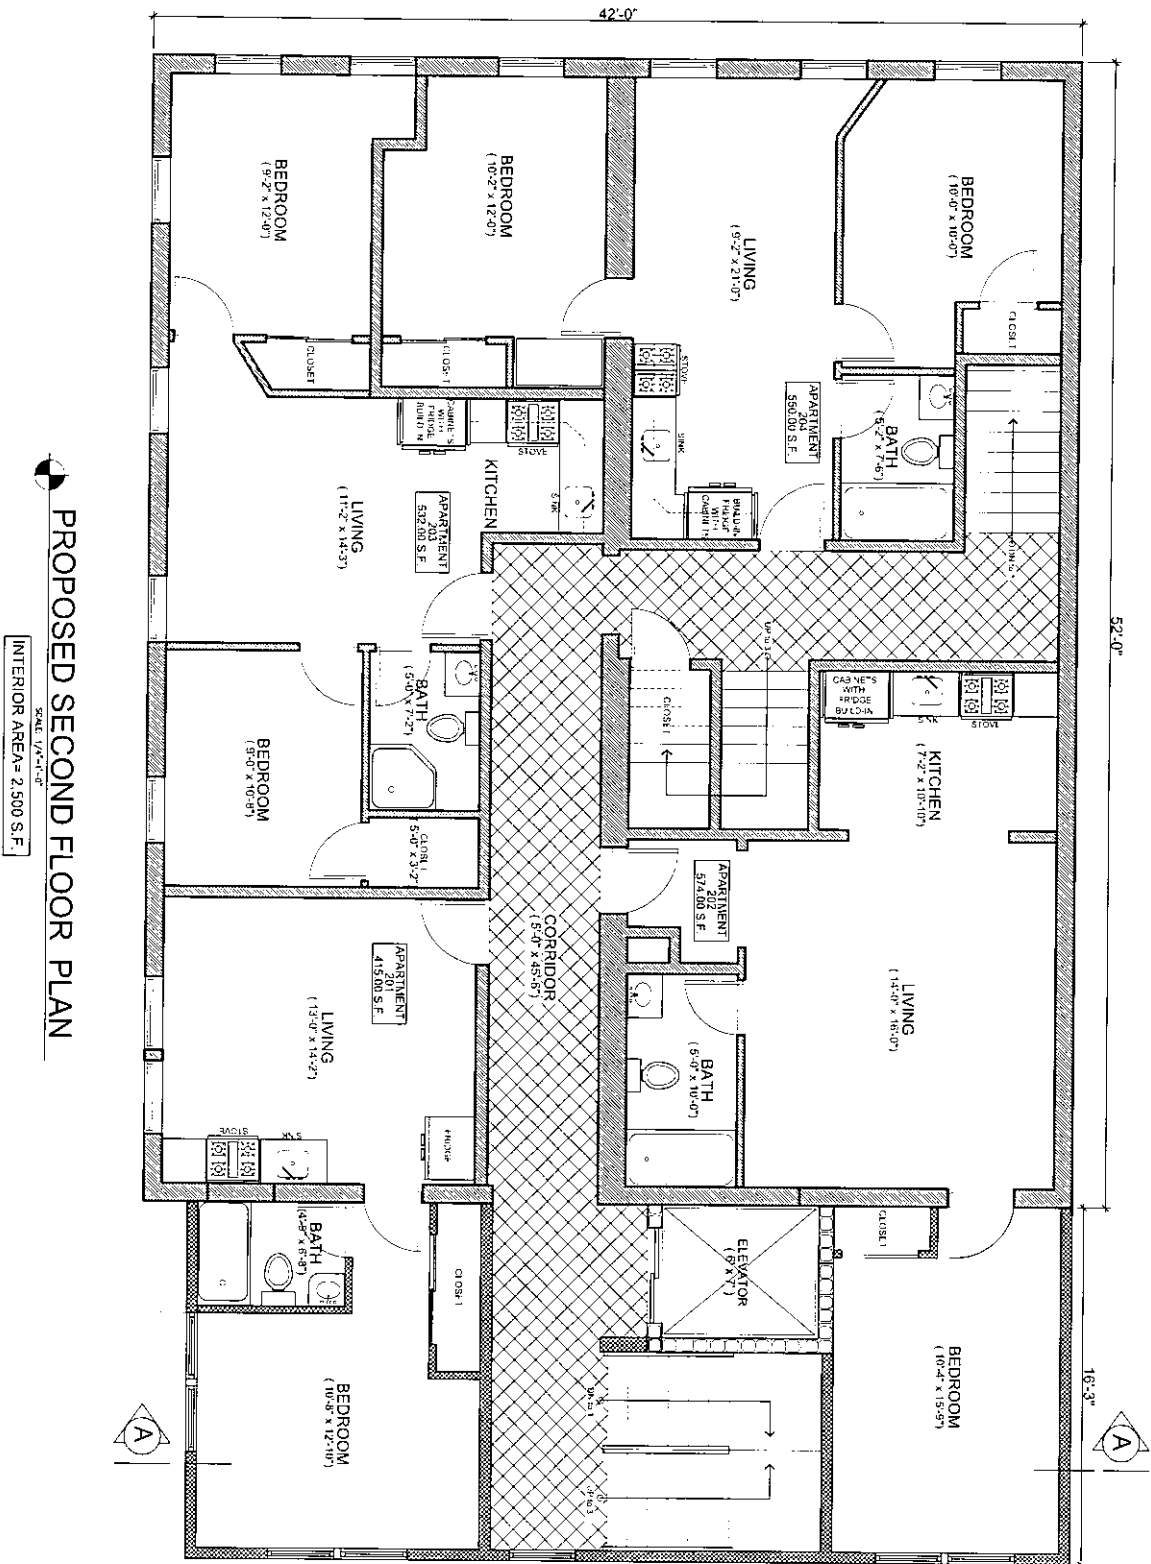

PROPOSED SECOND FLOOR PLAN

SCALE: 1/8"=1'-0"
INTERIOR AREA= 2,500 S.F.




GJ DESIGN GROUP LLC
Assoc. AIA
Professional Designer

118 WOODLAND ST LAWRENCE MA 01841
978-601-2844 FAX 978-208-1335
E. MAIL lach.07812@gmail.com
NOTE: THIS DESIGN IS THE INTELLECTUAL PROPERTY OF GILBERTO JIMENEZ GROUP. NO REPRODUCTION OR PARTIAL OR COMPLETE REPRODUCTION WITHOUT THE AUTHORIZATION OF THE AUTHOR

PROJECT: COMMERCIAL RESIDENTIAL BUILDING
ADDRESS: 125 MERRIMACK ST. HAVERHILL MA 01830
OWNER: DAVINCI MINI APTS-JONY PEREZ
PETITIONER: DAVINCI MINI APTS-JONY PEREZ


REVISED BY:
APPROVED BY:
DRAWN BY: GILBERTO JIMENEZ
DATE: 7/28/2025

FLOOR PLAN
SHEET 16
41

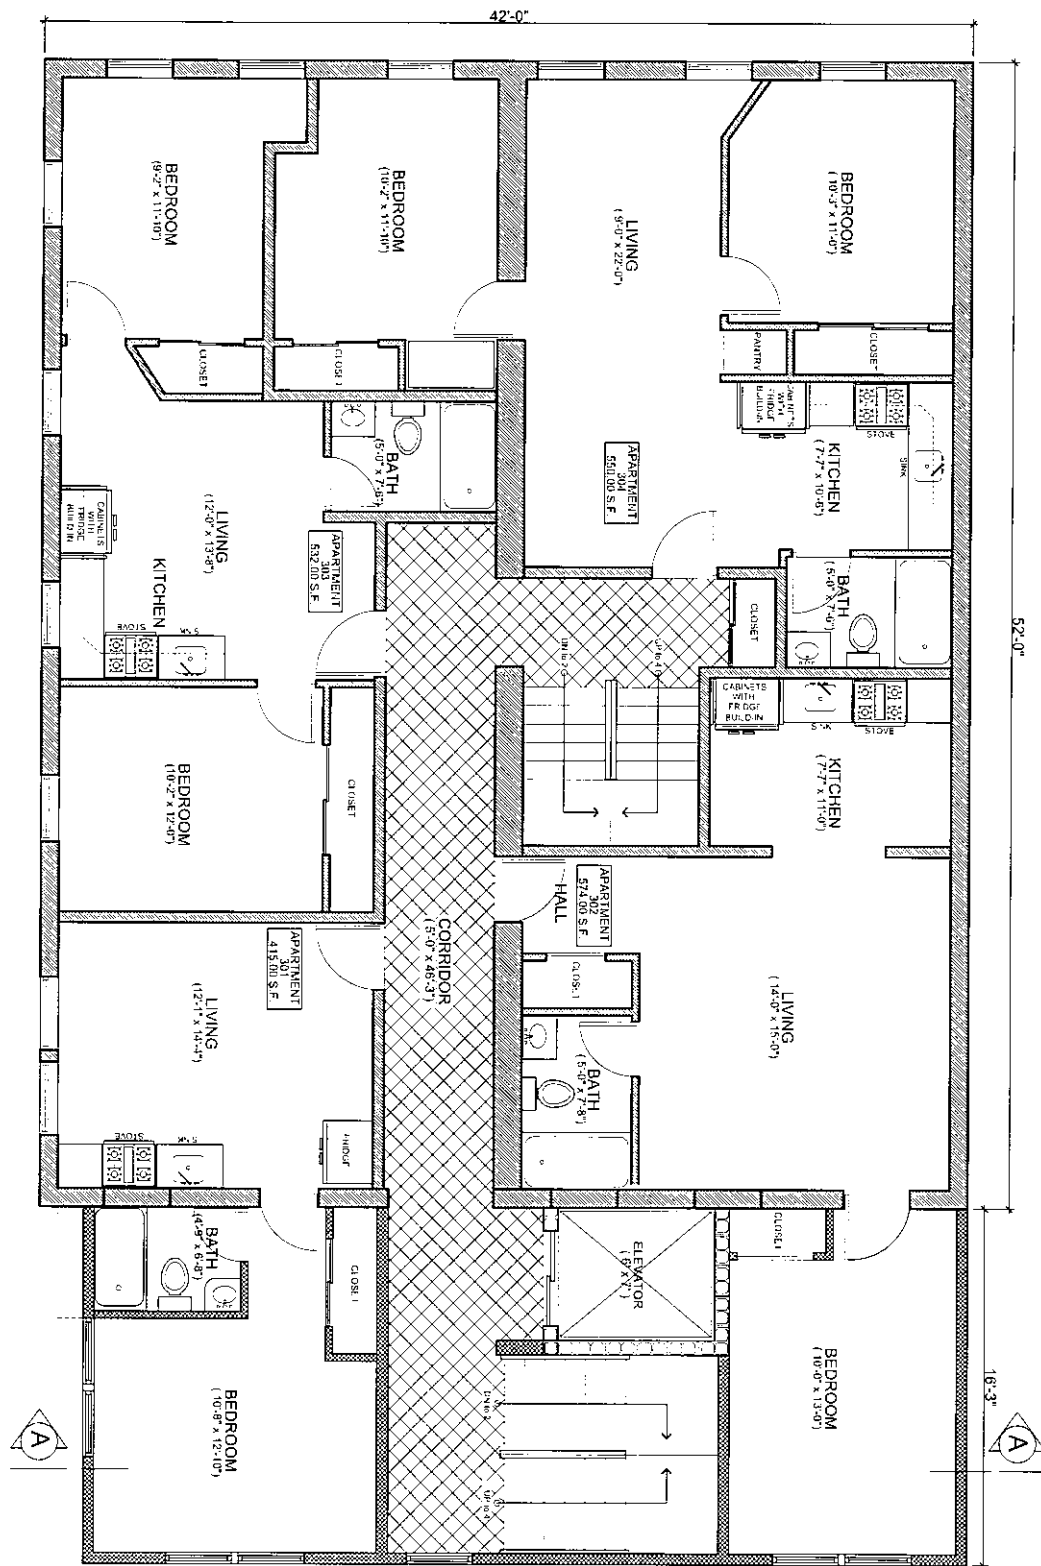

PROPOSED THIRD FLOOR PLAN


SCALE: 1/4"=1'-0"
INTERIOR AREA= 2,500 S.F.

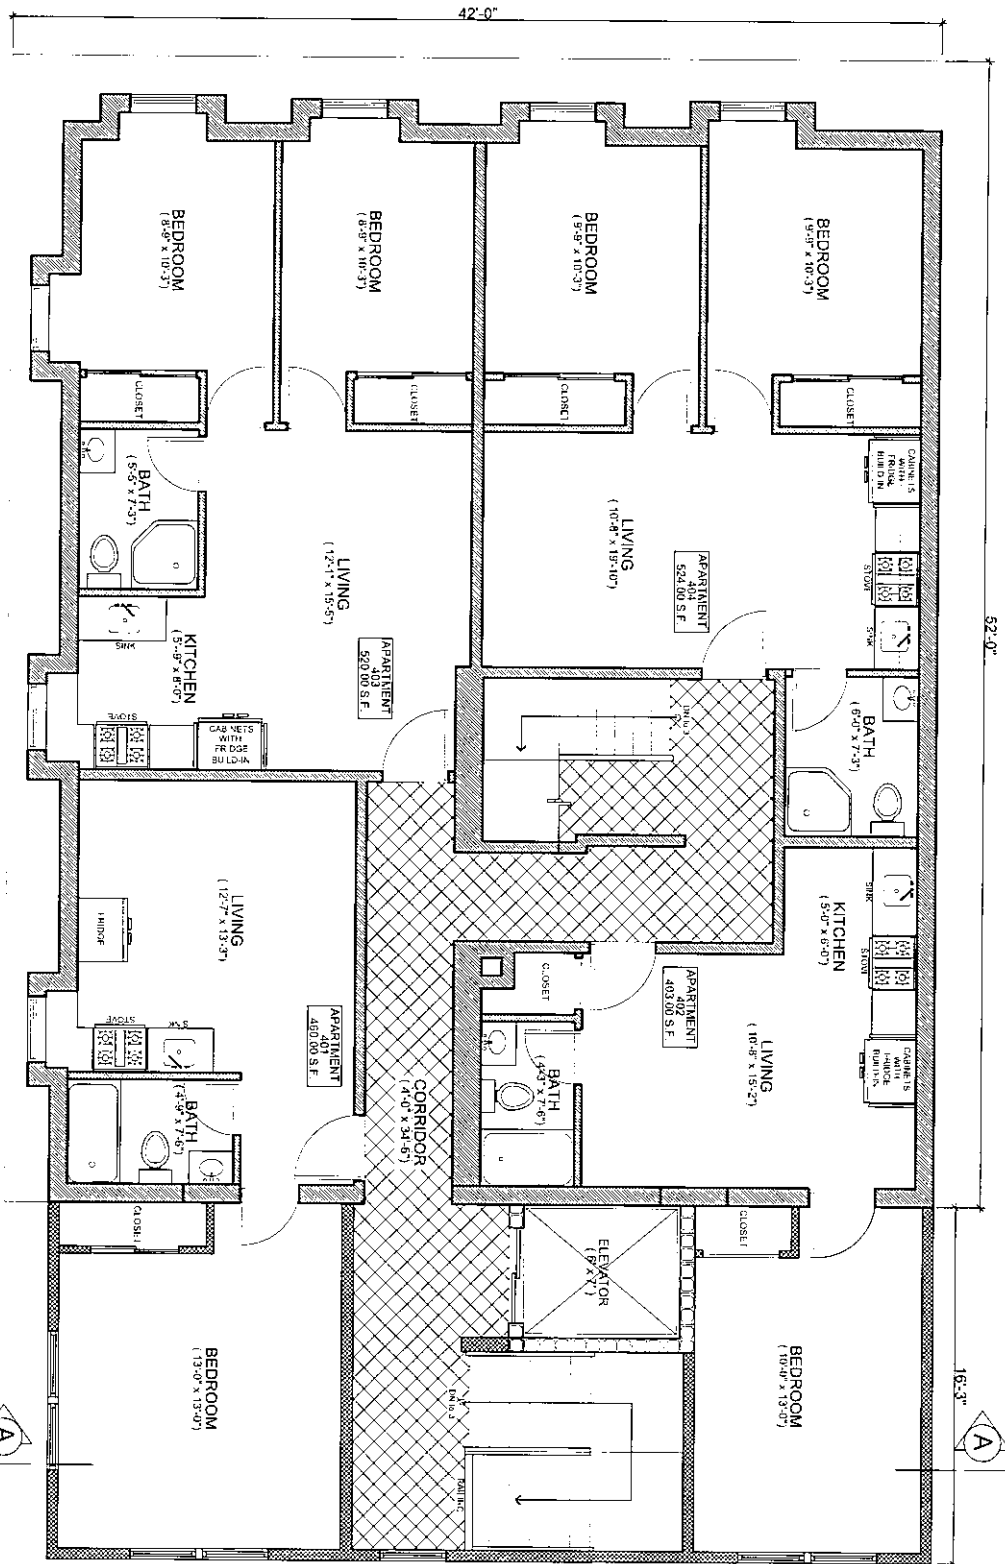

PROPOSED FOURTH FLOOR PLAN

SCAL: 1/8"=1'-0"

INTERIOR AREA= 2,500 S.F.

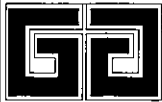

GJ
DESIGN GROUP LLC
 Assoc. AIA
 Professional Designer

118 WOODLAND ST LAWRENCE MA 01841
 978-601-2844 FAX 978-208-1335
 E. MAIL lach.07812@gmail.com
 NOTE: THIS DESIGN IS THE INTELLECTUAL PROPERTY OF
 GILBERTO JIMENEZ GROUP. IT IS
 PROHIBITED TO REPRODUCE OR COPY THIS
 DESIGN WITHOUT THE AUTHORIZATION OF THE AUTHOR


PROJECT: COMMERCIAL RESIDENTIAL BUILDING
 ADDRESS: 125 MERRIMACK ST. HAVERHILL MA 01830
 OWNER: DAVINCI MINI APTS-JONY PEREZ
 PETITIONER: DAVINCI MINI APTS-JONY PEREZ

REVISED BY:
 APPROVED BY:
 DRAWN BY: GILBERTO JIMENEZ
 DATE: 7/28/2025

FLOOR PLAN
 SHEET 1 18 41

PROPOSED RIGHT SIDE ELEVATION

SCALE 1/4" = 1'-0"

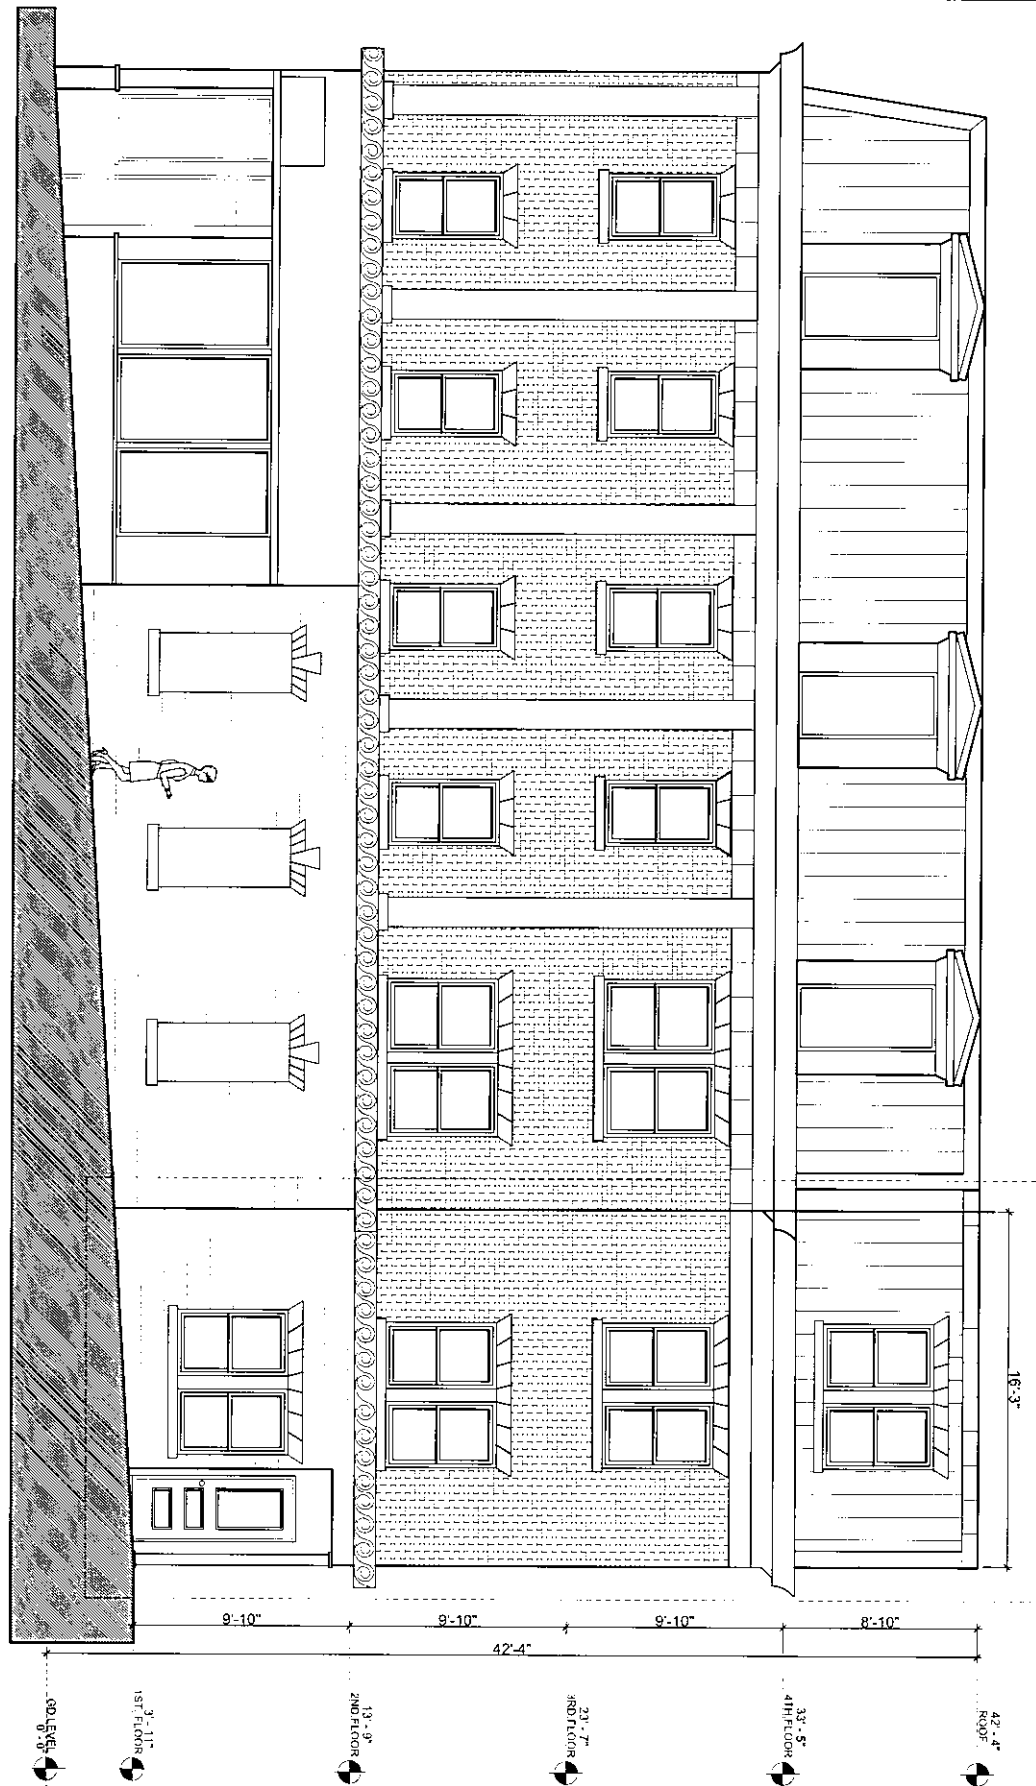

ADDITION PROPOSED

118 WOODLAND ST LAWRENCE MA 01841
978-601-2844 FAX 978-208-1335
E. MAIL lach.o7812@gmail.com


NOT: THIS DESIGN IS THE PROPERTY OF
GILBERTO JIMENEZ GROUP. BEFORE THE
PROPOSED COPY THAT A. V. OR COPY THAT A. V.
DESIGN WITHOUT THE AUTHORIZATION OF THE AUTHOR

PROJECT: COMMERCIAL RESIDENTIAL BUILDING
ADDRESS: 125 MERRIMACK ST. HAVERHILL MA 01830
OWNER: DAVINCI MINI APTS-JONY PEREZ
PETITIONER: DAVINCI MINI APTS-JONY PEREZ

REVISED BY:
APPROVED BY:
DRAWN BY: GILBERTO JIMENEZ
DATE: 7/28/2025



ELEVATION

SHEET 1 19 41

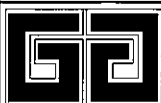

GJ
DESIGN GROUP LLC
Assoc. AIA
Professional Designer

REAR ELEVATION
SCALE 1/4" = 1'-0"

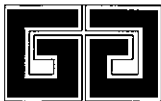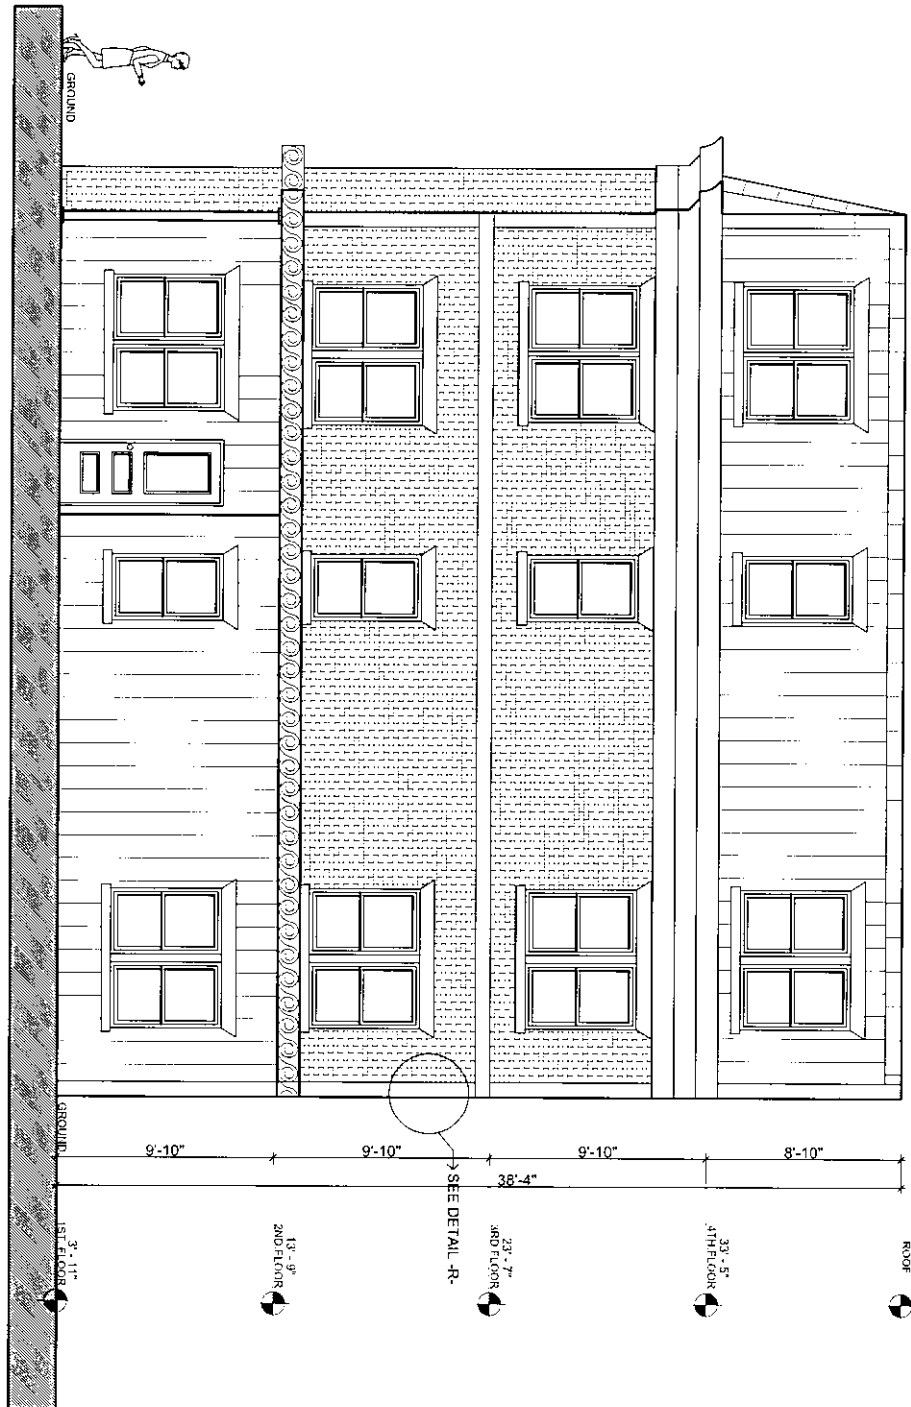


GJ
DESIGN GROUP LLC
Assoc. AIA
Professional Designer

118 WOODLAND ST LAWRENCE MA 01841
978-601-2844 FAX 978-208-1335
E. MAIL lach.07812@gmail.com
NOT: THIS DESIGN IS THE INTELLECTUAL PROPERTY OF
GILBERTO JIMENEZ GROUP. NO REUSE, REPRODUCTION,
PRODUCTION, COPY, PARTIAL OR COMPLETE, IN ANY
MANNER, WITHOUT THE AUTHORIZATION OF THE AUTHOR

PROJECT: COMMERCIAL RESIDENTIAL BUILDING
ADDRESS: 125 MERRIMACK ST. HAVERHILL MA 01830
OWNER: DAVINCI MINI APTS-JONY PEREZ
PETITIONER: DAVINCI MINI APTS-JONY PEREZ

REVISED BY:
APPROVED BY:
DRAWN BY: GILBERTO JIMENEZ
DATE: 7/28/2025

ELEVATION
SHEET 1
20
41

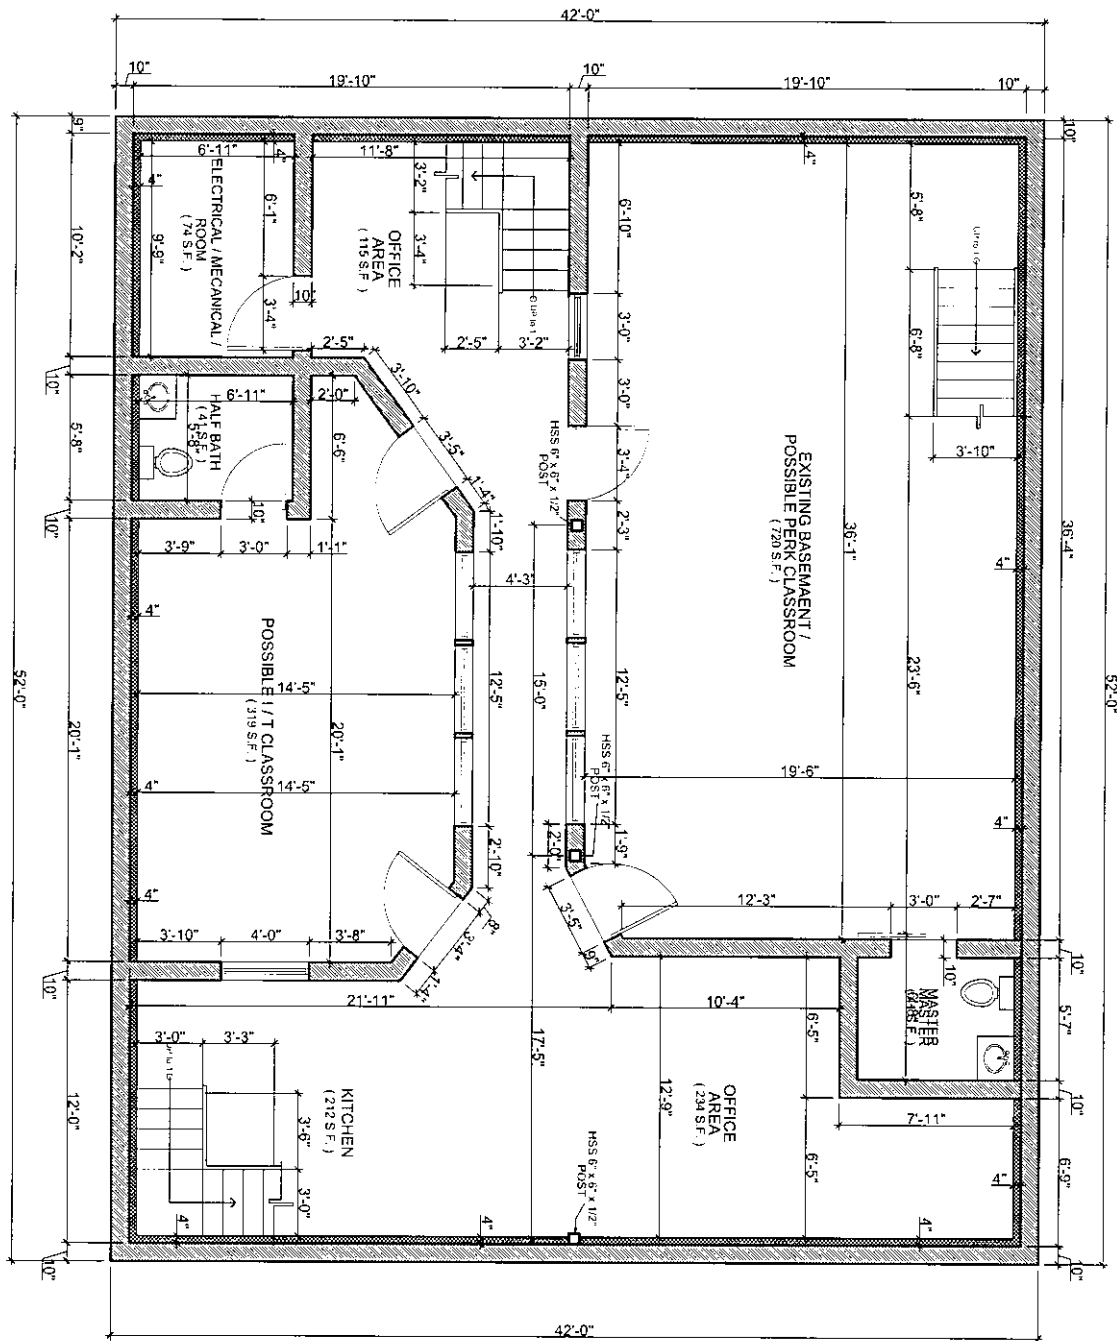

GJ DESIGN GROUP LLC
Assoc. AIA
Professional Designer

118 WOODLAND ST LAWRENCE MA 01841
978-601-2844 FAX 978-208-1335
E. MAIL lach.07812@gmail.com

NOTE: THIS DESIGN IS THE INTELLECTUAL PROPERTY OF GILBERTO JIMENEZ GROUP. THEREFORE, THE PROPOSED CONSTRUCTION OR CONSTRUCTION DESIGNATION OF THE AUTHOR ORIGIN OF THE AUTHOR


PROJECT: COMMERCIAL RESIDENTIAL BUILDING
ADDRESS: 125 MERRIMACK ST. HAVERHILL MA 01830
OWNER: DAVINCI MINI APTS-JONY PEREZ
PETITIONER: DAVINCI MINI APTS-JONY PEREZ

REVISED BY:
APPROVED BY:
DRAWN BY: GILBERTO JIMENEZ
DATE: 7/28/2025

FLOOR PLAN

SHEET 1
21
41



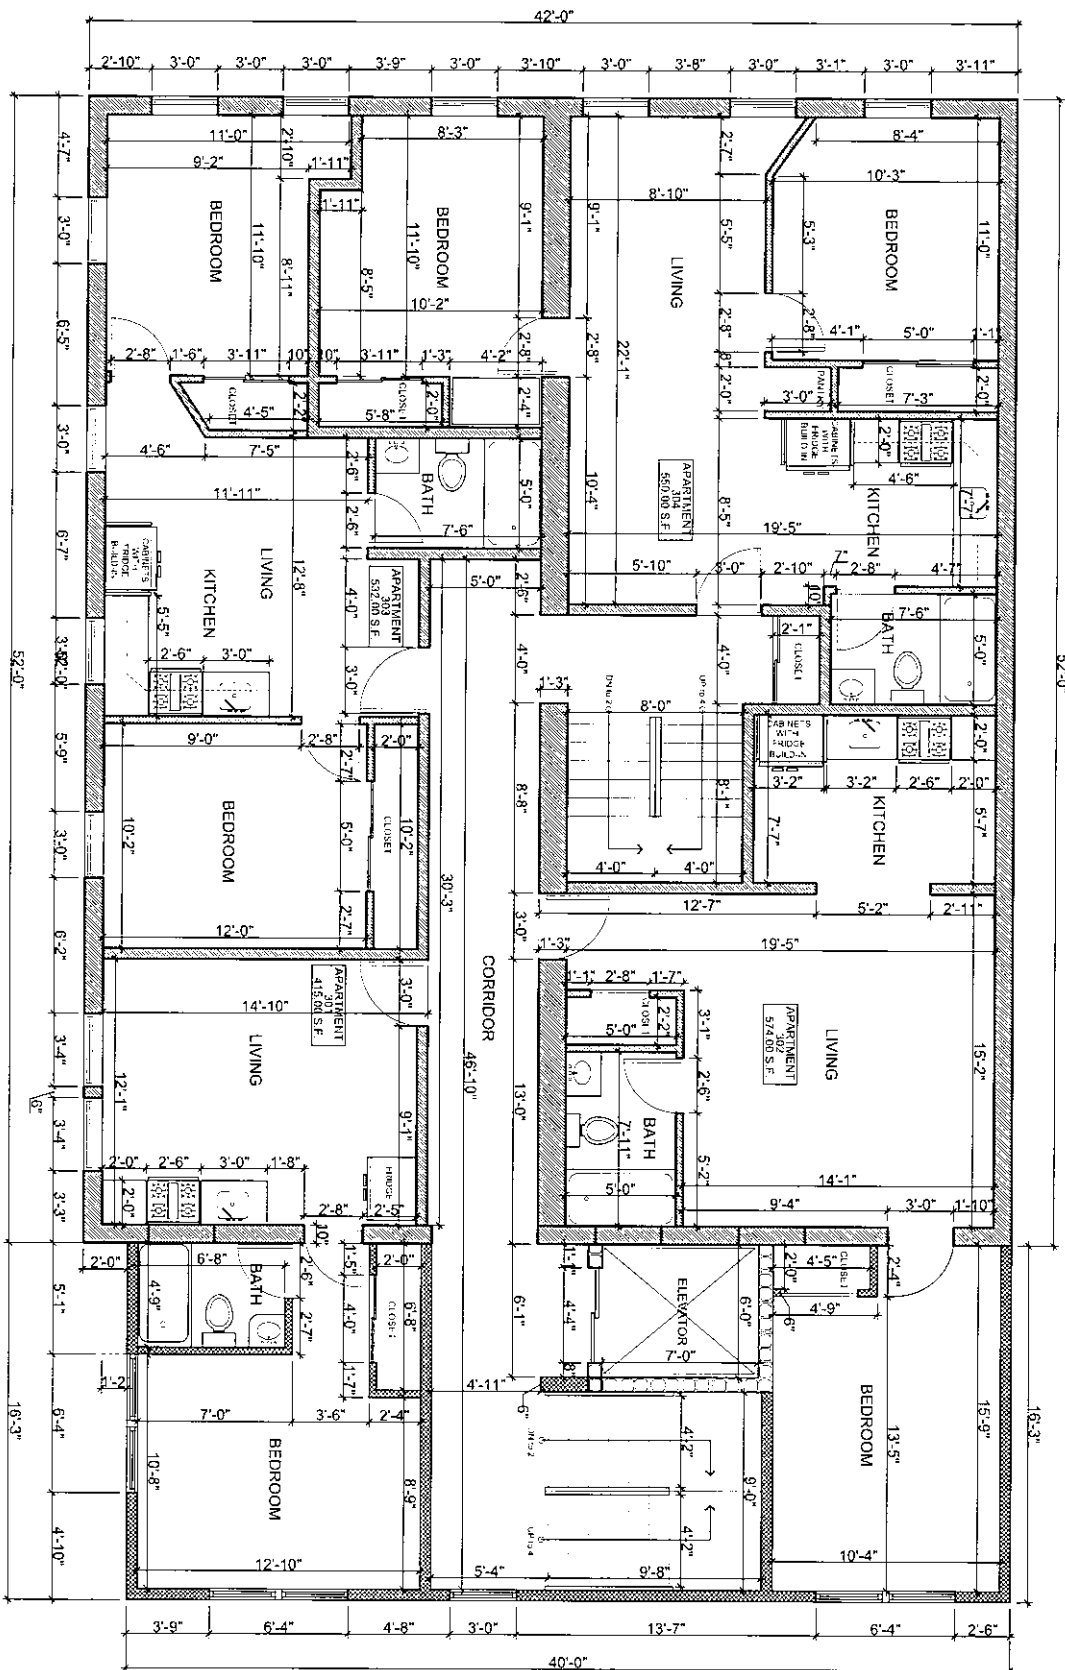

GJ
DESIGN GROUP LLC
Assoc. AIA
Professional Designer

118 WOODLAND ST LAWRENCE MA 01841
978-601-2844 FAX 978-208-1335
E. MAIL: lach.o7812@gmail.com



NOTES: THIS DESIGN IS THE PROPERTY OF GILBERTO JIMENEZ GROUP. IT IS NOT TO BE REPRODUCED OR COPIED IN ANY FORM WITHOUT THE WRITTEN PERMISSION OF THE AUTHOR.

PROJECT: COMMERCIAL RESIDENTIAL BUILDING
ADDRESS: 125 MERRIMACK ST. HAVERHILL MA 01830
OWNER: DAVINCI MINI APTS-JONY PEREZ
PETITIONER: DAVINCI MINI APTS-JONY PEREZ

REVISED BY:
APPROVED BY:
DRAWN BY: GILBERTO JIMENEZ
DATE: 7/28/2025

FLOOR PLAN
SHEET 1
24
41

(DIMENSIONED)
PROPOSED FOURTH FLOOR PLAN
 SCALE: 1/4" = 1'-0"
 INTERIOR AREA = 2,500 S.F.

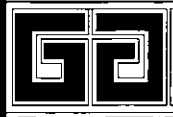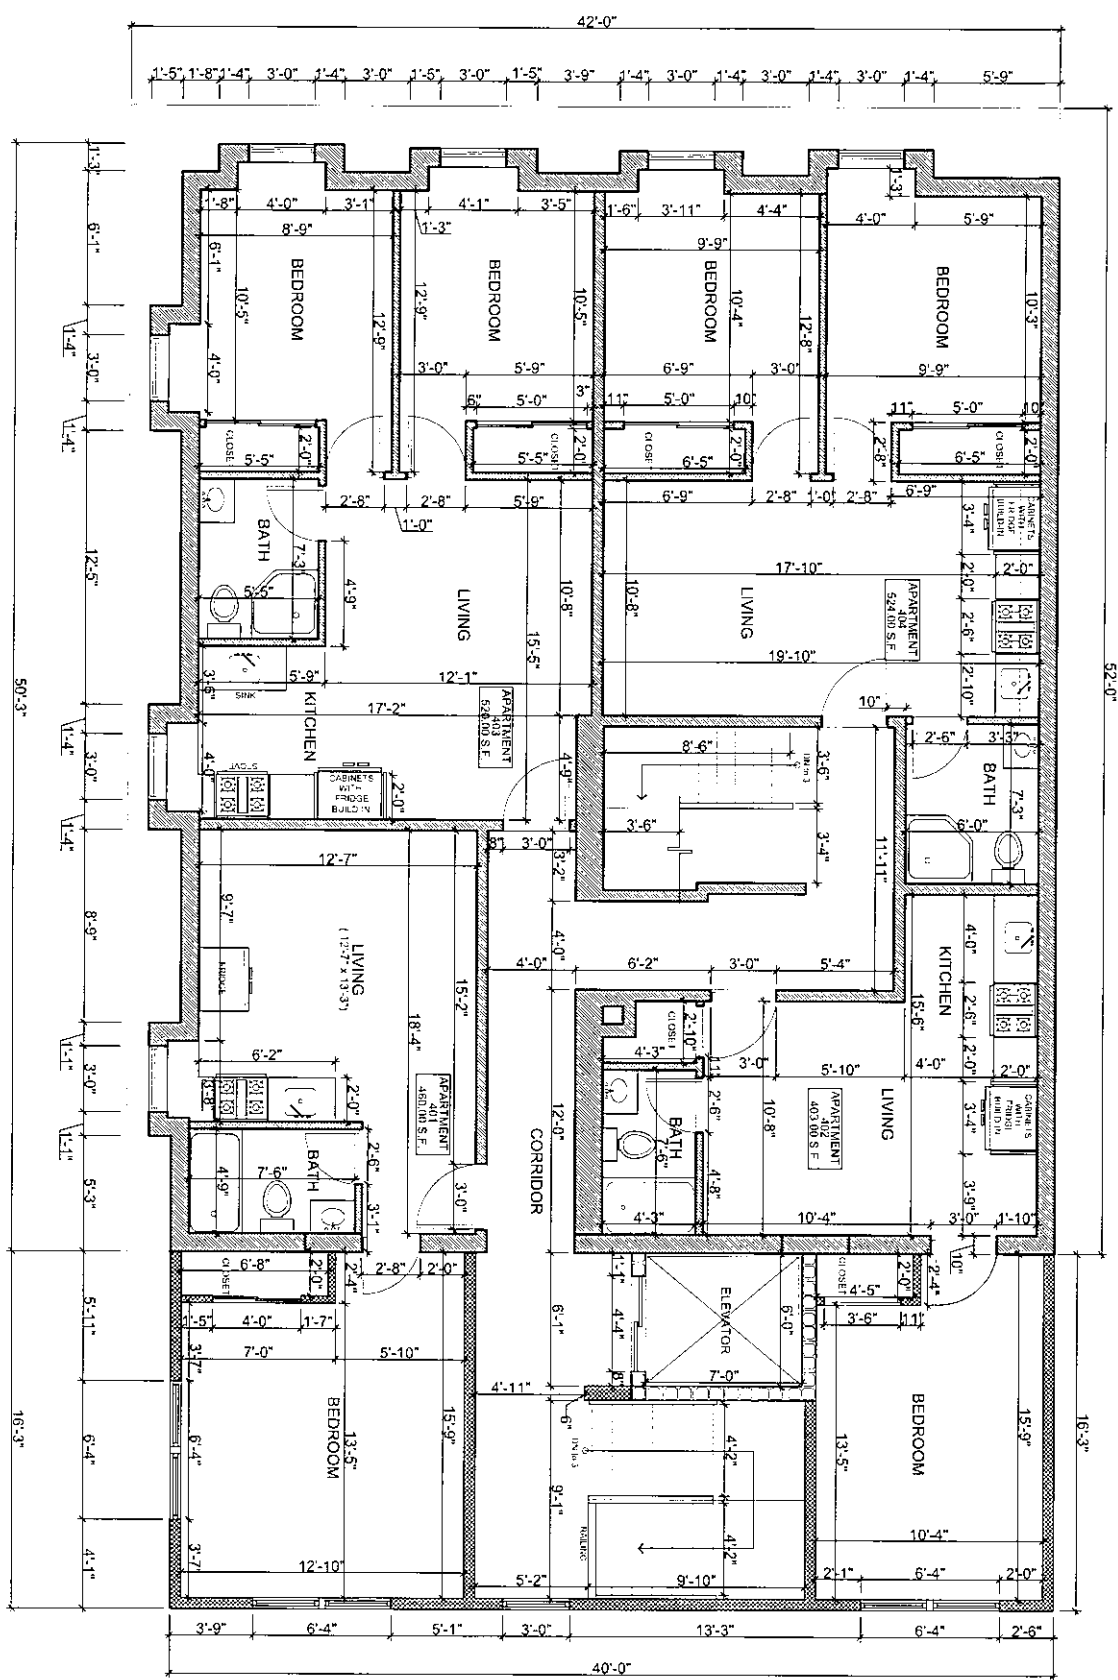


GJ DESIGN GROUP LLC
 Assoc. AIA
 Professional Designer

118 WOODLAND ST LAWRENCE MA 01841
 978-601-2844 FAX 978-208-1335
 E. MAIL lach.o7812@gmail.com
 NOTE: THIS DESIGN IS THE INTELLECTUAL PROPERTY OF GILBERTO JIMENEZ GROUP. THEREFORE, IT IS PROHIBITED TO COPY PARTIALLY OR COMPLETELY THIS DESIGN WITHOUT THE AUTHORIZATION OF THE AUTHOR.


PROJECT: COMMERCIAL RESIDENTIAL BUILDING
 ADDRESS: 125 MERRIMACK ST. HAVERHILL MA 01830
 OWNER: DAVINCI MINI APTS-JONY PEREZ
 PETITIONER: DAVINCI MINI APTS-JONY PEREZ

REVISED BY:
 APPROVED BY:
 DRAWN BY: GILBERTO JIMENEZ
 DATE: 7/28/2025

FLOOR PLAN
 SHEET 1
 25
 41

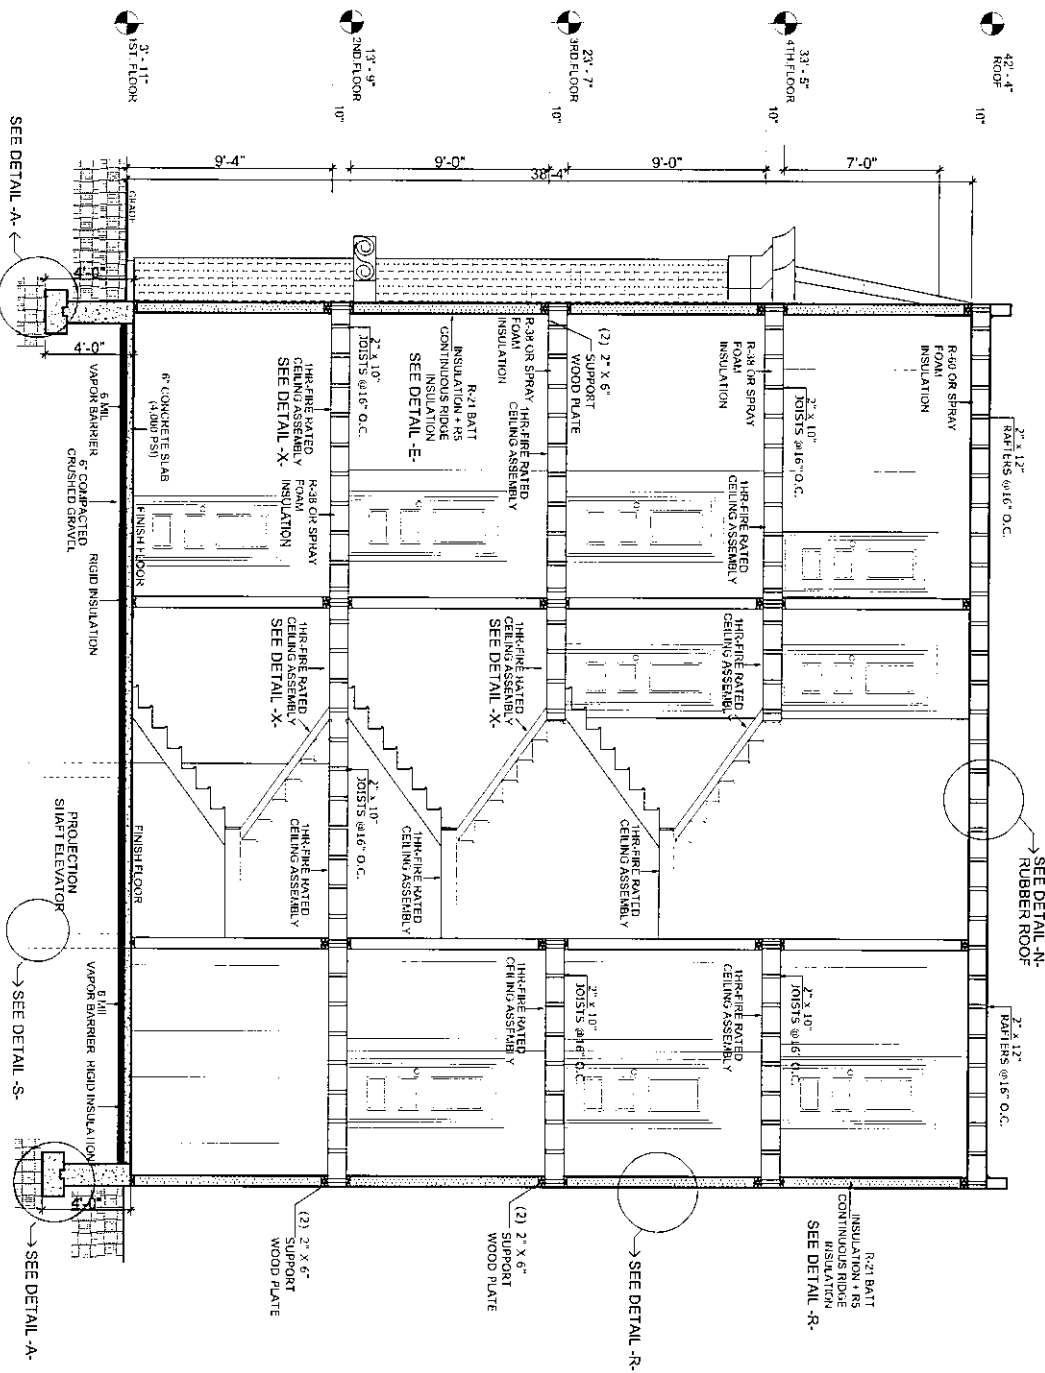

SECTION A-A
SCALE 1/4\"/>

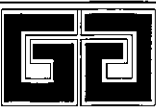


6J
DESIGN GROUP LLC
Assoc. AIA
Professional Designer

118 WOODLAND ST LAWRENCE MA 01841
978-601-2844 FAX 978-208-1335
E. MAIL lach.o7812@gmail.com
NOTE: THIS DESIGN IS THE EXCLUSIVE PROPERTY OF
GILBERTO JIMENEZ GROUP. NO PART OF THIS
DESIGN MAY BE REPRODUCED OR TRANSMITTED IN
ANY FORM OR BY ANY MEANS WITHOUT THE
WRITTEN PERMISSION OF THE AUTHOR.


PROJECT: COMMERCIAL RESIDENTIAL BUILDING
ADDRESS: 125 MERRIMACK ST. HAVERHILL, MA 01830
OWNER: DAVINCI MINI APTS-JONY PEREZ
PETITIONER: DAVINCI MINI APTS-JONY PEREZ

REVISED BY:
APPROVED BY:
DRAWN BY: GILBERTO JIMENEZ
DATE: 7/28/2025

FLOOR PLAN
SHEET 1
26
41

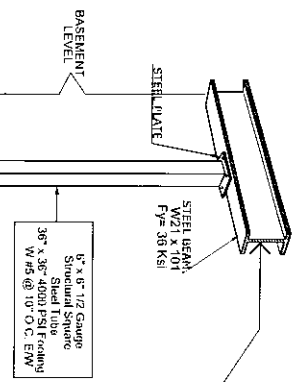


DETAIL -C- STEEL BEAM
N.T.S.

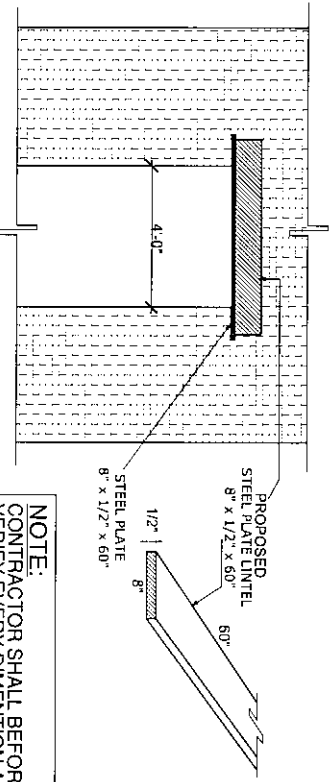


DETAIL -C- STEEL BEAM
N.T.S.


NOTE:
CONTRACTOR SHALL BEFORE START WORK,
VERIFY EVERY DIMENSION AND HEIGHT

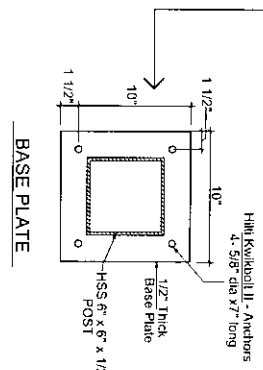


DETAIL -C-
N.T.S.

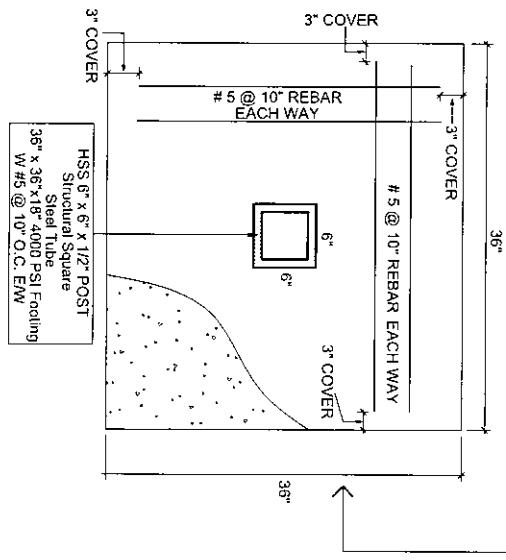

COLUMN FOOTING
DETAIL -C-
N.T.S.

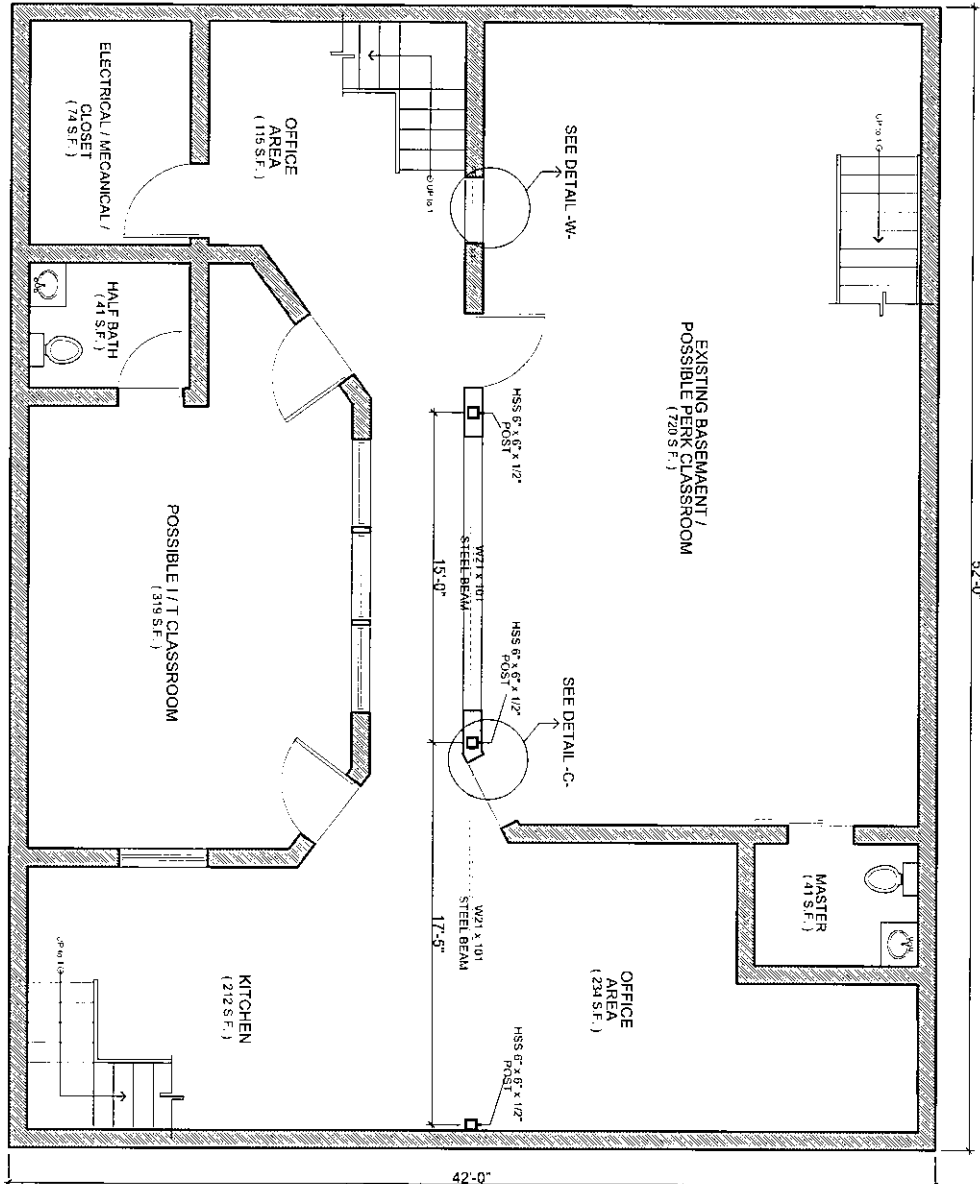

(STRUCTURAL)
BASEMENT FLOOR PLAN
SCALE 1/4" = 1'-0"

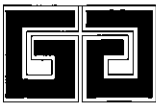

GJ DESIGN GROUP LLC
Assoc. AIA
Professional Designer

118 WOODLAND ST LAWRENCE MA 01841
978-601-2844 FAX 978-208-1335
E. MAIL lach.o7812@gmail.com
NOTE: THIS DOCUMENT IS THE PROPERTY OF GILBERTO JIMENEZ GROUP. IT IS TO BE USED ONLY FOR THE PROJECT AND NOT TO BE REPRODUCED OR COPIED IN ANY MANNER WITHOUT THE WRITTEN AUTHORIZATION OF THE DESIGNER.


PROJECT: COMMERCIAL RESIDENTIAL BUILDING
ADDRESS: 125 MERRIMACK ST. HAVERHILL MA 01830
OWNER: DAVINCI MINI APTS-JONY PEREZ
PETITIONER: DAVINCI MINI APTS-JONY PEREZ

REVISED BY:
APPROVED BY:
DRAWN BY: GILBERTO JIMENEZ
DATE: 7/28/2025

FLOOR PLAN
SHEET 1
27
41

GENERAL NOTES :

- 1-CONTRACTOR SHALL PERFORM ALL WORKS IN COMPLIANCE WITH THE COMMONWEALTH OF MASSACHUSETTS (10 TH EDITION OF THE MISC. 780 CMR) AND THE CITY OF HAVERHILL ORDINANCES.
- 2-CONTRACTOR SHALL BE SOLELY RESPONSIBLE FOR ALL CONSTRUCTION MEANS, METHODS, TECHNIQUES, AND PROCEDURES.
- 3-CONTRACTOR SHALL BE RESPONSIBLE FOR ALL ASPECTS DURING BUILDING CONSTRUCTION AND SHALL PROVIDE ADEQUATE SHORING AND BRACING TO ENSURE SAFETY.
- 4-ALL DIMENSIONS AND SITE CONDITIONS SHALL BE FIELD VERIFIED AND SHALL BE THE RESPONSIBILITY OF THE CONTRACTOR NOTIFY THE OWNER OR DESIGNER OF ANY DISCREPANCY BEFORE STARTING WORK.
- 5-IT SHALL BE THE RESPONSIBILITY OF THE CONTRACTOR TO LOCATE ALL EXISTING UTILITIES AND TO PROTECT THEM FROM DAMAGE.
- 6- ALL DETAILS, SECTIONS, NOTES OR REFERENCE TO OTHER DRAWINGS ARE INTENDED TO BE TYPICAL.
- 7-DURING CONSTRUCTION AND BEFORE ANY CHANGES, REVISIONS, MODIFICATIONS OR DEVIATION FROM THE CONSTRUCTION DOCUMENT, CONTRACTOR SHALL BRING TO THE ATTENTION OF THE OWNER OR DESIGNER AND OBTAIN APPROVAL FROM THE BUILDING INSPECTOR BEFORE PROCEEDING WITH THE WORK.
- 8-SPECIFIC NOTES AND DETAILS ON THE DRAWINGS SHALL TAKE PRECEDENCE OVER GENERAL NOTES AND TYPICAL DETAILS WHERE THE DRAWINGS DO NOT SHOW DETAILS. CONSTRUCTION SHALL CONFORM TO SIMILAR WORK ON THE PROJECT.

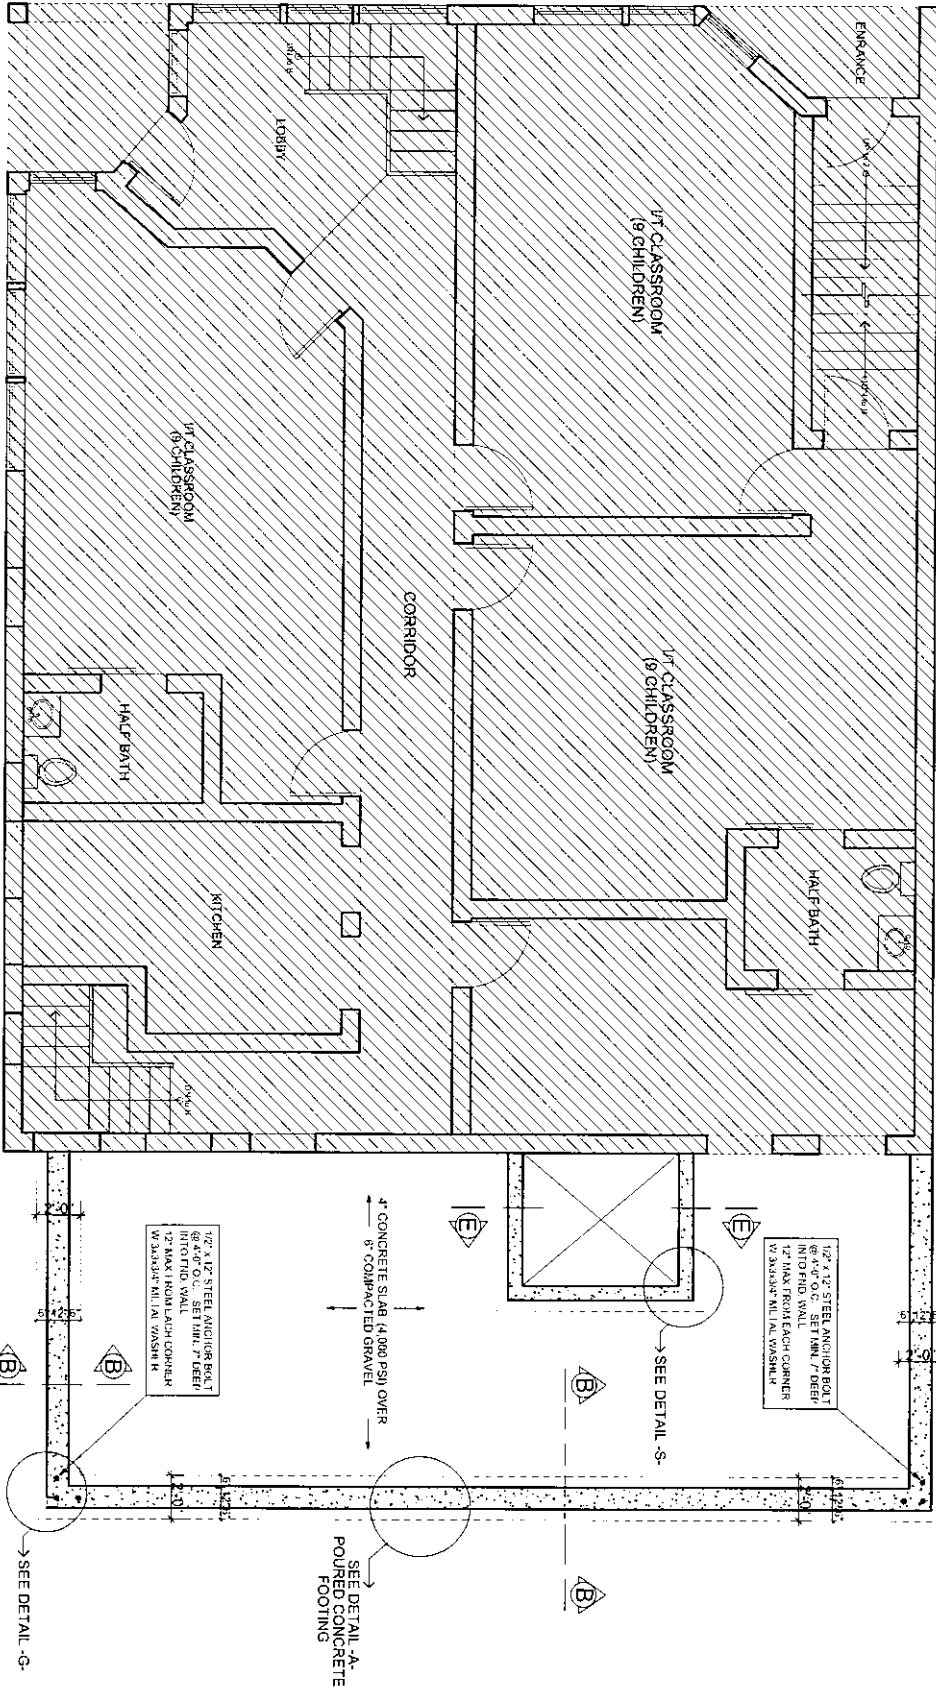

NOTE:


CONTRACTOR SHALL BEFORE START WORK
VERIFY EVERY DIMENTION AND HEIGHT

NOTE:

CONTRACTOR MUST CALL DIG SAFE
BEFORE PERFORMING ANY EXCAVATION

FOUNDATION PLAN

SCALE: 1/4" = 1'-0"

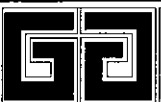

GJ DESIGN GROUP LLC
Assoc. AIA
Professional Designer


118 WOODLAND ST LAWRENCE MA 01841
978-601-2844 FAX 978-208-1335
E. MAIL: lach.o7812@gmail.com

NOTE: THIS DESIGN IS THE INTELLECTUAL PROPERTY OF
GILBERTO JIMENEZ GROUP. THEREFORE THE
PROHIBITED COPIES, REPRODUCTIONS OR
REPRODUCTION OF THIS DESIGN WITHOUT THE AUTHORIZATION OF THE AUTHOR


PROJECT: COMMERCIAL RESIDENTIAL BUILDING
ADDRESS: 125 MERRIMACK ST. HAVERHILL MA 01830
OWNER: DAVINCI MINI APTS-JONY PEREZ
PETITIONER: DAVINCI MINI APTS-JONY PEREZ

REVISED BY:
APPROVED BY:
DRAWN BY: GILBERTO JIMENEZ
DATE: 7/28/2025


FOUNDATION
PLAN
1 28 41

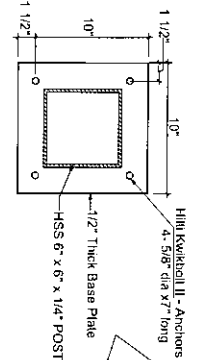


BASE PLATE

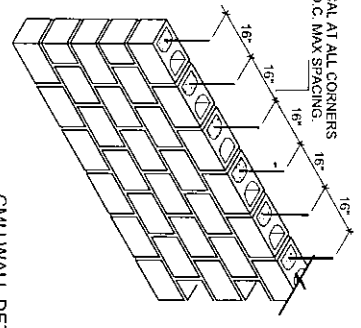

CMU WALL DETAIL

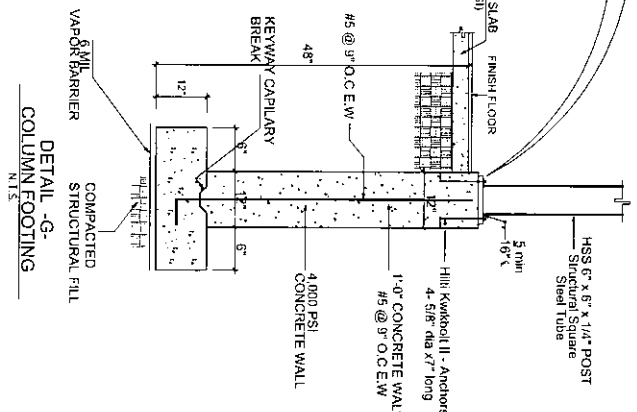


DETAIL - G- COLUMN FOOTING

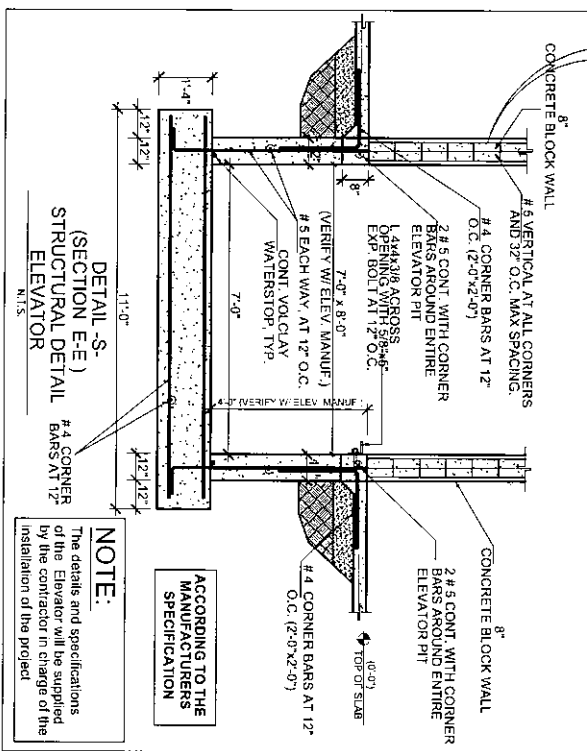


DETAIL - S- (SECTION E-E) STRUCTURAL DETAIL ELEVATOR

NOTE:
The details and specifications of the Elevator will be supplied by the contractor in charge of the installation of the project.

ACCORDING TO THE MANUFACTURERS SPECIFICATION

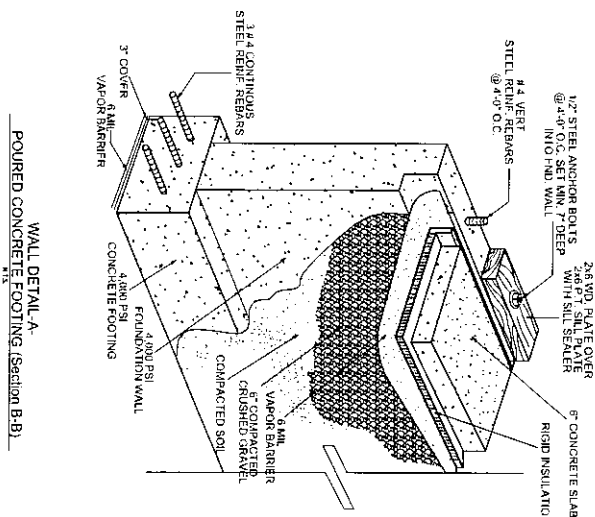

WALL DETAIL - A- POURED CONCRETE FOOTING (Section B-B)

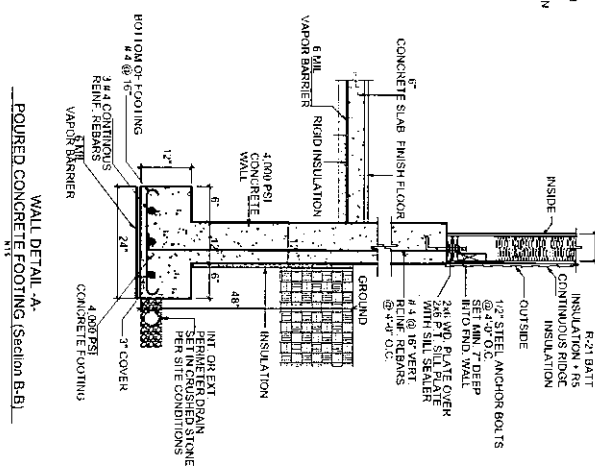

WALL DETAIL - A- POURED CONCRETE FOOTING (Section B-B)

CONCRETE NOTES

1. ALL CONCRETE TO BE 4,000 PSI @ 28 DAYS AND PLACED IN ACCORDANCE WITH INDUSTRY STANDARDS. DO NOT STRIP FORMS FOR 72 HOURS.
2. FOOTINGS TO BE PLACED ON UNDISTURBED NATIVE SOILS. NOTIFY ARCHITECT IN THE EVENT OF ANY OVER-EXCAVATION BEFORE PROCEEDING WITH WORK.
3. ALL STEEL REINFORCING TO BE NEW AND PLACED IN ACCORDANCE WITH INDUSTRY STANDARDS, AND FREE OF RUST, SCALE, DIRT OR OTHER DEBRIS.
4. CONCRETE CONTRACTOR TO VERIFY LOCATIONS OF ALL HOLD-DOWNS WITH FRAMING CONTRACTOR.
5. COORDINATE LOCATION OF ALL BONDOUTS FOR WATER, SEWER, ELECTRICAL AND OTHER UNDERGROUND UTILITIES.
6. IN AREAS WHERE FOUNDATION WALLS ARE TO BE LEFT EXPOSED TO VIEW, GRIND SMOOTH ALL FORM JOINTS AND FILL ALL THE HOLES BEFORE APPLYING PARING.


FOUNDATION WALL TYPICAL NOTE:

- 12" POURED CONCRETE WALL WITH 2'-0" X 1'-0" FOOTING

COLUMN FOOTING/THICKENED SLAB SCHEDULE:

- OVER FOUNDATION CONCRETE WALL


TYPICAL METAL CONNECTIONS

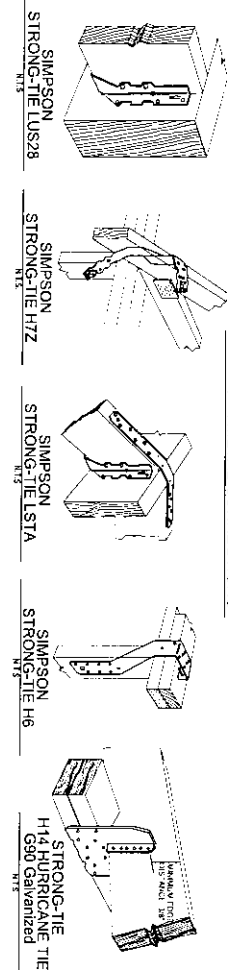



NOTE

G) Design Group, LLC made these plans to comply with owners' and builders' specifications. Any changes made to prints will be at the owners' and builder's expense and responsibility. The contractors shall verify all dimensions and enclosed drawings details before construction and be solely responsible after that.


DOOR OPENING DETAIL

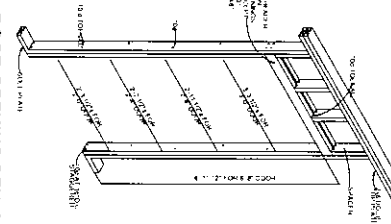


DETAIL -X- 1HR-RATED CEILING ASSEMBLY

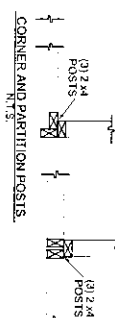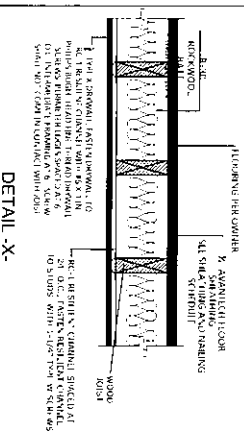


DESIGN GROUP, LLC made these plans to comply with owners' and builders' specifications. Any changes made to prints will be at the owners' and builder's expense and responsibility. The contractors shall verify all dimensions and enclosed drawings details before construction and be solely responsible after that.

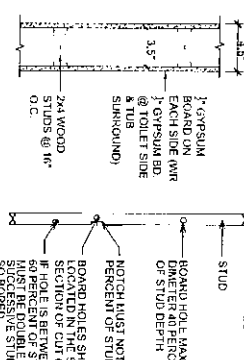


JOIST SUPPORTED ON WOOD GIRDERS

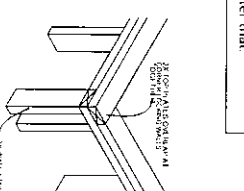

TOP PLATE FRAMING DETAIL

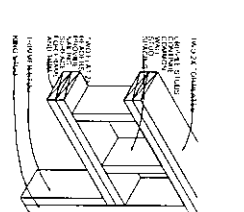

2x PARTITION WALL HEADER DETAIL

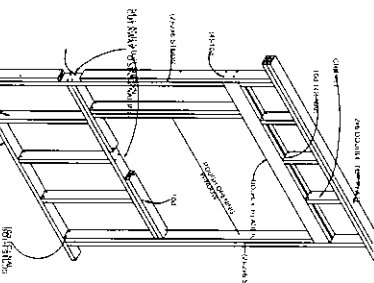


WINDOW OPENING DETAIL

PROJECT: COMMERCIAL RESIDENTIAL BUILDING
ADDRESS: 125 MERRIMACK ST. HAVERHILL MA 01830
OWNER: DAVINCI MINI APTS-JONY PEREZ
PETITIONER: DAVINCI MINI APTS-JONY PEREZ



REVISED BY:
APPROVED BY:
DRAWN BY: GILBERTO JIMENEZ
DATE: 7/28/2025

STRUCTURAL DETAILS
SHEET 1 30 41


DETAIL -E- INTERIOR WALL

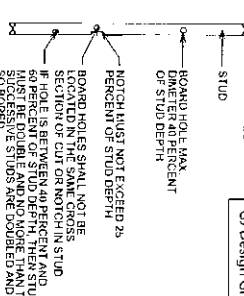


SECTION Z

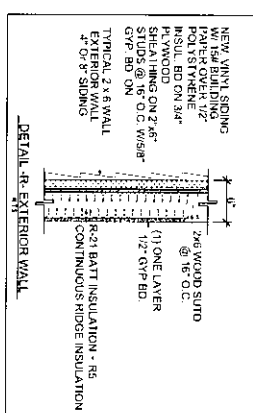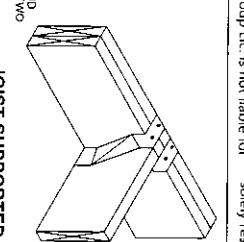



1 INSULATED WALL DETAILS

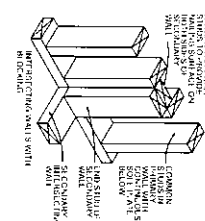

2 INSULATED WALL DETAILS

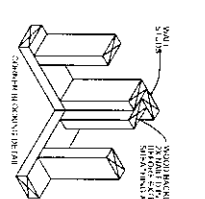

3 2x6 BEARING WALL HEADER DETAIL

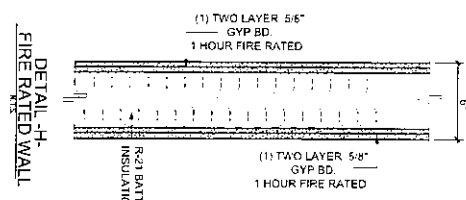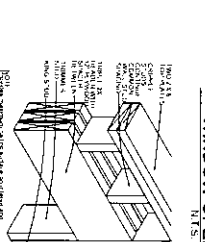

DETAIL -H- FIRE RATED WALL




DETAIL -R- EXTERIOR WALL

NOTE:
1. WITH SPRINKLER SYSTEM
2x6 STUDS @ 16" O.C. w/ ONE LAYER 5/8" SHEETROCK FIRE CODE EACH SIDE. (1 HR. FIRE-RATED).
2. WITHOUT SPRINKLER SYSTEM
2x6 STUDS @ 16" O.C. w/ TWO LAYER 5/8" SHEETROCK FIRE-CODE EACH SIDE. (2 HR. FIRE-RATED).

TYPICAL DETAILS

DOUBLE JOIST AT PARALLEL WALLS


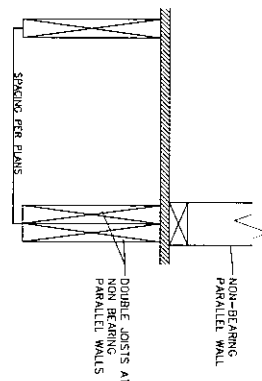


DESIGN GROUP LLC
Assoc. AIA
Professional Designer

118 WOODLAND ST LAWRENCE MA 01841
978-601-2844 FAX 978-208-1335
E. MAIL lach.07812@gmail.com

NOTE:
CONTRACTOR SHALL PERFORM ALL WORKS IN COMPLIANCE WITH THE COMMONWEALTH OF MASSACHUSETTS (10TH EDITION OF THE MBSC/780 CMR) (2021 IBC AND THE COMMONWEALTH OF MASSACHUSETTS' AMENDMENT TO THE INTERNATIONAL COMMERCIAL CODE 2021) AND THE CITY OF HAVERHILL ORDINANCES.



NOTE:
CONTRACTOR/INSTALLER TO COORDINATE HANDRAIL ATTACHMENT & BLOCKING WITH RESISTENT CHANNELS ON DEMISING WALL

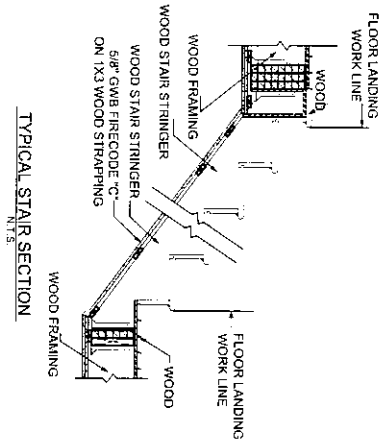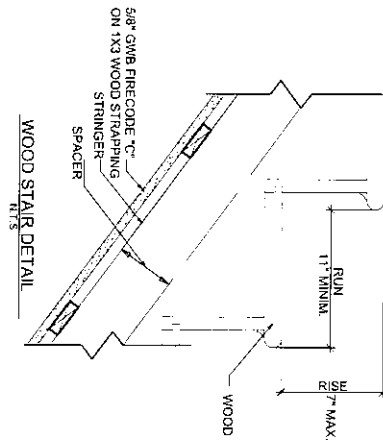




DETAILS STAIR
N.T.S.

WALL HANDRAIL BRACKET MOUNTING DETAIL
N.T.S.


PICKET RAIL INTERMEDIATE POST
N.T.S.

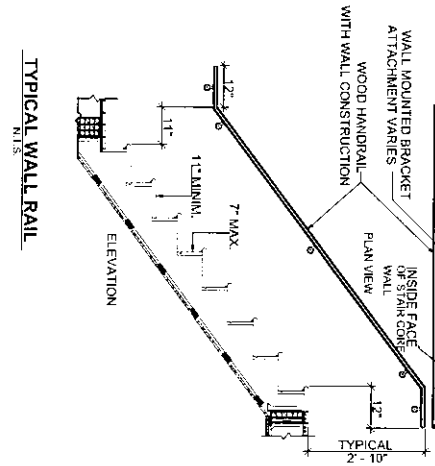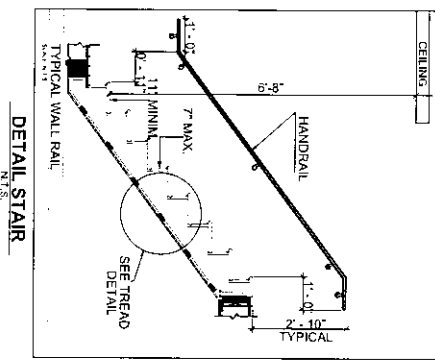

TYPICAL DETAILS STAIR
N.T.S.

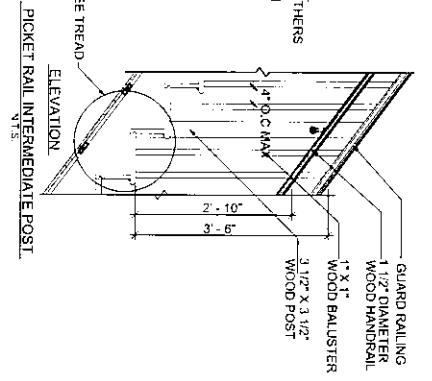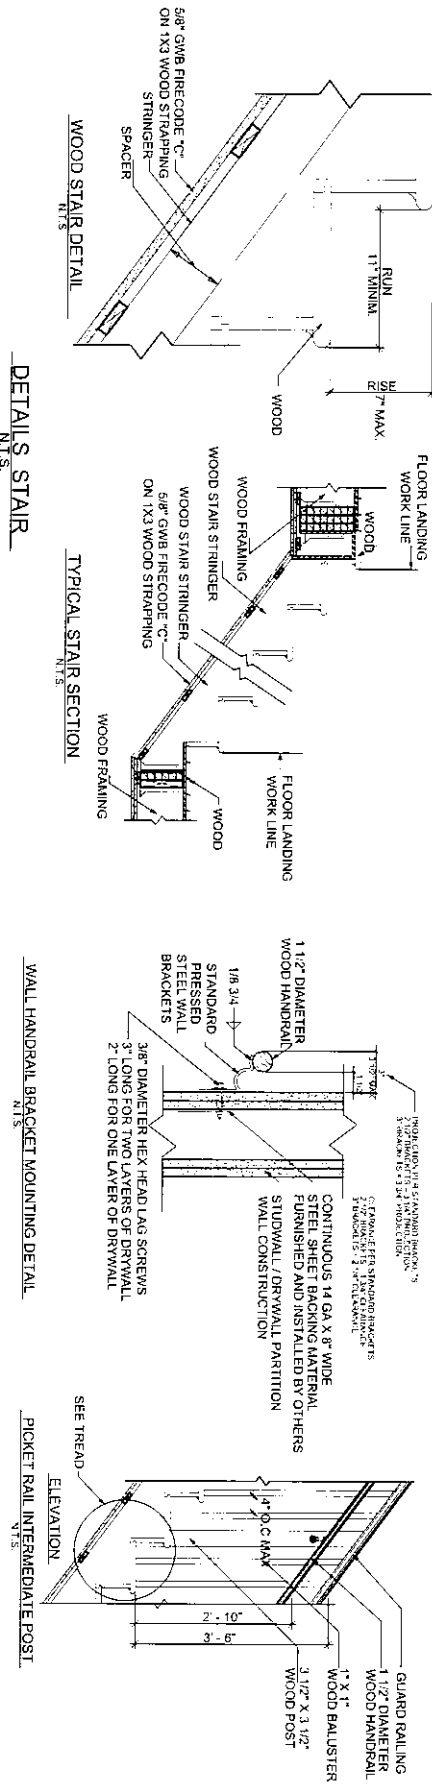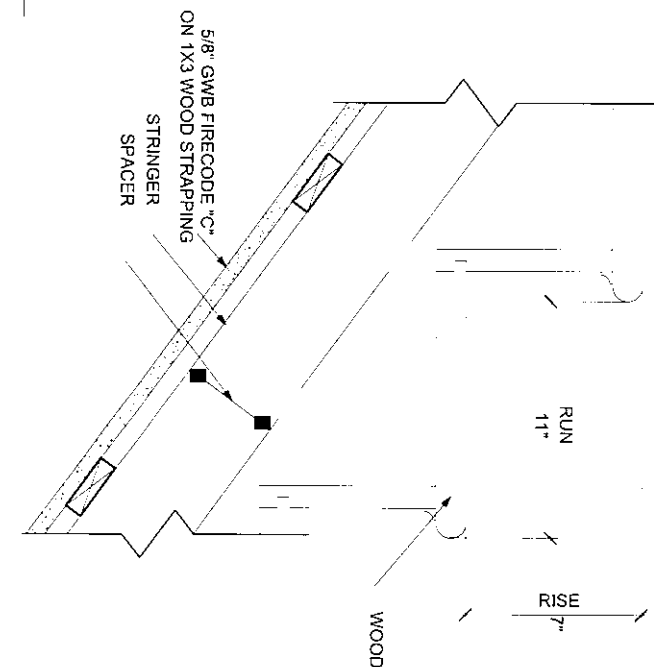


NOTE:
CONTRACTOR SHALL PERFORM ALL WORKS IN COMPLIANCE WITH THE COMMONWEALTH OF MASSACHUSETTS (10TH EDITION OF THE MBSC 780 CMR) (2021 IBC AND THE COMMONWEALTH OF MASSACHUSETTS AMENDMENT TO THE INTERNATIONAL COMMERCIAL CODE 2021) AND THE CITY OF HAVERHILL ORDINANCES.

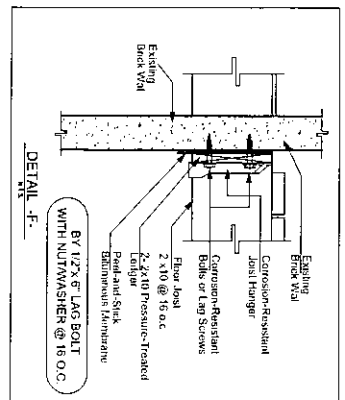

NOTE:
CONTRACTOR SHALL BEFORE START WORK
VERIFY EVERY DIMENSION AND HEIGHT

FRAMING NOTES:
1. ALL HANGERS ARE BY SIMPSON STRONG TIE
2. FASTEN R rafters TO EXTERIOR WALL DOUBLE TOP PLATE WITH SIMPSON STRONG H2.5A HURRICANE TIES.
3. HOT DIP & GALVANIZED HANGERS EXPOSED TO WEATHER.
4. SCREWS AND NAILS TO BE STAINLESS WHEN EXPOSED TO WEATHER.
5. FOR A SINGLE 2x8 OR 2x10 USE LUS26, FOR A DOUBLE 2x8 OR DOUBLE 2x10 USE LUS28-FOR A SINGLE 2x10 USE LUS28, FOR A DOUBLE 2x10 USE LUS28-2.

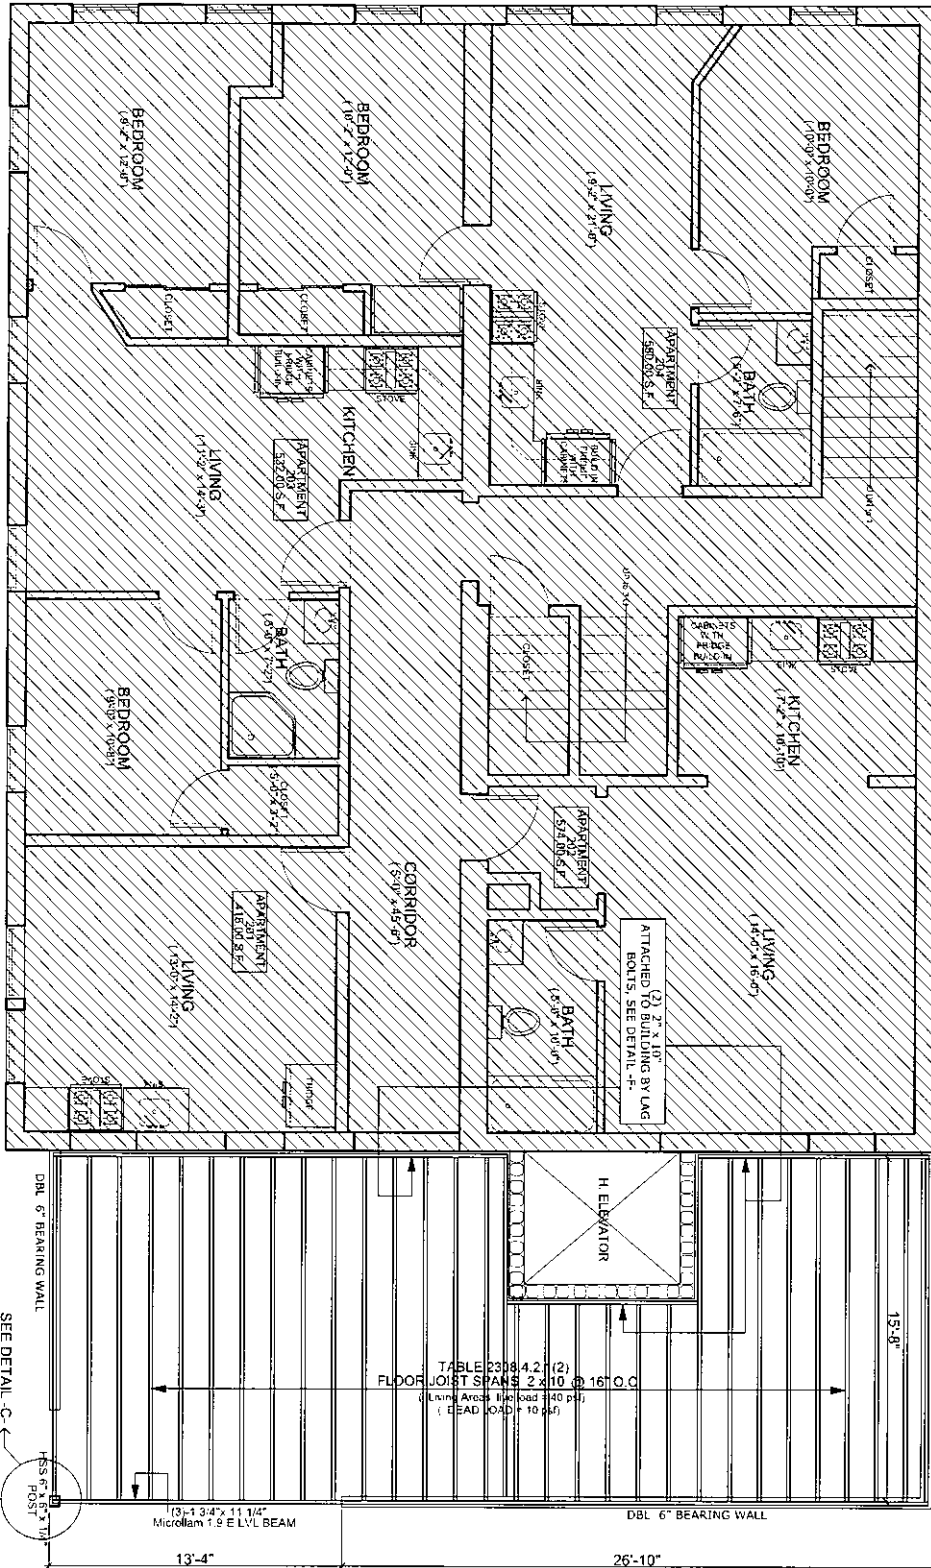

1ST FLOOR FRAMING PLAN
SCALE 1/4"=1'-0"



GJ DESIGN GROUP LLC
Assoc. AIA
Professional Designer

118 WOODLAND ST LAWRENCE MA 01841
978-601-2844 FAX 978-208-1335
E. MAIL: lach.o7812@gmail.com
NOTE: THIS DESIGN IS THE INTELLECTUAL PROPERTY OF G. JIMENEZ GROUP. THEREFORE, IT IS PROHIBITED TO COPY, PARTIAL OR COMPLETE, THIS DESIGN WITHOUT THE AUTHORIZATION OF THE AUTHOR.

PROJECT: COMMERCIAL RESIDENTIAL BUILDING
ADDRESS: 125 MERRIMACK ST. HAVERHILL MA 01830
OWNER: DAVINCI MINI APTS-JONY PEREZ
PETITIONER: DAVINCI MINI APTS-JONY PEREZ

REVISED BY:
APPROVED BY:
DRAWN BY: GILBERTO JIMENEZ
DATE: 7/28/2025

FRAMING PLAN
13THS
32
41

MJD incorporated made these plans to comply with owners and builders' specifications. At the owners' and builders' expense and responsibility, MJD incorporated is not liable for any errors once construction has begun, while MJD incorporated made every effort to prepare this plan to avoid mistakes, the maker cannot guarantee that all dimensions and other details are correct and other parties responsible after that.

NOTE:
CONTRACTOR SHALL BEFORE START WORK
VERIFY EVERY DIMENTION AND HEIGHT

PRAISING NOTES:

1. ALL HANGERS ARE BY SIMPSON STRONG TIE



2. FASTEN RAFTERS TO EXTERIOR WALL, DOUBLE TOP PLATE WITH SIMPSON STRONG #2 5d HURD-CANE TIES.


3. HOT DIP & GALVANIZE HANGERS EXPOSED TO WEATHER

4. SCREWS AND NAILS TO BE STAINLESS WHEN EXPOSED TO WEATHER

5. FOR A SINGLE 2x6 OR 2x8 USE LUS26, FOR A DOUBLE 2x6 OR DOUBLE 2x8 USE LUS26-2.


FOR A SINGLE 2x10 USE LUS28, FOR A DOUBLE 2x10 USE LUS28-2.

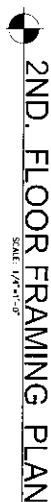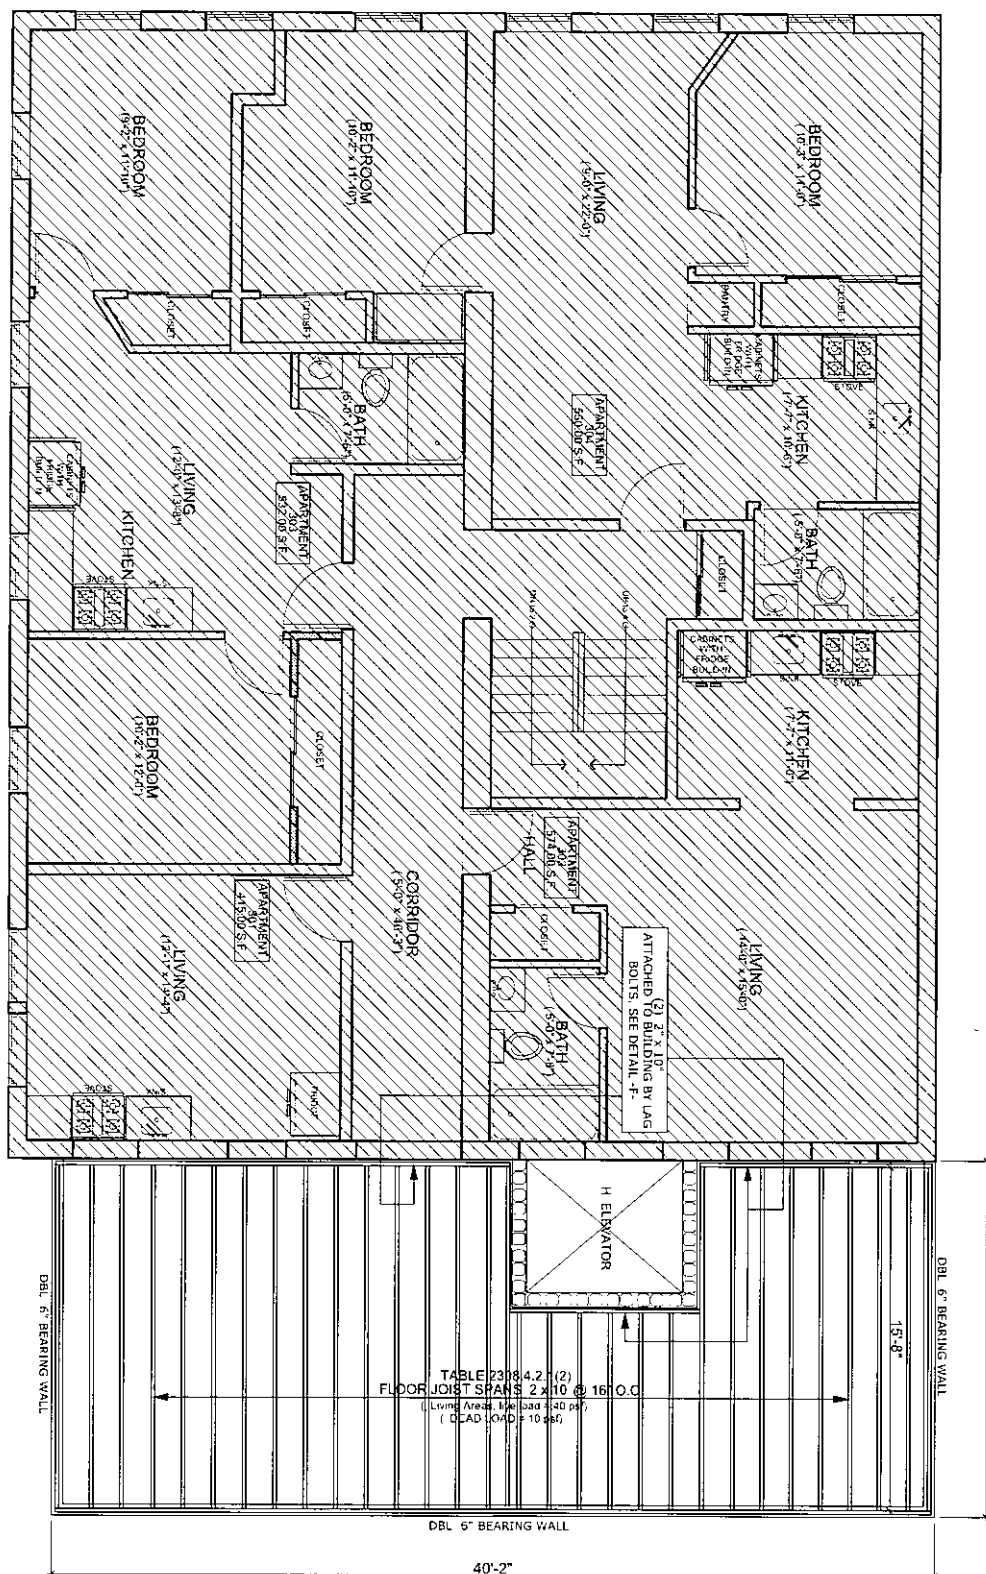

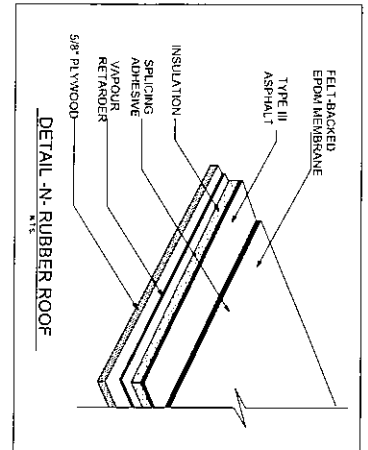


NOTE:
CONTRACTOR SHALL BEFORE START WORK
VERIFY EVERY DIMENSION AND HEIGHT

FRAMING NOTES:
1. ALL FRAMERS ARE BY SIMPSON STRONG TIE
2. FASTEN RAFTERS TO EXTERIOR WALL DOUBLE TOP
3. PLATE WITH SIMPSON STRONG TIE 2X HURRICANE TIES
4. 3X DIPS SAIL VANE HANGERS EXPOSED TO WEATHER
5. SCORP AND VANS TO BE STAINLESS WHEN EXPOSED TO WEATHER
6. FOR A SINGLE RAKE 2X USE LUS2X, FOR DOUBLE 2X OR DOUBLE 2X
USE LUS2X-2 FOR A SINGLE 2X10 USE LUS2X FOR A DOUBLE 2X10 USE

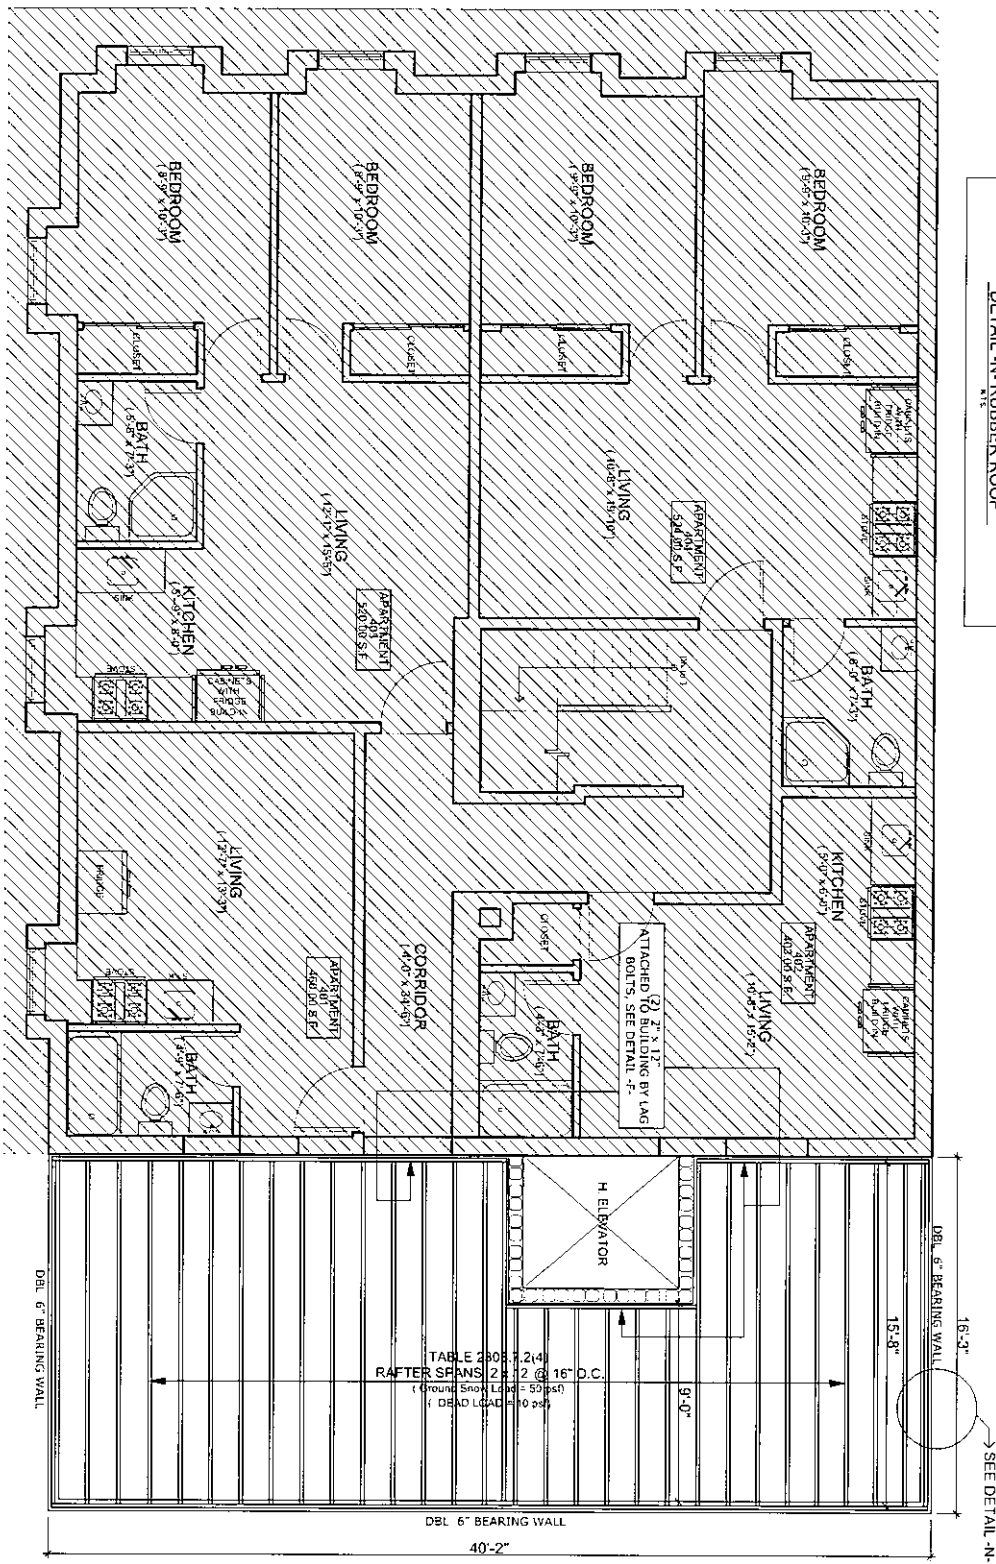

ROOF FRAMING PLAN
SCALE 1/8\"/>

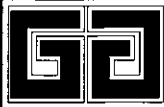

GJ DESIGN GROUP LLC
Assoc. AIA
Professional Designer

118 WOODLAND ST LAWRENCE MA 01841
978-601-2844 FAX 978-208-1335
E. MAIL lach.o7812@gmail.com
NOT: THIS DESIGN IS THE INTELLECTUAL PROPERTY OF
GILBERTO JIMENEZ GROUP THEREFORE THIS
DESIGN WILL BE THE PROPERTY OF THE AUTHOR

PROJECT: COMMERCIAL RESIDENTIAL BUILDING
ADDRESS: 125 MERRIMACK ST. HAVERHILL MA 01830
OWNER: DAVINCI MINI APTS-JONY PEREZ
PETITIONER: DAVINCI MINI APTS-JONY PEREZ

REVISED BY:
APPROVED BY:
DRAWN BY: GILBERTO JIMENEZ
DATE: 7/28/2025

FRAMING PLAN
SHEET 1 35 41

JOIST HANGER SCHEDULE

JOISTS	HANGER	FACE NAILS	TOP FLANGE NAILS	JOIST NAILS
(SINGLE) 2x6 OR 2x8	LUS26	(4) 10d	N/A	(4) 10d
(DOUBLE) 2x6 OR 2x8	LUS26-2	(4) 16d	N/A	(4) 16d
(SINGLE) 2x10 OR 2x12	LUS210	(8) 10d	N/A	(4) 10d
(DOUBLE) 2x10 OR 2x12	LUS210-2	(8) 16d x 3"	N/A	(6) 16d x 3"
RAFTERS 2x10	LSSR210Z	(14) 10d x 2 1/2"	N/A	(10) 10d x 2 1/2"
RAFTERS 2x12	LSSR212Z	(14) 10d x 2 1/2"	N/A	(10) 10d x 2 1/2"
(2) 1 1/2" x 1 1/2" LVL	MCU363-SDS	(24) 1/2" x 2 1/2" SDS	N/A	(16) 1/2" x 2 1/2" SDS

WEATHING/NAILING SCHEDULE

LOCATION	APA RATED/CEC APPROVED SHEATHING	MIN. PLYWOOD THICKNESS	BLOCKED PANEL EDOES REQ.	COMMON NAIL SIZE	PERIMETER PANEL EDGES & DIAPHRAGM BOUNDARIES	OTHER PANEL EDGES	INTERMEDIATE FRAMING MEMBER	NOTES
FLOOR	AVANTECH SHEATHING	3/4"	NO	8	6" O.C.	N/A	12" O.C.	
SHEAR WALL	ZIP SYSTEM SHEATHING	3/4"	YES	8	6" O.C.	N/A	12" O.C.	
ROOF	ZIP SYSTEM ROOF SHEATHING	3/4"	NO	8	6" O.C.	N/A	12" O.C.	

STRUCTURAL NOTES

- GENERAL NOTES
 - ALL WORK SHALL CONFORM TO THE FOLLOWING STANDARDS
 - MASSACHUSETTS COMMERCIAL CODE 780 CMR
 - MINIMUM DESIGN LOADS FOR BUILDINGS AND OTHER STRUCTURES - ASCE 7-10
 - NATIONAL DESIGN SPECIFICATION FOR WOOD CONSTRUCTION - AFPA NDS-2005
 - ALL CONTRACTORS SHALL BE RESPONSIBLE FOR ALL CONSTRUCTION MEANS, METHODS, COORDINATION OF OTHER TRADES, AND THE TECHNIQUES TO PRODUCE A SOUND AND QUALITY PROJECT. SHORING IS THE RESPONSIBILITY OF THE CONTRACTOR.
 - ALL CONTRACTORS SHALL VERIFY AND COORDINATE ALL DIMENSIONS AND DETAILS RELATED TO THIS PROJECT. CONTRACTORS MUST INFORM ALL DISCREPANCIES BEFORE PROCEEDING.
 - ALL DETAILS AND NOTES SHOWN ON THE CONTRACT DOCUMENTS ARE TYPICAL FOR ALL SIMILAR CONDITIONS EXCEPT WHERE SPECIFICALLY REQUIRED OTHERWISE.
 - NO MAIN FRAMING OR STRUCTURAL MEMBERS ARE TO BE MODIFIED, ALTERED, OR CUT WITHOUT THE APPROVAL.
 - ALL CONTRACTORS SHALL BE RESPONSIBLE FOR ALL JOB SAFETY DURING CONSTRUCTION, INCLUDING BUT NOT LIMITED TO SHEETING, SHORING, AND GUTTING STRUCTURES, BARRIERS, AND SIGNAGE.
- STRUCTURAL LOADS
 - PER MASSACHUSETTS STATE BUILDING CODE - 10TH EDITION
 - DESIGN LOADS FOR BUILDING AND OTHER STRUCTURES - ASCE 7-10
 - EXPOSURE B
 - GROUND SNOW LOAD 50 PSF
 - UNBALANCED SNOW LOAD (ADDITIONAL ALLOWANCES FOR DRIFTING AND SLIDING SNOW) LIVE LOADS-LIVING SPACE 40 PSF
 - FOURWORK - ACI 318-05
 - SPECIFICATIONS FOR STRUCTURAL CONCRETE FOR BUILDINGS ACI 301-05
 - COLD WEATHER CONCRETING ACI 306
 - DETAILING REINFORCING STEEL ACI 315-05
 - BUILDING CODE REQUIREMENTS FOR REINFORCED CONCRETE ACI 318-11
 - BUILDING CODE REQUIREMENTS FOR PLAN CONCRETE ACI 322-05

WOOD FRAMING

- ALL WOOD FRAMING SHALL CONFORM TO THE FOLLOWING STANDARDS:
 - MASSACHUSETTS COMMERCIAL CODE 780 CMR
 - INTERNATIONAL BUILDING CODE - 2003 EDITION
 - NATIONAL DESIGN SPECIFICATION FOR WOOD CONSTRUCTION AFPA NDS-2005
- ALL FRAMING MEMBERS SHALL BE NO. 1 / NO. 2 OR BETTER WITH AL MAXIMUM MOISTURE CONTENT OF 19% UNLESS NOTED OTHERWISE.
- DESIGN VALUES SHALL BE:
 - ENGINEERED LUMBER PRODUCTS SHALL HAVE THE FOLLOWING DESIGN VALUES OR BETTER:
 - COLUMNS GRADE 3100 F_b 3.109 PSI, F_c 1.1 x 1000 PSI, E=1,800,000 PSI
 - BEAMS GRADE 3100 F_b 3.109 PSI, F_c = 265 PSI, E=2,000,000 PSI
 - ALL LUMBER AND PLYWOOD SHALL BE GRADE STAMPED BY THE APPROPRIATE MANUFACTURER'S ASSOCIATION FOR THE APPROPRIATE USE.
 - ROOF 19x27 SQUARE EDGE PLYWOOD WITH FRAMING CLIPS
 - FLOORS 23x27 TONGUE & GROOVE PLYWOOD
 - WALLS 15x27 PLYWOOD
- ROOF AND WALL SHEATHING SHALL COMPLY WITH THE FOLLOWING:
 - APA RATED SHEATHING EXPOSURE 1 OR 2
 - ROOF SHEATHING SHALL HAVE A 4020 SPANNING
 - ROOF SHEATHING SHALL HAVE ONE PANEL EDGE CLIP BETWEEN EACH SUPPORT
 - LEAVE A 1/8" EXPANSION GAP BETWEEN ALL PANELS AS REQUIRED BY APA
 - INSTALL SHEETS WITH FACE GRAIN PERPENDICULAR TO SUPPORTING MEMBERS
- ALL WOOD THAT CONTACTS CONCRETE, MASONRY, OR EARTH SHALL BE PRESSURE TREATED (PT) WITH A CCA-C 0.40 PROCESS SEE MANUFACTURER'S RECOMMENDATIONS FOR FASTENING TO PT WOOD.
- ALL FRAMING SHALL BE PLUMB, TRUE, AND ADEQUATELY BRACED SUCH THAT THE STRUCTURE IS RIGID AND BEARS FULLY WITHOUT THE USE OF SHIMS.
- BUILD UP ALL FRAMING MEMBERS WITH 16D NAILS AT 16" O.C. MAXIMUM UNLESS NOTED OTHERWISE. PROVIDE PLYWOOD FILTERS BETWEEN MEMBERS TO MATCH WALL THICKNESS.
- PROVIDE SOLID BLOCKING UNDER ALL CONCENTRATED LOADS. PROVIDE CONTINUITY TO TOP OF FOUNDATION OR FOOTING.
- PROVIDE A DOUBLE TOP PLATE FOR ALL EXTERIOR WALLS W/ SPLICES STAGGERED BY 4 FEET MIN.
- FASTENERS SHALL COMPLY WITH THE FOLLOWING:
 - NAILS SHALL BE COMMON WIRE NAILS, GALVANIZED @ EXPOSED FRAMING
 - BOLTS, NUTS, AND WASHER SHALL BE ASTM A-307, HOT DIP GALVANIZED AT EXTERIOR EXPOSED FRAMING CONFORMING TO ASTM A153
 - ALL WOOD MEMBERS TO BE NAILED PER THE MASSACHUSETTS RESIDENTIAL CODE 780 CMR 51.00
 - PLYWOOD SHALL BE NAILED AT 6" O.C. AT ALL JOINTS AND EDGES & AT 10" O.C. AT OTHER SUPPORTS. GLUE PLYWOOD SUB-FLOORS TO JOISTS BEFORE NAILING WITH CONSTRUCTION ADHESIVE.
 - PROVIDE DOUBLE JOISTS UNDER PARALLEL PARTITION WALLS AT ALL FLOORS UNLESS OTHERWISE NOTED

STRUCTURAL NOTES



GJ DESIGN GROUP LLC
Assoc. AIA
Professional Designer

118 WOODLAND ST LAWRENCE MA 01841
978-601-2844 FAX 978-208-1335
E. MAIL lach.o7812@gmail.com

NOT TO BE USED ON OTHER PROJECTS WITHOUT THE WRITTEN PERMISSION OF THE DESIGNER. THE DESIGNER'S SEAL AND SIGNATURE ARE REQUIRED FOR ALL PROJECTS. THE DESIGNER'S SEAL AND SIGNATURE ARE REQUIRED FOR ALL PROJECTS.

PROJECT: COMMERCIAL RESIDENTIAL BUILDING
ADDRESS: 125 MERRIMACK ST. HAVERHILL MA 01830
OWNER: DAVINCI MINI APTS-JONY PEREZ
PETITIONER: DAVINCI MINI APTS-JONY PEREZ

REVISED BY:
APPROVED BY:
DRAWN BY: GILBERTO JIMENEZ
DATE: 7/28/2025

STRUCTURAL NOTES


SHEET 1
36
41

ELECTRICAL SPECIFICATIONS:

1. THE ESTIMATE FOR THE ELECTRICAL WILL NOT INCLUDE ANY CHARGES FROM THE UTILITY COMPANY RELATED TO THE INSTALLATION OF THE MAIN ELECTRICAL SERVICE PANEL. THE ELECTRICAL SERVICE WILL BE A 400 AMP, THREE-PHASE, FOUR-WIRE OVERHEAD SERVICE RUNNING TO THE BUILDING.
2. ALL BRANCH CIRCUITS, SUB-PANELS, FEEDERS TO SUB-PANELS, ETC., WILL BE SIZED ACCORDING TO LOAD CALCULATIONS AS SPECIFIED BY THE NATIONAL ELECTRICAL CODE (NEC).
3. SUB-FEEDERS AS WELL AS MAIN FEEDER WIRE WILL BE ALUMINUM AND SIZED ACCORDING TO NEC STANDARDS.
4. WE WILL PROVIDE THE POWER WIRING ONLY FOR THE HVAC EQUIPMENT (CONTROL WIRING THE RESPONSIBILITY OF OTHERS).
5. THE FINAL FIRE ALARM COST WILL BE DETERMINED ONCE THE PLANS ARE APPROVED BY THE HAVERHILL FIRE DEPARTMENT.
6. ALL LIGHTING FIXTURES USED WILL BE THE RESPONSIBILITY OF THE OWNER.
7. WE WILL SUBMIT A SET OF FINAL ELECTRICAL PLANS OUTLINING WHAT WE WILL DO IN COMPLETING THE ELECTRICAL WORK FOR THE PROJECT.

LEGEND:

	DUPLEX RECEPTACLE		ELECTRICAL BREAKER PANEL
	DEDICATED RECEPTACLE		CEILING OUTLET LIGHTING
	GFI DUPLEX RECEPTACLE		2 x 4 LAMP OUTLET LIGHTING
	240V RECEPTACLE		WALL MOUNTED LIGHTS
	SAFETY DISCONNECT SWITCH		BATHROOM EXHAUST FAN
	LIGHTING SWITCH @ 48"		50 CFM 0.90 AMP S CEILING/WALL MOUNTED
	3 WAY LIGHTING SWITCH @ 48"		MONOXIDE DETECTOR
	SMOKE DETECTOR		
	COMBO MONOXIDE/CARBON DETECTOR		

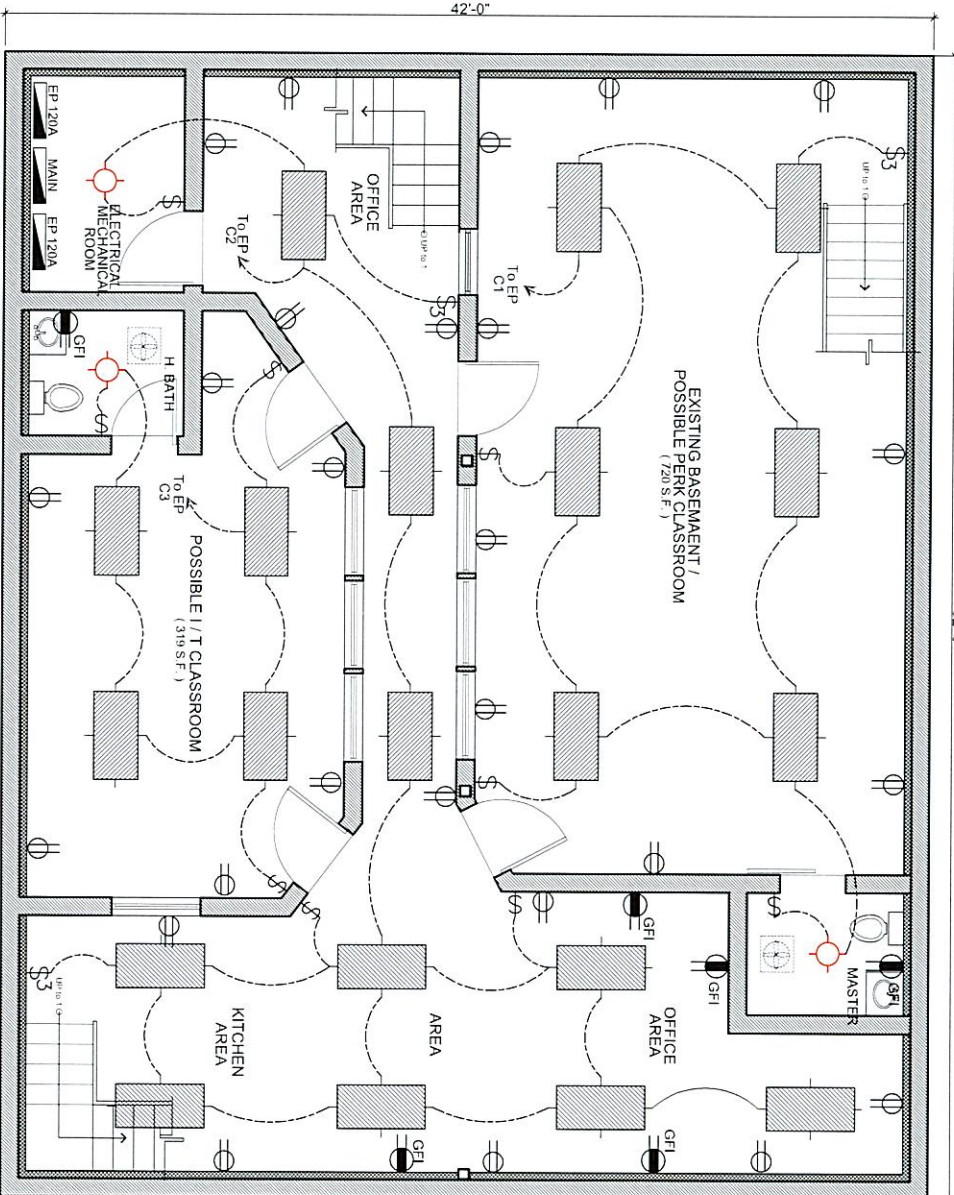

PROPOSED BASEMENT FLOOR PLAN (ELECTRICAL)

SCALE 1/4"=1'-0"



GJ DESIGN GROUP LLC
Assoc. AIA
Professional Designer

118 WOODLAND ST LAWRENCE MA 01841
978-601-2844 FAX 978-208-1335
E. MAIL lach.o7812@gmail.com
NOTE: THIS DESIGN IS THE INTELLECTUAL PROPERTY OF GILBERTO JIMENEZ GROUP. THEREFORE IT IS PROHIBITED COPY PARTIALLY OR COMPLETELY THIS DESIGN WITHOUT THE AUTHORIZATION OF THE AUTHOR.


PROJECT: COMMERCIAL RESIDENTIAL BUILDING
ADDRESS: 125 MERRIMACK ST. HAVERHILL MA 01830
OWNER: DAVINCI MINI APTS-JONY PEREZ
PETITIONER: DAVINCI MINI APTS-JONY PEREZ

REVISED BY:
APPROVED BY:
DRAWN BY: GILBERTO JIMENEZ
DATE: 7/28/2025

ELECTRICAL PLAN
13THS
37/41

GENERAL NOTES:

1. ALL WORK SHALL COMPLY WITH STATE AND LOCAL BUILDING CODES AND REGULATIONS.
2. CONTRACTOR SHALL BE SOLELY RESPONSIBLE FOR ALL CONSTRUCTION MEANS, METHODS, TECHNIQUES, AND PROCEDURES.
3. CONTRACTOR SHALL BE RESPONSIBLE FOR ALL ASPECTS DURING BUILDING CONSTRUCTION AND SHALL PROVIDE ADEQUATE SHORING AND BRACING TO ENSURE SUCH SAFETY.
4. ALL DIMENSIONS AND SITE CONDITIONS SHALL BE FIELD VERIFIED AND SHALL BE THE RESPONSIBILITY OF THE CONTRACTOR. NOTIFY THE OWNER OR DESIGNER OF ANY DISCREPANCY PRIOR TO COMMENCEMENT OF WORK.
5. IT SHALL BE THE RESPONSIBILITY OF THE CONTRACTOR TO LOCATE ALL EXISTING UTILITIES, AND TO PROTECT THEM FROM DAMAGE.
6. ALL DETAILS, SECTIONS, NOTES, OR REFERENCE TO OTHER DRAWINGS ARE INTENDED TO BE TYPICAL.
7. DURING CONSTRUCTION, AND PRIOR TO THE INCORPORATION OF ANY CHANGES, REVISIONS, MODIFICATIONS OR DEVIATION FROM THE CONSTRUCTION DOCUMENT, CONTRACTOR SHALL BRING TO THE ATTENTION OF THE OWNER OR DESIGNER AND OBTAIN APPROVAL FROM THE BUILDING INSPECTOR BEFORE PROCEEDING WITH THE WORK.
8. SPECIFIC NOTES AND DETAILS ON THE DRAWINGS SHALL TAKE PRECEDENCE OVER GENERAL NOTES AND TYPICAL DETAILS, WHERE NO DETAILS ARE SHOWN, CONSTRUCTION SHALL CONFORM TO SIMILAR WORK ON THE PROJECT.
9. GENERAL CONTRACTOR SHALL VERIFY ALL DIMENSIONS PRIOR TO STARTING CONSTRUCTION.
10. CONTRACTOR SHALL PERFORM ALL WORKS IN COMPLIANCE WITH THE COMMONWEALTH OF MASSACHUSETTS (107TH EDITION OF THE MBSG/780 CWM) (2021 IBC AND THE COMMONWEALTH OF MASSACHUSETTS AMENDMENT TO THE INTERNATIONAL COMMERCIAL CODE 2021) AND THE CITY OF HAVERHILL ORDINANCES.

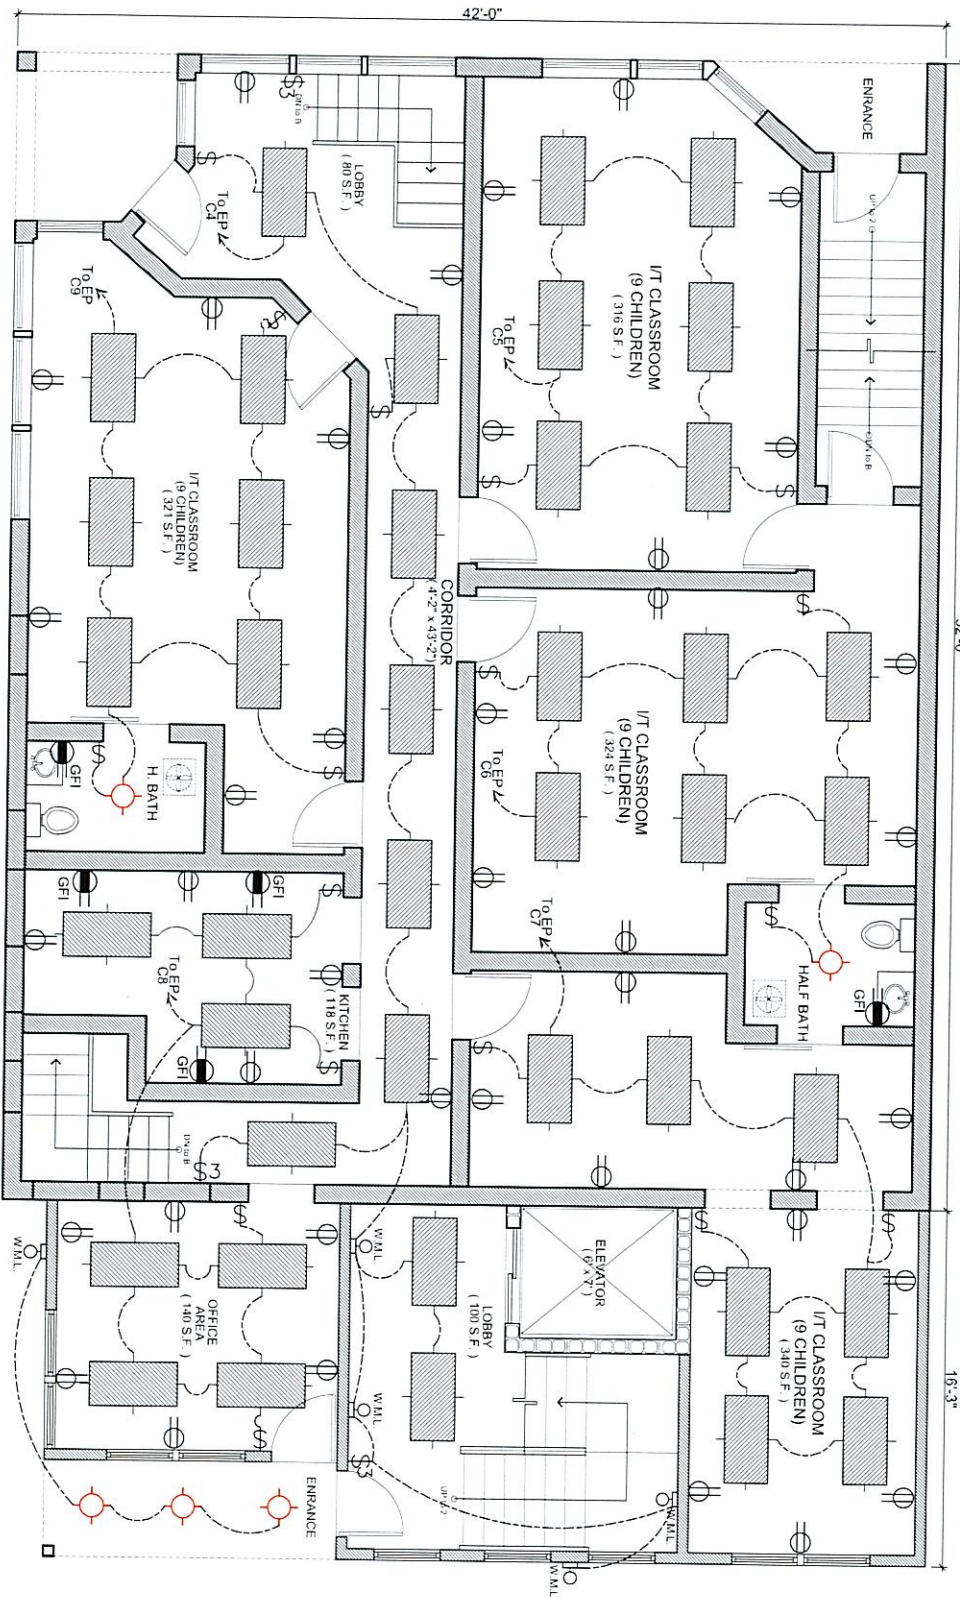

(ELECTRICAL)
PROPOSED FIRST FLOOR PLAN
SCALE: 1/4"=1'-0"



GJ
DESIGN GROUP LLC
Assoc. AIA
Professional Designer

118 WOODLAND ST LAWRENCE MA 01841
978-601-2844 FAX 978-208-1335
E. MAIL lach.o7812@gmail.com
NOTE: THIS DESIGN IS THE INTELLECTUAL PROPERTY OF GILBERTO JIMENEZ GROUP. THEREFORE IT IS PROHIBITED. COPY PARTIALLY OR COMPLETELY THIS DESIGN WITHOUT THE AUTHORIZATION OF THE AUTHOR

PROJECT: COMMERCIAL RESIDENTIAL BUILDING
ADDRESS: 125 MERRIMACK ST. HAVERHILL MA 01830
OWNER: DAVINCI MINI APTS-JONY PEREZ
PETITIONER: DAVINCI MINI APTS-JONY PEREZ

REVISED BY:
APPROVED BY:
DRAWN BY: GILBERTO JIMENEZ
DATE: 7/28/2025


ELECTRICAL PLAN
1 38 41

ELECTRICAL SPECIFICATIONS:

1. THE ESTIMATE FOR THE ELECTRICAL WILL NOT INCLUDE ANY CHARGES FROM THE UTILITY COMPANY RELATED TO THE INSTALLATION OF THE MAIN ELECTRICAL SERVICE (E.M.S.). THE MAIN ELECTRICAL SERVICE WILL BE A 400 AMP, THREE-PHASE, FOUR-WIRE OVERHEAD SERVICE RUNNING TO THE BUILDING.)
2. ALL BRANCH CIRCUITS, SUB-PANELS, FEEDERS TO SUB-PANELS, ETC. WILL BE SIZED ACCORDING TO LOAD CALCULATIONS AS SPECIFIED BY THE NATIONAL ELECTRICAL CODE (NEC).
3. SUB-FEEDERS AS WELL AS MAIN FEEDER WIRE WILL BE ALUMINUM AND SIZED ACCORDING TO NEC STANDARDS.
4. WE WILL PROVIDE THE POWER WIRING ONLY FOR THE HVAC EQUIPMENT (CONTROL WIRING THE RESPONSIBILITY OF OTHERS).
5. THE FINAL FIRE ALARM COST WILL BE DETERMINED ONCE THE PLANS ARE APPROVED BY THE HAVERHILL FIRE DEPARTMENT.
6. ALL LIGHTING FIXTURES USED WILL BE THE RESPONSIBILITY OF THE OWNER.
7. WE WILL SUBMIT A SET OF FINAL ELECTRICAL PLANS OUTLINING WHAT WE WILL DO IN COMPLETING THE ELECTRICAL WORK FOR THE PROJECT.

ELECTRICAL NOTES:

1. CONTRACTOR SHALL FURNISH ALL LABOR MATERIALS AND EQUIPMENT FOR COMPLETE ELECTRICAL INSTALLATION IN ACCORDANCE WITH THESE DRAWINGS.
2. COMPLY WITH THE NEC AND THE MASSACHUSETTS BUILDING CODE.
3. OBTAIN ALL PERMITS FOR WORK UNDER THIS CONTRACT.
4. NO APPLIANCES OUTLETS SHALL BE INSTALLED BELOW BASE FLOOD ELEV. ARCHITECTURAL FEATURES.
5. CONTRACTOR SHALL VISIT THE SITE TO FAMILIARIZE HIMSELF WITH ALL EXISTING CONDITIONS.
6. A/C COMPRESSOR SHALL BE INSTALLED ABOVE BASE FLOOD ELEV.
7. MINIMUM COVER SHALL BE 24".
8. OUTDOOR CONDUITS SHALL BE SCHEDULE 40 PVC.
9. ALL MOUNTING HARDWARE SHALL BE BY CONTRACTOR.
10. ELECTRICAL OUTLETS BELOW BASE ELEV. SHALL BE INSTALLED AT THE HIGHEST PERMITTED ELEV AND SHALL BE INSTALLED (SEPARATE) AS INDEPENDANT CIRCUITS FROM THOSE IN THE HABITABLE AREAS.
11. MAIN CIRCUIT BRK PANELS SHALL BE LOCATED ABOVE BASE FLOOD ELEV.

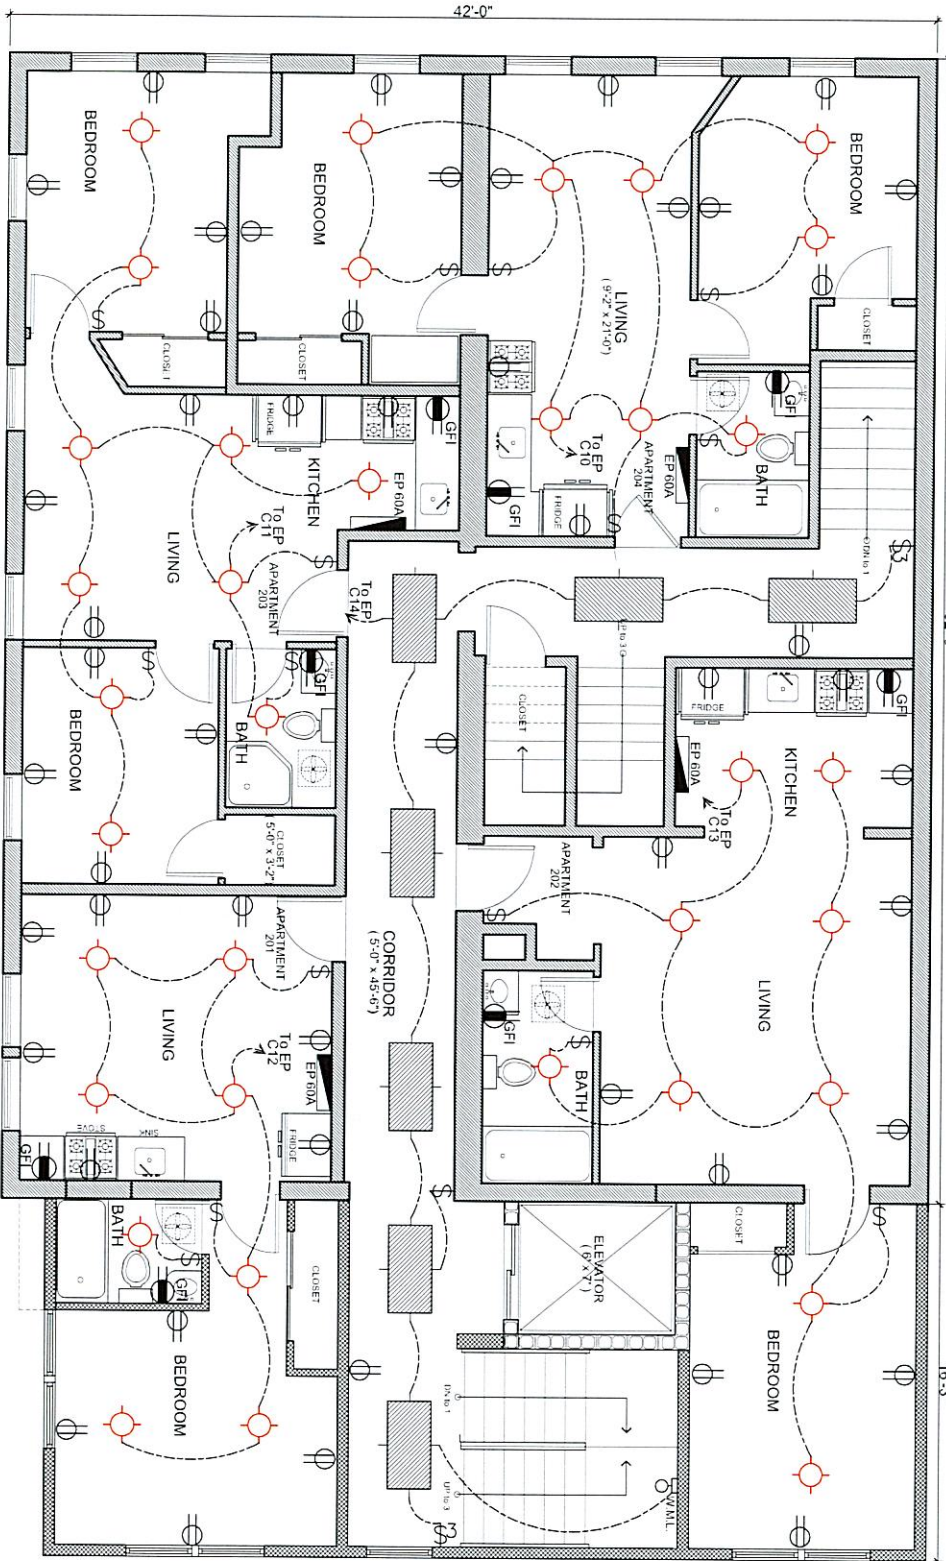

(ELECTRICAL)
PROPOSED SECOND FLOOR PLAN

SCALE: 1/4"=1'-0"



GJ
DESIGN GROUP LLC
Assoc. AIA
Professional Designer

118 WOODLAND ST LAWRENCE MA 01841
978-601-2844 FAX 978-208-1335
E. MAIL lach.o7812@gmail.com

NOTE: THIS DESIGN IS THE INTELLECTUAL PROPERTY OF GILBERTO JIMENEZ GROUP. THEREFORE IT IS PROHIBITED COPY PARTIALLY OR COMPLETELY THIS DESIGN WITHOUT THE AUTHORIZATION OF THE AUTHOR

PROJECT: COMMERCIAL RESIDENTIAL BUILDING
ADDRESS: 125 MERRIMACK ST. HAVERHILL MA 01830
OWNER: DAVINCI MINI APTS-JONY PEREZ
PETITIONER: DAVINCI MINI APTS-JONY PEREZ

REVISED BY:
APPROVED BY:
DRAWN BY: GILBERTO JIMENEZ
DATE: 7/28/2025


ELECTRICAL
PLAN
1 39
41

ELECTRICAL SPECIFICATIONS:

1. THE ESTIMATE FOR THE ELECTRICAL WILL NOT INCLUDE ANY CHARGES FROM THE UTILITY COMPANY RELATED TO THE INSTALLATION OF THE MAIN ELECTRICAL SERVICE. (THE MAIN ELECTRICAL SERVICE WILL BE A 400 AMP, THREE-PHASE, FOUR-WIRE OVERHEAD SERVICE RUNNING TO THE BUILDING.)
2. ALL BRANCH CIRCUITS, SUB-PANELS, FEEDERS TO SUB-PANELS, ETC. WILL BE SIZED ACCORDING TO LOAD CALCULATIONS AS SPECIFIED BY THE NATIONAL ELECTRICAL CODE (NEC).
3. SUB-FEEDERS, AS WELL AS MAIN FEEDER WIRE WILL BE ALUMINUM AND SIZED ACCORDING TO NEC STANDARDS.
4. WE WILL PROVIDE THE POWER WIRING ONLY FOR THE HVAC EQUIPMENT (CONTROL WIRING THE RESPONSIBILITY OF OTHERS).
5. THE FINAL FIRE ALARM COST WILL BE DETERMINED ONCE THE PLANS ARE APPROVED BY THE HAVERHILL FIRE DEPARTMENT.
6. ALL LIGHTING FIXTURES USED WILL BE THE RESPONSIBILITY OF THE OWNER.
7. WE WILL SUBMIT A SET OF FINAL ELECTRICAL PLANS OUTLINING WHAT WE WILL DO IN COMPLETING THE ELECTRICAL WORK FOR THE PROJECT.

LEGEND:

	DUPLEX RECEPTACLE		ELECTRICAL BREAKER PANEL
	DEDICATED RECEPTACLE		CEILING OUTLET LIGHTING
	GFI DUPLEX RECEPTACLE		2 x 4 LAMP OUTLET LIGHTING
	240V RECEPTACLE		WALL MOUNTED LIGHTS
	SAFETY DISCONNECT SWITCH		BATHROOM EXHAUST FAN
	LIGHTING SWITCH @ 48"		50 CFM 0.50 AMPs CEILING/WALL MOUNTED
	3WAY LIGHTING SWITCH @ 48"		
	SMOKE DETECTOR		
	COMBO MONOXIDE/CARBON DETECTOR		MONOXIDE DETECTOR

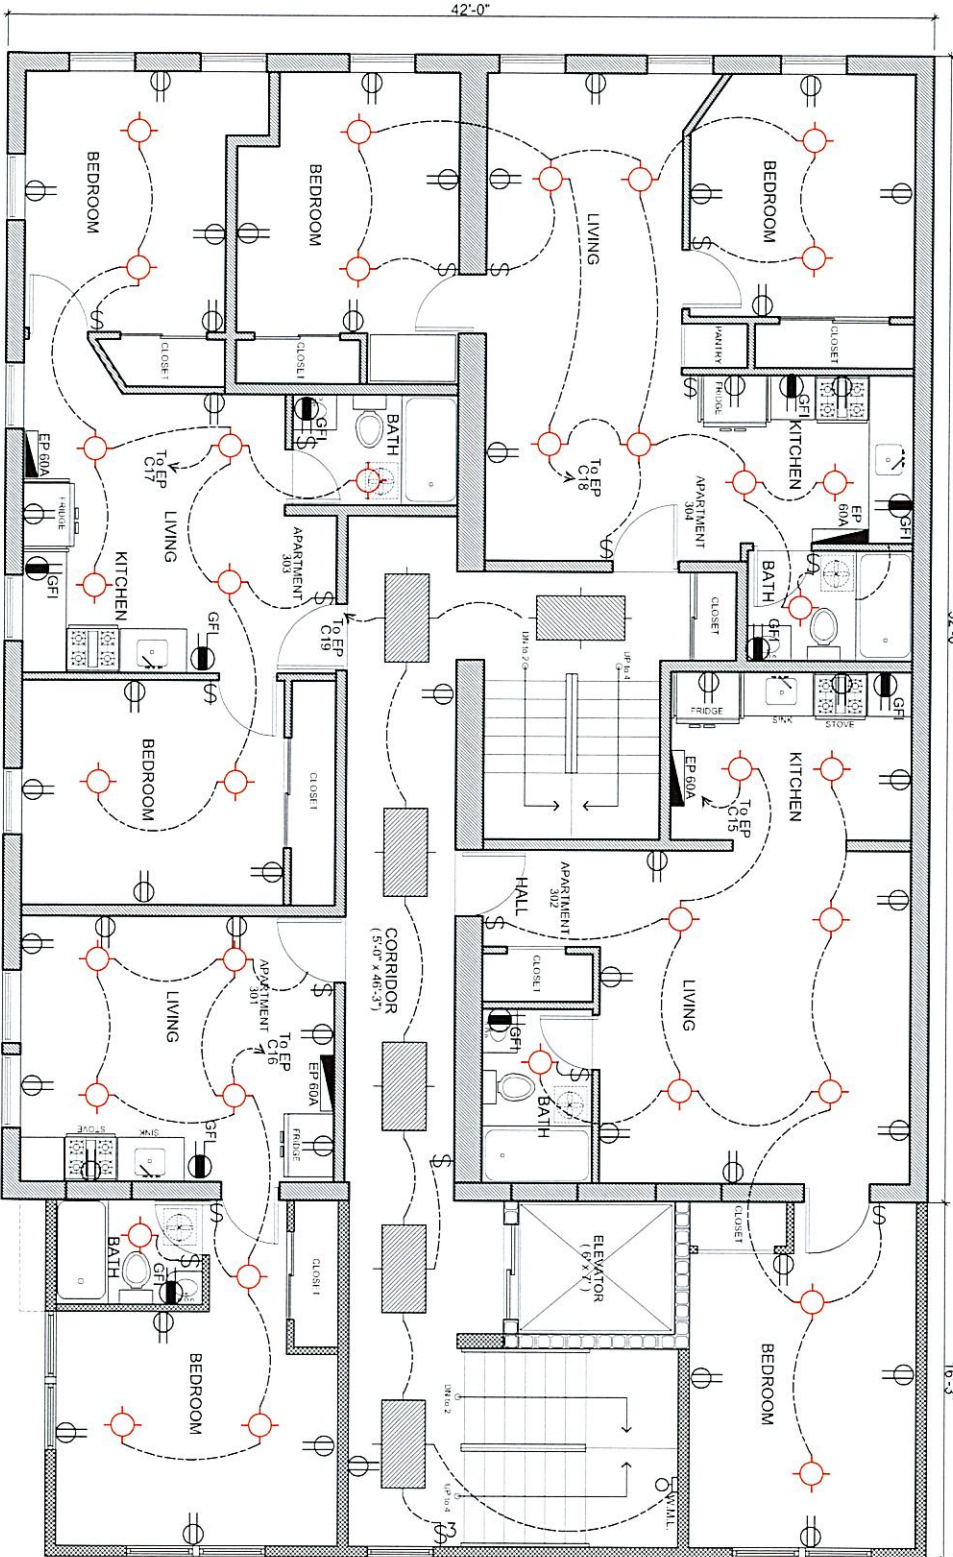

(ELECTRICAL)
PROPOSED THIRD FLOOR PLAN

SCALE: 1/8" = 1'-0"



GJ DESIGN GROUP LLC
Assoc. AIA
Professional Designer

118 WOODLAND ST LAWRENCE MA 01841
978-601-2644 FAX 978-208-1335
E. MAIL: lach.o7812@gmail.com

NOTE: THIS DESIGN IS THE INTELLECTUAL PROPERTY OF GILBERTO JIMENEZ GROUP. THEREFORE IT IS PROHIBITED COPY PARTIALLY OR COMPLETELY THIS DESIGN WITHOUT THE AUTHORIZATION OF THE AUTHOR.


PROJECT: COMMERCIAL RESIDENTIAL BUILDING
ADDRESS: 125 MERRIMACK ST. HAVERHILL MA 01830
OWNER: DAVINCI MINI APTS-JONY PEREZ
PETITIONER: DAVINCI MINI APTS-JONY PEREZ

REVISED BY:
APPROVED BY:
DRAWN BY: GILBERTO JIMENEZ
DATE: 7/28/2025

ELECTRICAL PLAN
1 40
41

1. ALL WORK SHALL COMPLY WITH STATE AND LOCAL BUILDING CODES AND REGULATIONS.
2. CONTRACTOR SHALL BE SOLELY RESPONSIBLE FOR ALL CONSTRUCTION MEANS, METHODS, TECHNIQUES, AND PROCEDURES.
3. CONTRACTOR SHALL BE RESPONSIBLE FOR ALL ASPECTS OF THE CONSTRUCTION AND SHALL PROVIDE ADEQUATE SHORING AND BRACING TO ENSURE SUCH SAFETY.
4. ALL DIMENSIONS AND SITE CONDITIONS SHALL BE FIELD VERIFIED AND SHALL BE THE RESPONSIBILITY OF THE CONTRACTOR. NOTIFY THE OWNER OR DESIGNER OF ANY DISCREPANCY PRIOR TO COMMENCEMENT OF WORK.
5. IT SHALL BE THE RESPONSIBILITY OF THE CONTRACTOR TO LOCATE ALL EXISTING UTILITIES, AND TO PROTECT THEM FROM DAMAGE.
6. ALL DETAILS, SECTIONS, NOTES, OR REFERENCE TO OTHER DRAWINGS ARE INTENDED TO BE TYPICAL.
7. DURING CONSTRUCTION, AND PRIOR TO THE INCORPORATION OF ANY CHANGES, REVISIONS, MODIFICATIONS OR DEVIATION FROM THE CONSTRUCTION DOCUMENT, CONTRACTOR SHALL BRING TO THE ATTENTION OF THE OWNER OR DESIGNER BEFORE PROCEEDING WITH THE WORK.
8. SPECIFIC NOTES AND DETAILS ON THE DRAWINGS SHALL TAKE PRECEDENCE OVER GENERAL NOTES AND TYPICAL DETAILS, WHERE NO DETAILS ARE SHOWN CONSTRUCTION SHALL CONFORM TO SIMILAR WORK ON THE PROJECT.
9. GENERAL CONTRACTOR SHALL VERIFY ALL DIMENSIONS PRIOR TO STARTING CONSTRUCTION.
10. CONTRACTOR SHALL PERFORM ALL WORKS IN COMPLIANCE WITH THE COMMONWEALTH OF MASSACHUSETTS (2021 IBC AND THE COMMONWEALTH OF MASSACHUSETTS AMENDMENT TO THE INTERNATIONAL COMMERCIAL CODE 2021) AND THE CITY OF HAVERHILL ORDINANCES.

GENERAL NOTES :

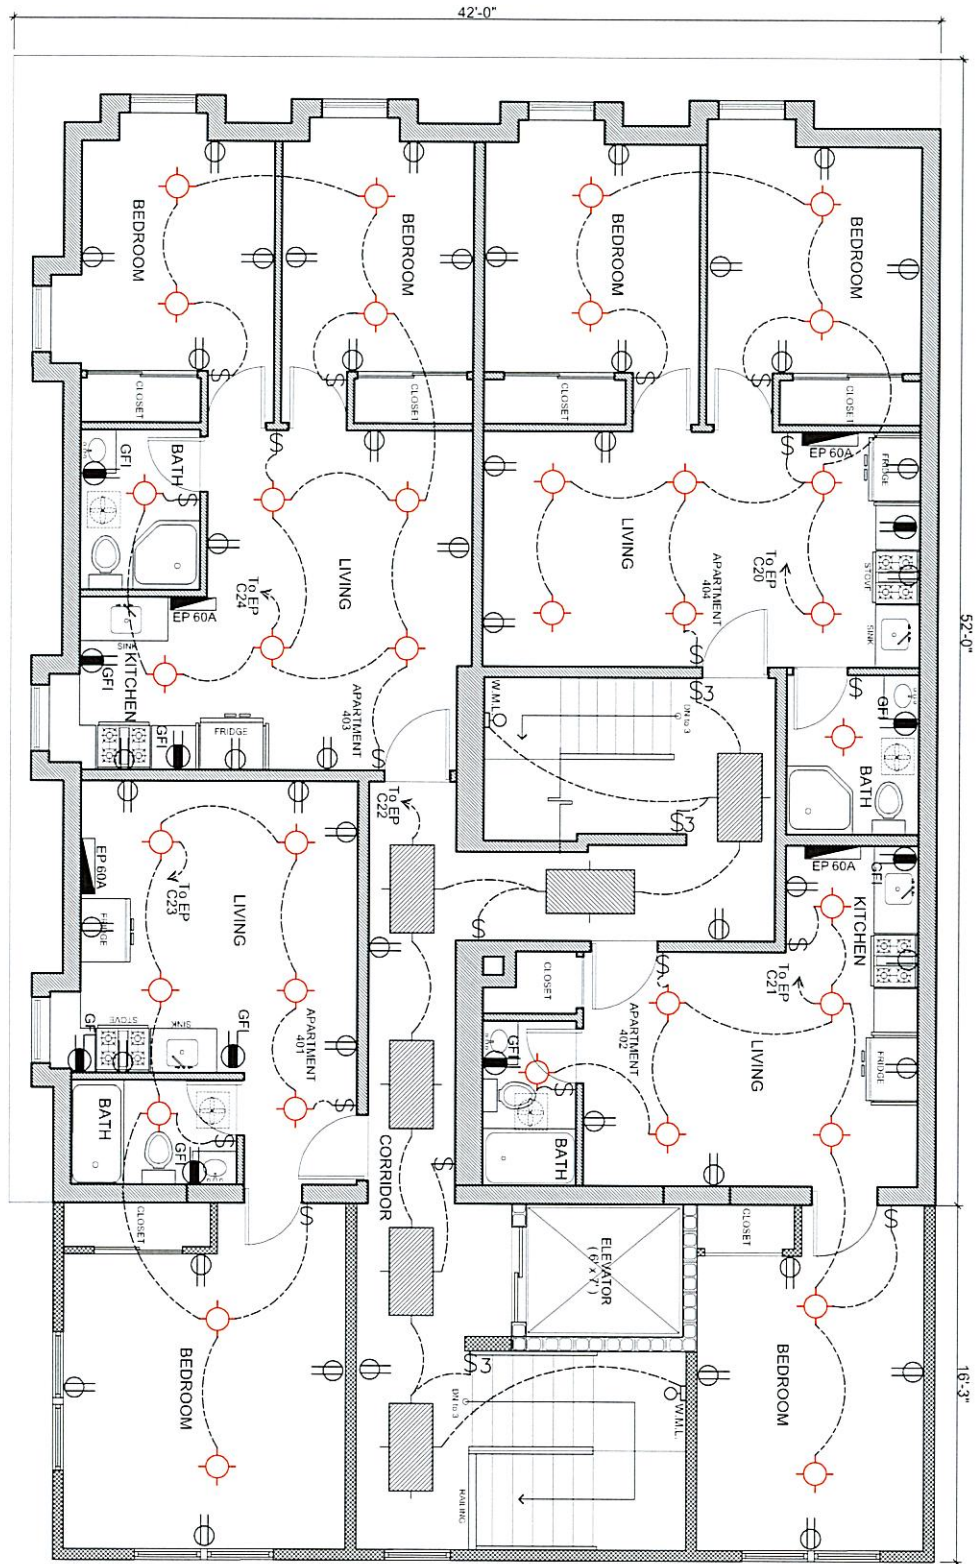

(ELECTRICAL)
PROPOSED FOURTH FLOOR PLAN
SCALE: 1/8"=1'-0"