


LOCUS MAP
SCALE: NOT TO SCALE

REQUIRED PARKING	
512 WASHINGTON - BLOKS 1, 2, 3	13 SPACES

**ZONING TABLE: RH ZONING DISTRICT
(MULTI-FAMILY)**

DESCRIPTION	REQUIRED
MINIMUM LOT FRONTAGE (FT.)	132'-0"
MINIMUM LOT AREA (S.F.)	40,000 S.F.
MINIMUM FRONT YARD (FT.)	25'-0"
MINIMUM SIDE YARD (FT.)	25'-0"
MINIMUM REAR YARD (FT.)	40'-0"
MINIMUM OPEN SPACE	35%
MINIMUM LOT DEPTH	200'-0"

N/F
JOSEPH L. JACOBSON
#200 WASHINGTON ST
MAP 504 BLOCK 245 LOT 4
BK. 41506 PG. 176

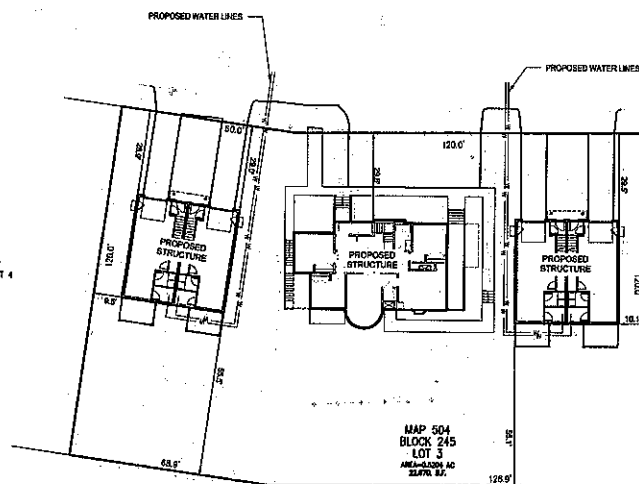

ASSESSOR REFERENCE:

MAP 504 BLOCK 245 LOT 3

WASHINGTON STREET

PUBLIC - WITH VARIES
1971 E.C.L.O. No. 1209

I HEREBY CERTIFY THAT THIS PLAN HAS BEEN PREPARED
IN CONFORMANCE WITH THE RULES AND REGULATIONS OF
THE REGISTRARS OF DEEDS OF THE COMMONWEALTH OF
MASSACHUSETTS.

I FURTHER CERTIFY THAT THE PROPERTY LINES ON THIS
PLAN ARE THE LINES SHOWING EXISTING OWNERSHIPS, AND
THE LINES OF THE STREETS AND WAYS SHOWN ARE
THOSE OF PUBLIC OR PRIVATE STREETS OR WAYS
ALREADY ESTABLISHED AND THAT NO NEW LINES FOR
DIVISION OF EXISTING OWNERSHIP OR FOR NEW WAYS ARE
SHOWN. (MGL CHAPTER 41 SEC 81G)



4/10/26

DATE

FOR REGISTRY USE ONLY

OWNER & APPLICANT:

ESSEX COUNTY HABITAT FOR HUMANITY
14 PARK ST
CAMBRIDGE, MA 02142

KEY REFERENCE DEEDS:

- DEED FROM FEDERAL NATIONAL MORTGAGE ASSOCIATION TO KATHY F. BOUCHER AND DIANE C. BOUCHER DATED MAY 17, 2012 AND RECORDED AT THE SOUTH ESSEX REGISTRY OF DEEDS BOOK 31356 PAGE 78.
- DEED FROM PAUL H. AND TITIANA HOKA TO SOCRATES & POTOLIA YAMAMOURAS DATED NOV 8, 1973 AND RECORDED AT THE SOUTH ESSEX REGISTRY OF DEEDS BOOK 6061 PAGE 778.

KEY REFERENCE PLANS:

- PLAN OF A PORTION OF WASHINGTON STREET, HAVERHILL, MASS. AS WIDENED BY THE COUNTY COMMISSIONERS. BY H. SPORFORD, SURVEYOR. DATED 1871 AND RECORDED AT THE SOUTH ESSEX REGISTRY OF DEEDS E.C.L.O. No. 1209.
- PLAN OF A PORTION OF BEACH STREET, HAVERHILL, MASS. BY JOHN T. DESIGNED, CITY ENGINEER. DATED APRIL, 1883 AND ON FILE WITH THE CITY OF HAVERHILL ENGINEERING DEPARTMENT, SECTION 3A PLAN 20.
- PLAN OF A PORTION OF WILSON STREET, BEACH ST. TO RIVER ST. FOR ACCEPTANCE. BY HARRY W. BAILEY, CITY ENGINEER. DATED SEPT. 1947, ON FILE WITH THE CITY OF HAVERHILL ENGINEERING DEPARTMENT AND RECORDED AT THE SOUTH ESSEX REGISTRY OF DEEDS PLAN BOOK 79 PLAN 51.
- PLAN OF A PORTION OF THE BOWLEY ESTATE, HAVERHILL, MASS. BY H. SPORFORD, SURVEYOR. DATED FEB. 18, 1900 AND RECORDED AT THE SOUTH ESSEX REGISTRY OF DEEDS PLAN BOOK 12 PLAN 18.

GENERAL NOTES:

- THE EXISTING CONDITIONS DEPICTED HEREON ARE TAKEN FROM AN EXISTING CONDITIONS PLAN DATED NOVEMBER 27, 2024. PREPARED AND SIGNED/STAMPED BY MICHAEL J. SERIO, PROFESSIONAL LAND SURVEYOR.
- THE SUBJECT PROPERTY IS NOT LOCATED WITHIN ANY FLOOD ZONE AS ILLUSTRATED BY FEMA MAP 250000000P; EFFECTIVE JULY 3, 2012.
- ELEVATIONS HEREON ARE BASED ON HANDS.
- ORIENTATION IS TO NAD83 MASSACHUSETTS STATE PLANE COORDINATES.
- HORIZONTAL LOCATION OF SITE BENCHMARKS SHOWN ARE APPROXIMATE.
- THE LOCATION OF ALL UNDERGROUND UTILITIES SHOWN HEREON ARE APPROXIMATE AND ARE BASED ON A COMBINATION OF FIELD LOCATIONS AND RECORD DATA ON FILE WITH THE CITY OF HAVERHILL ENGINEERING DEPARTMENT.
- THE SUBJECT PROPERTY IS BENEFITTED BY A SEWER EASEMENT CROSSING ADJUTING PROPERTY AT #102 WASHINGTON STREET TO BEACH STREET AS DESCRIBED IN KEY REFERENCE DEED 2. THIS EASEMENT IS BLANKET IN NATURE AND NOT PLOTTABLE.

LEGEND:

BENCHMARK
CATCH BASIN
DRAIN MANHOLE
HYDRANT
SEWER MANHOLE
WATER GATE VALVE
WATER SHUT-OFF
UTILITY POLE
CONTOUR MAJOR
CONTOUR MINOR
DRAIN LINE
GAS LINE
OVERHEAD WIRE
SEWER LINE
WATER LINE

ABBREVIATIONS

CB CATCH BASIN
CLF CHAINLINK FENCE
DMH DRAIN MANHOLE
EP EDGE OF PAVEMENT
HYD HYDRANT
SMH SEWER MANHOLE
VOC VERTICAL GRANITE CURB
WFD WOOD-FRAMED DWELLING
WG WATER GATE VALVE
WSO WATER SHUT-OFF

N/F
STEPHEN & KATHY PARSONS
#181-123 WILSON ST
MAP 506 BLOCK 225A LOT 13
BK. 37478 PG. 441

N/F
RICARDO ALVARADO LUIS
#121-123 WILSON ST
MAP 506 BLOCK 225A LOT 14
BK. 37478 PG. 441

N/F
NATALIE MOUSSA
#101-103 WILSON ST
MAP 504 BLOCK 245 LOT 5
BK. 34488 PG. 104

SCALE 1"=20'
20 0 20 40 FT

APPLICANT

HAVERHILL BOARD OF APPEALS

DATE:



PCA

Tighe & Bond

The
Morm-Cameron
GROUP, INC.

CIVIL ENGINEERS / ENVIRONMENTAL CONSULTANTS
LAND SURVEYORS / LAND USE PLANNERS
14 ELM STREET, SUITE 200, HAVERHILL, MASSACHUSETTS 01830
P: 978-777-8400, W: WWW.MORMCAMERON.COM

512 WASHINGTON STREET
HAVERHILL, MASSACHUSETTS




REVISIONS

PROJECT NO.: 15115
DRAWN BY: ACH
CHECKED BY: BJ
SCALE: 1"=20'

APRIL 10, 2026

**CERTIFIED
PLOT PLAN**

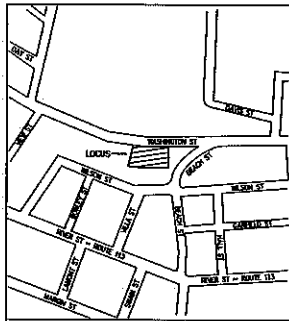


REQUIRED PARKING	
512 WASHINGTON - BLDGS 1, 2, 3	13 SPACES

ZONING TABLE: RH ZONING DISTRICT (MULTI-FAMILY)

DESCRIPTION	REQUIRED
MINIMUM LOT FRONTAGE (FT.)	150'-0"
MINIMUM LOT AREA (S.F.)	40,000 SF
MINIMUM FRONT YARD (FT.)	20'-0"
MINIMUM SIDE YARD (FT.)	20'-0"
MINIMUM REAR YARD (FT.)	40'-0"
MINIMUM OPENSPACE	55%
MINIMUM LOT DEPTH	200'-0"

N/F
JOSEPH L. ABOURK
1500 WASHINGTON ST
MAP 504 BLOCK 245 LOT 4
BK. 41506 PG. 176

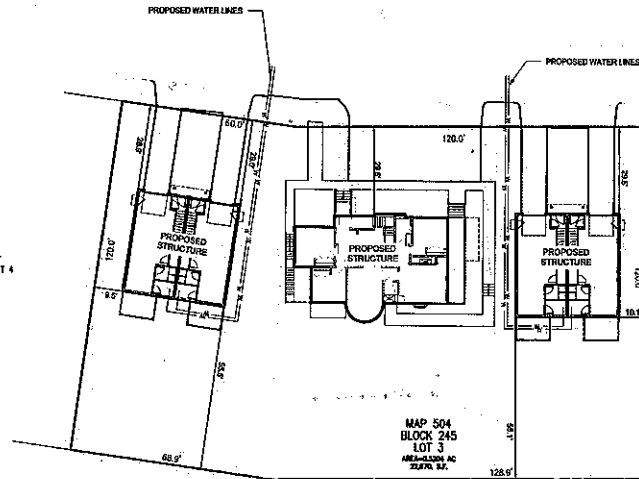

N/F
STEPHEN & KATY PARSONS
8121-123 WILSON ST
MAP 506 BLOCK 252A LOT 13
BK. 37478 PG. 441

N/F
RICARDO ALVARADO LUIS
8121-123 WILSON ST
MAP 506 BLOCK 252A LOT 14
BK. 37478 PG. 441

ASSESSOR REFERENCE:

MAP 504 BLOCK 245 LOT 3

WASHINGTON STREET

PUBLIC - 100' WIDE
1571 E.C.D. No. 1209

I HEREBY CERTIFY THAT THIS PLAN HAS BEEN PREPARED IN CONFORMANCE WITH THE RULES AND REGULATIONS OF THE REGISTER OF DEEDS OF THE COMMONWEALTH OF MASSACHUSETTS.

I FURTHER CERTIFY THAT THE PROPERTY LINES ON THIS PLAN ARE THE LINES SURROUNDING EXISTING OWNERSHIP, AND THE LINES OF THE STREETS AND WAYS SHOWN ARE THOSE OF PUBLIC OR PRIVATE STREETS OR WAYS ALREADY ESTABLISHED AND THAT NO NEW LINES FOR DIVISION OF EXISTING OWNERSHIP OR FOR NEW WAYS ARE SHOWN. (MGL CHAPTER 41 SEC. 81D)



4/10/26
DATE

FOR REGISTRY USE ONLY

OWNER & APPLICANT:

ESSEX COUNTY HABITAT FOR HUMANITY
14 PARK ST
CAMBRIDGE, MA 02142

KEY REFERENCE DEEDS:

- DEED FROM FEDERAL NATIONAL MORTGAGE ASSOCIATION TO KETH F. BOWDITCH AND DIANE C. BOWDITCH DATED MAY 17, 2012 AND RECORDED AT THE SOUTH ESSEX REGISTRY OF DEEDS BOOK 31355 PAGE 74.
- DEED FROM PAUL H. AND TRINIA HOMA TO SOCRATES & POTOLIA YANMAROUKAS DATED NOV 3, 1973 AND RECORDED AT THE SOUTH ESSEX REGISTRY OF DEEDS BOOK 6091 PAGE 776.

KEY REFERENCE PLANS:

- PLAN OF A PORTION OF WASHINGTON STREET, HAVERHILL, MASS. AS WIDENED BY THE COUNTY COMMISSIONERS. BY H. SPOTFORD, SURVEYOR. DATED 1871 AND RECORDED AT THE SOUTH ESSEX REGISTRY OF DEEDS E.C.D. No. 1209.
- PLAN OF A PORTION OF BEACH STREET, HAVERHILL, MASS. BY JOHN T. BOWDITCH, CITY ENGINEER. DATED APRIL 1953 AND ON FILE WITH THE CITY OF HAVERHILL ENGINEERING DEPARTMENT, SECTION 3A PLAN 20.
- PLAN OF A PORTION OF WILSON STREET, BEACH ST. TO RIVER ST. FOR ACCEPTANCE. BY HARRY W. BAILEY, CITY ENGINEER. DATED SEPT. 1947. ON FILE WITH THE CITY OF HAVERHILL ENGINEERING DEPARTMENT AND RECORDED AT THE SOUTH ESSEX REGISTRY OF DEEDS PLAN BOOK 79 PLAN 21.
- PLAN OF A PORTION OF THE BOWLEY ESTATE, HAVERHILL, MASS. BY H. SPOTFORD, SURVEYOR. DATED FEB. 19, 1900 AND RECORDED AT THE SOUTH ESSEX REGISTRY OF DEEDS PLAN BOOK 12 PLAN 18.

GENERAL NOTES:

- THE EXISTING CONDITIONS DEPICTED HEREON ARE TAKEN FROM AN EXISTING CONDITIONS PLAN DATED NOVEMBER 27, 2024, PREPARED AND SIGNED/STAMPED BY MICHAEL A. SCOLA, PROFESSIONAL LAND SURVEYOR.
- THE SUBJECT PROPERTY IS NOT LOCATED WITHIN ANY FLOOD ZONE AS ILLUSTRATED BY FEMA MAP 25090C0000P; EFFECTIVE JULY 3, 2012.
- ELEVATIONS HEREON ARE BASED ON NAVD83.
- ORIENTATION IS TO NAD83 MASSACHUSETTS STATE PLANE COORDINATES.
- HORIZONTAL LOCATION OF SITE BENCHMARKS SHOWN ARE APPROXIMATE.
- THE LOCATION OF ALL UNDERGROUND UTILITIES SHOWN HEREON ARE APPROXIMATE AND ARE BASED ON A COMBINATION OF FIELD LOCATIONS AND RECORD DATA ON FILE WITH THE CITY OF HAVERHILL ENGINEERING DEPARTMENT.
- THE SUBJECT PROPERTY IS INCURTED BY A SEWER EASEMENT CROSSING ADJUTING PROPERTY AT 8542 WASHINGTON STREET TO BEACH STREET AS DESCRIBED IN KEY REFERENCE DEED 2. THIS EASEMENT IS BLANKET IN NATURE AND NOT PLOTTABLE.

LEGEND

● BENCHMARK
○ CATCH BASIN
○ CHAINLINK FENCE
○ DRAIN MANHOLE
○ HYDRANT
○ SEWER MANHOLE
○ WATER GATE VALVE
○ WATER SHUT-OFF
○ UTILITY POLE

○ CONTOUR MAJOR
○ CONTOUR MINOR
○ DRAIN LINE
○ GAS LINE
○ OVERHEAD WIRES
○ SEWER LINE
○ WATER LINE

ABBREVIATIONS

CB CATCH BASIN
CLF CHAINLINK FENCE
DM DRAIN MANHOLE
EP EDGE OF PAVEMENT
HYD HYDRANT
HWM HYDROMANHOLE
VGC VERTICAL GRANITE CURB
WFD WOOD-FRAMED DWELLING
WG WATER GATE VALVE
WSO WATER SHUT-OFF

SCALE: 1"=20'
0 20 40 FT

APPLICANT

HAVERHILL BOARD OF APPEALS

DATE



PCA

Tighe & Bond

The
Morin-Cameron
GROUP, INC.

CIVIL ENGINEERS / ENVIRONMENTAL CONSULTANTS
LAND SURVEYORS / LAND USE PLANNERS
14 RIV STREET, DAVENPORT, MASSACHUSETTS 01923
P. 978-777-8344, W. WWW.MORINCAMERON.COM

512 WASHINGTON STREET
HAVERHILL, MASSACHUSETTS



Michael A. Scola



John M. Morin

REVISIONS

PROJECT NO. 18115
DRAWN BY: JCH
CHECKED BY: BU
SCALE: 1"=20'

APRIL 10, 2026

CERTIFIED
PLOT PLAN